


ЛК15'+89 а-90°00' уз.8
ОСС (30°+30°+30°)-720(10-СмЭсп)-1,6-0,75
R-5D, ТУ102-488-95.

337
336
335
334
333
332
331
330
329
328
327
326
325
324

Горизонтальный масштаб 1:1000
Вертикальный масштаб 1:100

Инженерно– геологическая характеристика	
Уг. электросопр. грунтов, Р ом*м	
Угояы	
Отметка земли, м	
Расстояние, м	
Пикетъ, указатель километров	
Полка, выемка, насыпь, засыпка	Планировочные отметки Тип поперечного профиля
Проектные отметки (верх трубы)	
Уклон газопровода %	
Длина участка, м	
Истинная глина, м	
Глубина траншеи, м	
Трубы Ф х S, мм	
Тип изоляции газопровода	
Защита изоляции от механических повреждений	
Балластировка и закрепление газопровода (тип балласта или крепежа кол. шаг)	
Защитный кожух	

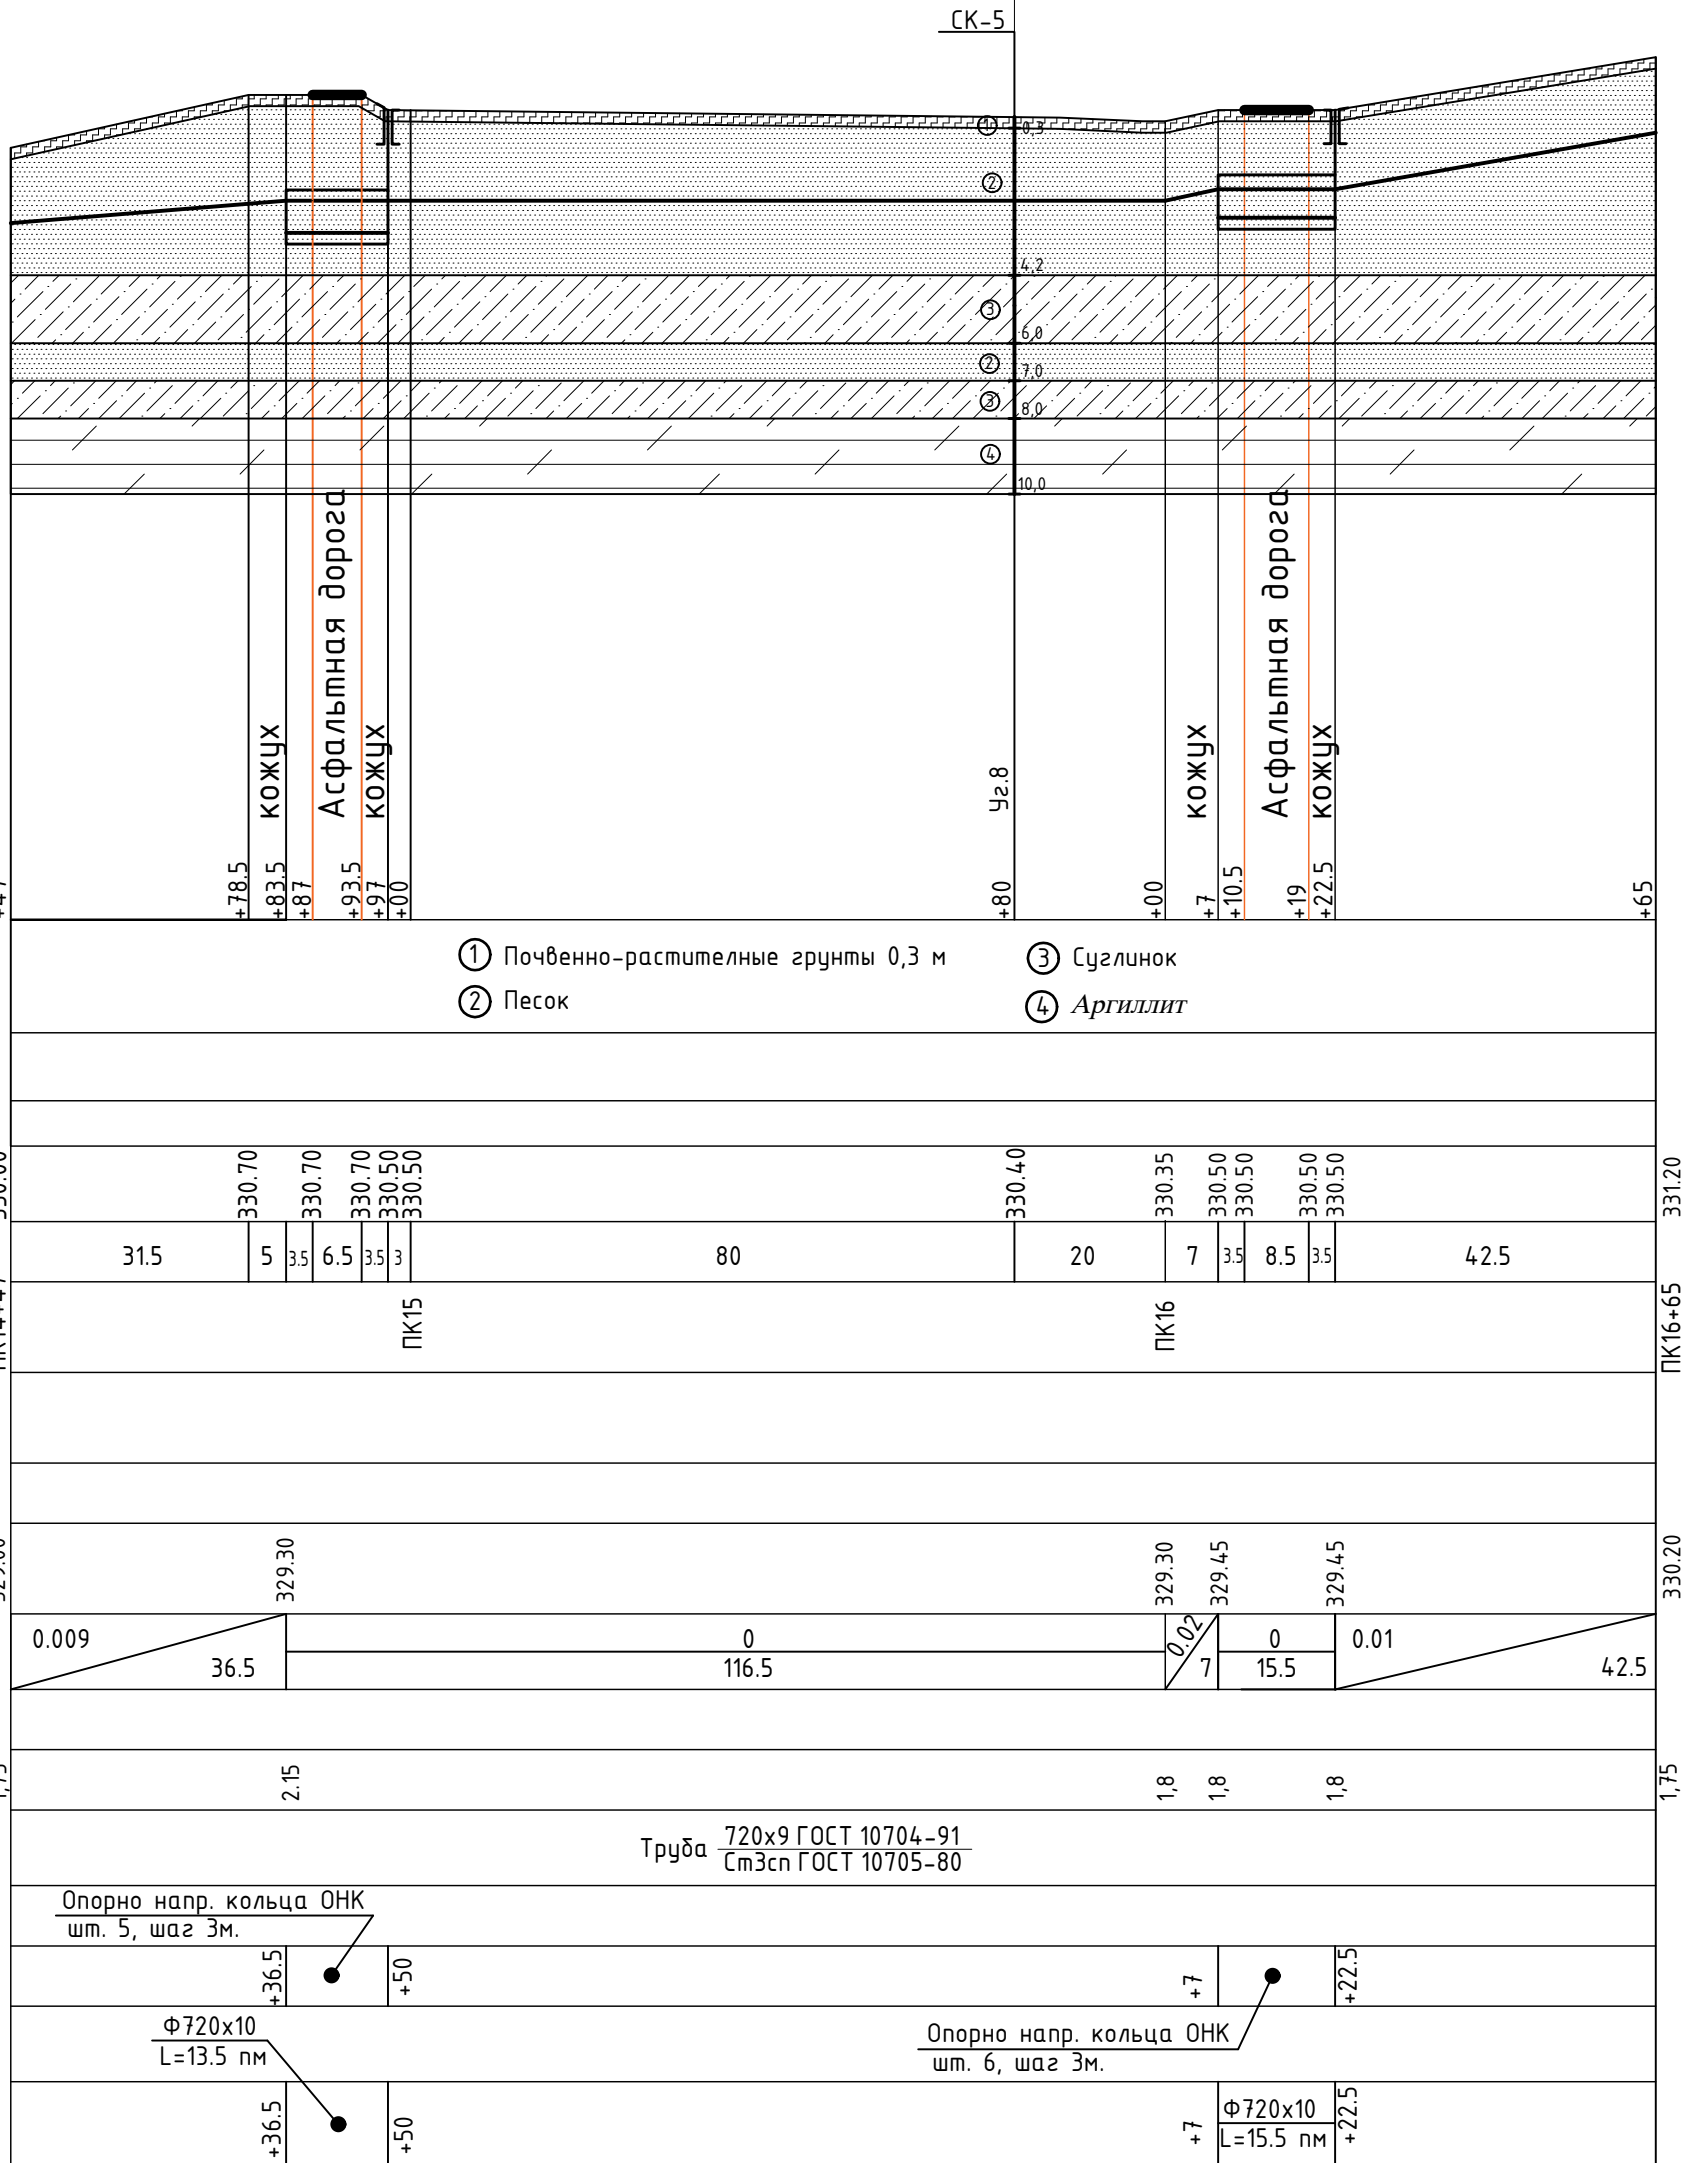

Экспликация деталей и отдельных изделий

№ п.п	Наименование деталей	Ед. изм.	Кол.	Примечание
1	2	3	4	
1	ОСС 30°-720(10-СмЭсп)-1,6-0,75 5D ТУ-102-488-95	шт	13	
2	ОСС 9°-720(10-СмЭсп)-1,6-0,75 5D ТУ-102-488-95	шт	3	
3	ОСС 6°-720(10-СмЭсп)-1,6-0,75 5D ТУ-102-488-95	шт	9	
4	ОСС 3°-720(10-СмЭсп)-1,6-0,75 5D ТУ-102-488-95	шт	4	
5	Отвод 90°-720х10-СмЭсп 1,5Д ГОСТ 17375-2001	шт	1	
6	Тройник 720х10-СмЭсп ГОСТ 17376-2001	шт	1	

Ведомость объемов работ

№ п.п	Наименование работ	Ед. изм.	Кол.	Примечание
1	2	3	4	5
1	Труба 720х9-ПТ-01кл ГОСТ 10704-91 с АКП В-СмЭсп ГОСТ 10706-76	пм	4522	с учетом рубленного пикета
2	Прокладка газопровода Ду700 в равнинно-холмистой местности в грунгах I группы с заглублением (в песках) до дна траншеи на: гл. 1,75/2,0 м гл. 2,25/2,75 м	пм	3433 836 113 140	
3	Контроль монтажных сварных соединений физическими методами, радиографическим 100% Ду700мм	стык	460	
4	Испытание газопровода на прочность давлением 1,5МПа φ720 и на герметичность давлением 1,2 МПа φ720	пм	4522	
5	Изоляция пленкой "Полилен 40-ЛИ-63" в один слой с оберткой "Полилен 40-ОБ-63" в один слой по праймеру "НК-50" кожух Ду1000	пм	58	
6	Опознавательный столб	шт	4	
9	Переход через автомобильную дорогу открытым способом а) Кожух 1020х12 ГОСТ 10704-91 б) опорно-направляющие кольца ОНК в) протаскивание трубы Ду700 в кожух Ду1000 г) Уплотнительные манжеты для концов кожуха Ду1000 марки ГМР 700-1000 д) разборка гравийного покрытия автодороги е) восстановление гравийного покрытия автодороги ж) вывод контрольной трубки под ковер	мест пм шт пм шт	2 58 22 58 8 1,0 1,0 4	
7	Рекультивация земли на пашне а) срезка ПСП мощностью 0,3 м (шир.1,9м) с перемещение ПСП до 15м и обратно	м³	450	
8	Монтаж фасонных изделий	шт	31	
9	Установка шарового крана с пневмогидроприводом для подземной установки Ду700мм, Ру1,6МПа	шт	2	
10	Ограждение кранового узла 4х4м Манжеты Терма-СТМП-720 (трехслойное покрытие для защиты стыков) ТУ 22.21.42-001-82119587-2019	шт	394	

Общие указания

Общие данные смотреть на листе 1;
Продольный профиль трассы газопровода 1 нитки;
Общая на обе нитки ведомость объемов работ приведена на 4 листе.

						029-26-ГСН			
						Магистральный газопровод -отвод со строительством новой ГРС подключением к МГ -отводу "Термиз" для газоснабжения новостроящейся парогазовой электростанции мощностью 1500-1600 МВт в Сурхандарьинской области			
Изм.	Колуч.	Лист	Ндок.	Подп.	Дата				
Нач. отд.						Газопровод высокого давления	Стадия	Лист	Листов
Исполн.							РП	3	3
						Продольный профиль подземной части газопровода высокого давления от ПК0+00 по ПК2+69,5		UZTRANSGAZ «TRANSGAZINJINIRING» MCJ	