




- Общие указания
1. Общие данные смотри на листе 1.
 2. Продольный профиль трассы газопровода смотри на листе 3.
 3. Перед началом работ следует определить точное местоположение существующих коммуникаций шурфованием вручную, глубину их заложения и обозначить предупреждающими и разъясняющими знаками, освещаемыми в ночное время.
 4. На период эксплуатации установить предупреждающие и запрещающие знаки (Ч.ВТ-МГ-86).
 5. Земляные работы в зоне по 2 м в обе стороны от пересечения выполнить без применения ударных инструментов вручную.
 6. Проезд техники через существующие трубопроводы выполнить по специально устройной насыпи, с уложенными железобетонными плитами, которую после окончания строительства газопровода конфигурацию оросительных сетей восстановить.
 7. После окончания строительства газопровода конфигурацию оросительных сетей восстановить.
 8. При пересечении строящегося газопровода с ЛЭП работы производить в присутствии представителей, выдающей ЛЭП, и соблюдением правил технической безопасности и ПУЭ. Строительно-монтажные работы в охранных зонах ЛЭП необходимо выполнять при снятом напряжении.

029-26-ГСН				
Магистральный газопровод - отвод со строительством новой ГРС подведением к МГ - отводу "Тиргиз" для газоснабжения новостроящейся паргазовой электростанции мощностью 1500-1600 МВт в Сурхандарьинской области				
Изм.	Кол.	Лист	Ндок.	Подп.
Испол.	отв.			
Газопровод высокого давления		Стдия	Лист	Листов
газопровода от ПК0+00 по ПК10+46		РП	2	3
План трассы магистрального газопровода от ПК0+00 по ПК10+46		М 1:1000		
		UTRANSKAZ TRANSKAZINING MCH		