



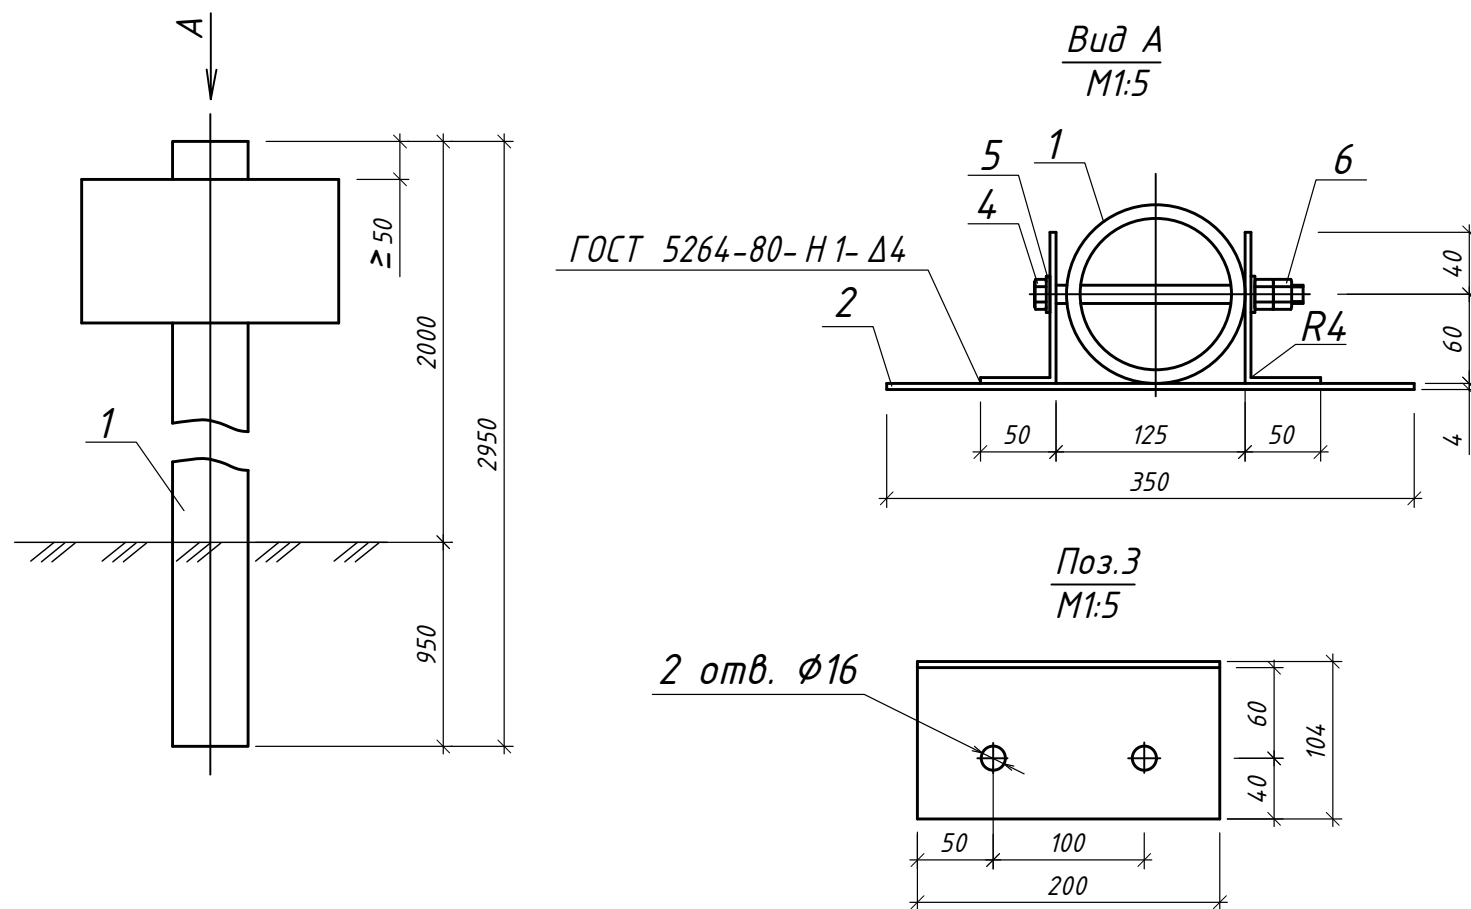

Пример обозначения угла поворота

I. на землях сельхозназначения

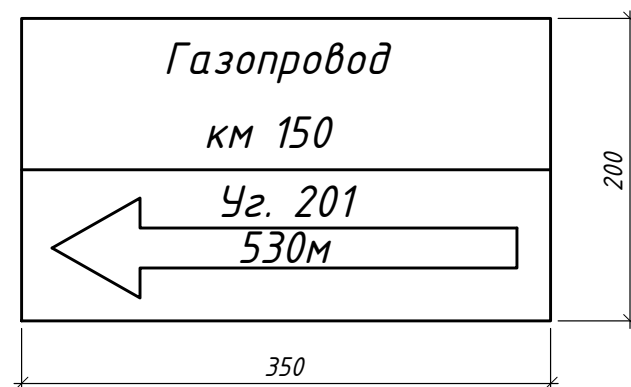

II. на несельскохозяйственных землях



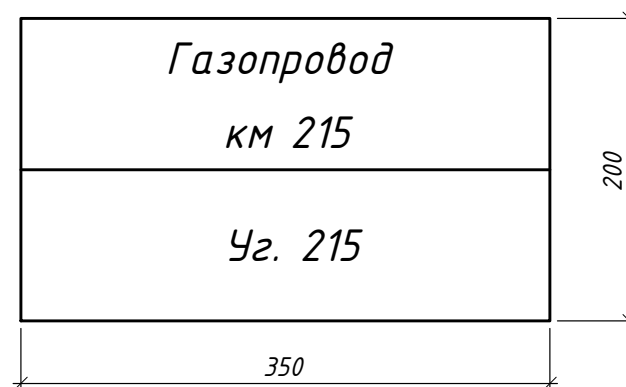


Схема установки опознавательных столбов

I. на землях сельхозназначения

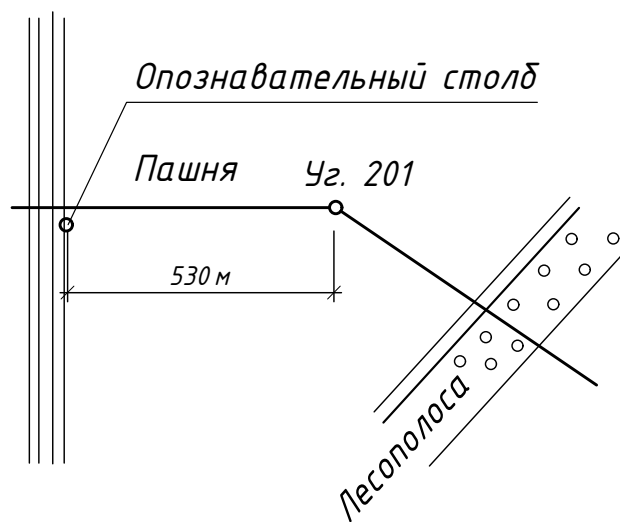

II. на несельскохозяйственных землях

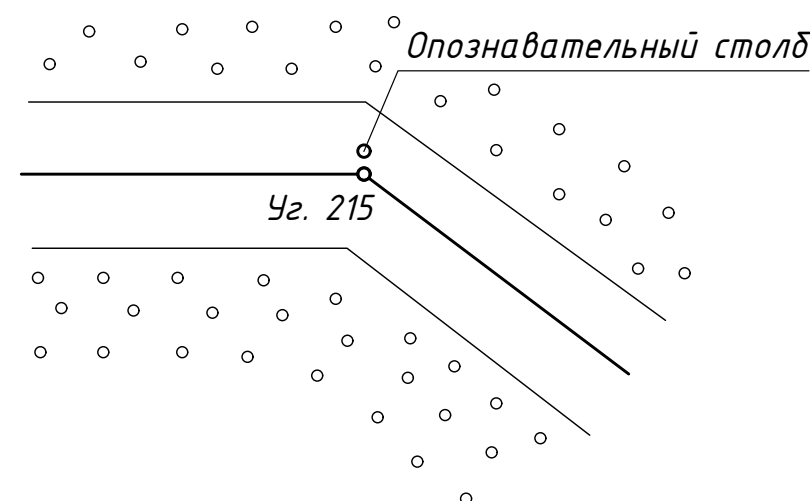

Спецификация

Марка поз.	Обозначение	Наименование	Кол.	Масса ед.,кг	Примечание
1		Труба БНТ 100 ГОСТ1839-80	1	18	А/Ц
		L=2950			
2		Полоса 40x200 ГОСТ103-76	1	2,2	L=350
		Ст.3 ГОСТ535-79			
3		Полоса 40x200 ГОСТ103-76	2	0,82	L=150
		Ст.3 ГОСТ535-79			согнуть
4		Болт М12х170.36 ГОСТ15589-70	2	0,166	
5		Шайба 12.02 ГОСТ11371-78	4	0,0007	
6		Гайка 12.4 ГОСТ15526-70	4	0,024	

Указания по установке опознавательных столбов

- Опознавательные столбы на трассе должны быть установлены на углах поворота - по данному чертежу, а также через 300-500м в пределах видимости (эти функции совмещаются с КИП, п.5.7 "Правил технической эксплуатации магистральных газопроводов").
- При установке опознавательных столбов на сельскохозяйственных землях они выносятся в сторону на границу таких земель (см. схему I) с указанием на стрелке, повернутой в сторону угла поворота, расстояния в метрах до него. На землях несельскохозяйственного назначения опознавательный столб устанавливается непосредственно у угла поворота (см. схему II).
- Указательная пластина (поз. 2) окрашивается белой масляной краской, надписи выполняются черной масляной краской, сам столб окрашивается в оранжевый цвет (п.5.7 "Правила технической эксплуатации магистральных газопроводов").

Привязан к: 002-25-ГСН

Исполн.

Инв. №

85.00-08.00-000;00.08-МР

Магистральный трубопровод

Изм.	Кол.уч.	Лист	№Док.	Подп.	Дата
Гл. спец.	Ромодан				
Рук. гр.	Воронова				
Н. контр.	Воронова				
Ст. инж.	Бойченко				

Опознавательный столб

Стадия

Лист

Листов

ЮЖНИИГИПРОГАЗ