

Территория строящейся ТЭЦ "Сурхандарья"



ПК 22' +01/ПК 21+86 конец трассы II н.
Тройник 720х10-СтЗсп
R-5D, ТУ 102-488-95.

ПК 22'+36 Конец трассы
ПК 21+71 Установка шарового
крана Ду700 Ру1,6

ПК 17+67 а-216°00' уг.10
ОСС (30°+3°)-720(10-СтЗсп)-1,6-0,75
R-5D, ТУ 102-488-95.



ПК 21'+72 Установка шарового
крана Ду700 Ру1,6
ПК 21'+97 а-90°00' уг.11
Отвод 90°-720(10-СтЗсп)-1,6-0,75
R-1,5D, ТУ 102-488-95.

ПК 17'+06 а-147°00' уг.9
ОСС (30°+3°)-720(10-СтЗсп)-1,6-0,75
R-5D, ТУ 102-488-95.

ПК 17'+83 а-144°00' уг.10
ОСС (30°+6°)-720(10-СтЗсп)-1,6-0,75
R-5D, ТУ 102-488-95.

ПК 15+80 а-90°00' уг.8
ОСС (30°+30°+30°)-720(10-СтЗсп)-1,6-0,75
R-5D, ТУ 102-488-95.

ПК 15'+89 а-90°00' уг.8
ОСС (30°+30°+30°)-720(10-СтЗсп)-1,6-0,75
R-5D, ТУ 102-488-95.

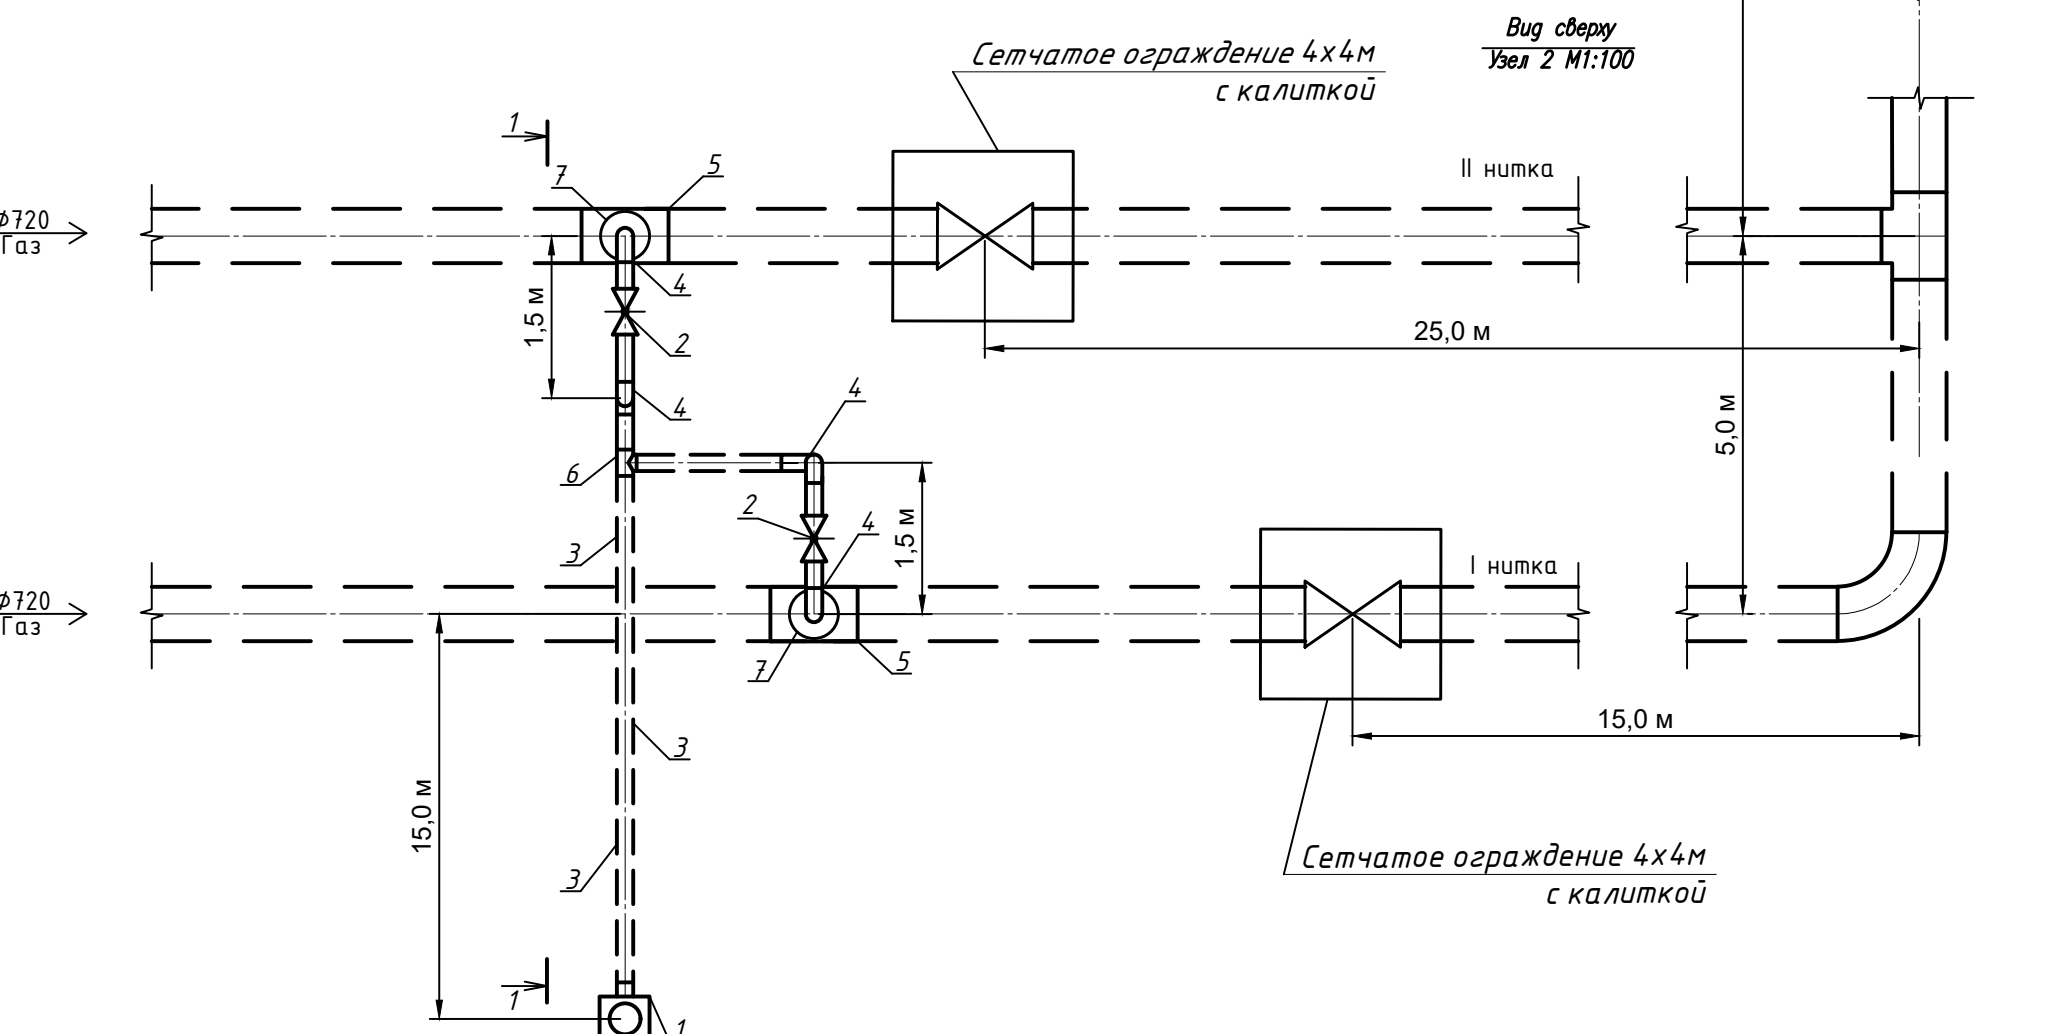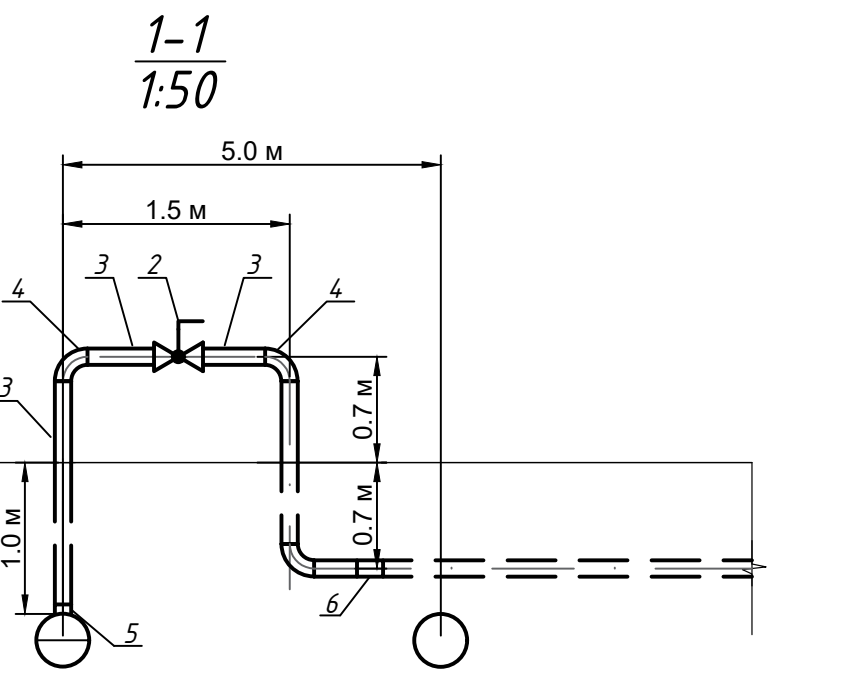

Спецификация					
Поз.	Обозначение	Наименование	Кол.	Масса ед.изм.	Примечание
1	2	3	4	5	6
1	7.402-3-23.000	Свеча правдоульная Ду100 мм	1	29,5	
2	ТУ 28-87-16.25-95	Кран шаровой с ручным приводом на фланцевой установке 11 кг 60 л Ду100 мм, Ру1,6 МПа	2	53	
3	ГОСТ 8732-78 Р 35 ГОСТ 4131-74	Трубка 108 х 6 Отвод 90° 108 х 8	39	53	
4	ГОСТ 17375-2001	Отвод 90° 108 х 8	6	3,8	
5	ТУ 51-29-81	Тройник 120 х 14-325 х 12	2	259	
6	ГОСТ 17376-2001	Тройник 108 х 8	1	4,5	
7	ГОСТ 17376-2001	Переход К 325 х 12-108 х 6	2	16,0	

- Общие указания
- Общие данные смотри на листе 1.
 - Продольный профиль трассы газопровода смотри на листе 3.
 - Перед началом работ следует определить точное местоположение существующих коммуникаций шурфованием вручную, глубину их заложения и обозначить предупреждающими и разъясняющими знаками, освещаемыми в ночное время.
 - На период эксплуатации установить предупреждающие и запрещающие знаки (Ч.ВТ-МГ-86).
 - Земляные работы в зоне по 2 м в обе стороны от пересечения выполнить без применения ударных инструментов вручную.
 - Проезд техники через существующие трубопроводы выполнить по специально устройной насыпи, с уложенными железобетонными плитами, которую после окончания строительства ликвидировать.
 - После окончания строительства газопровода конфигурацию оросительных сетей восстановить.
 - При пересечении строящегося газопровода с ЛЭП работы производить в присутствии представителей, выдающей ЛЭП, и соблюдением правил технической безопасности и ПУЭ. Строительно-монтажные работы в охранных зонах ЛЭП необходимо выполнять при снятом напряжении.

					029-26-ГСН		
					Магистральный газопровод-отвод со строительством новой ГРС подключением к МГ-отводу "Термиз" для газоснабжения новостроящейся парогазовой электростанции мощностью 1500-1600 МВт в Сурхандарьинской области		
Изм.	Коп.уч.	Лист	Изд.	Подп.	Дата	Стадия	Лист
Нач. отд.						РП	2
Исполн.							3
					Газопровод высокого давления		
					План трассы магистрального газопровода от ПК0+00 по ПК10+46 М 1:1000		
					UZTRANS-GAZ «TRANSGAZINJINIRING» MCHJ		