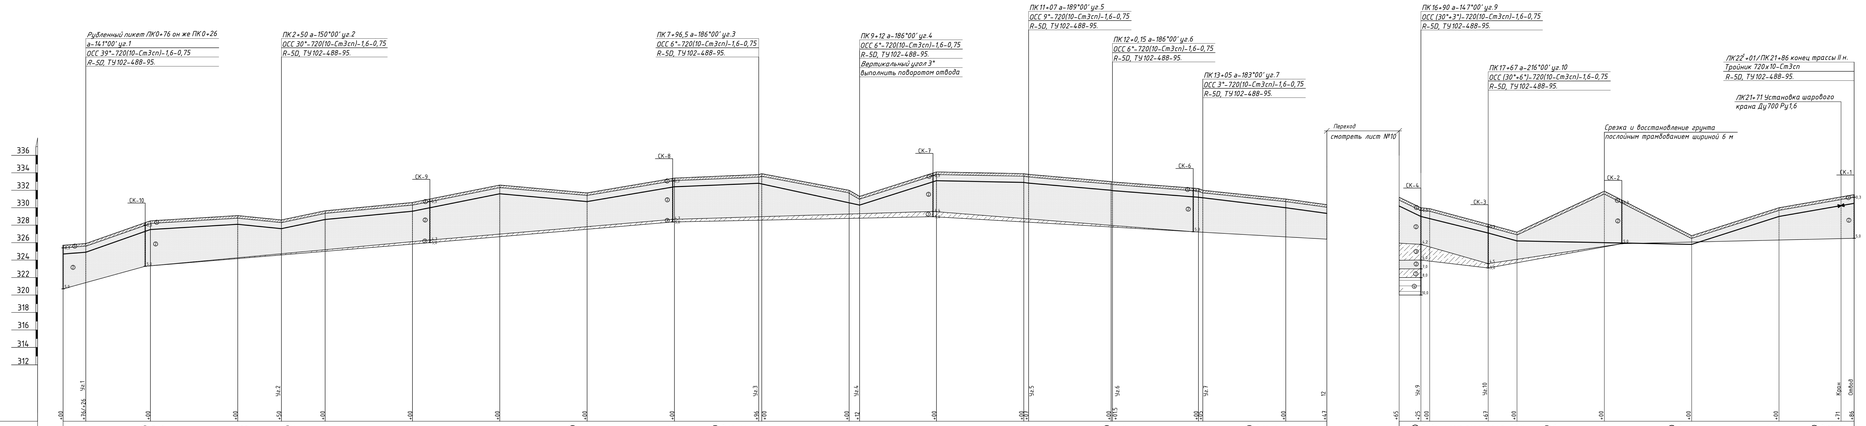



| | | | | | | | |
|---|---|---|---|---|---|---|---|
| | | | | | | 029-26-ГСН | |
| | | | | | | Магистральный газопровод-отвод со строительством новой ГРС подключения к МГ-отводу "Горный" для газоснабжения новостроящихся горнорудных электростанций мощностью 1500-1600 МВт в Сдержданьской области | |
| Изм. | Кол.уч. | Лист | №док. | Подп. | Дата | | |
| Нач. отд. | | | | | | Газопровод высокого давления | Стадия: РП; Лист: 9; Листов: |
| Исполн. | | | | | | Продольный профиль трассы магистрального газопровода от ПК40+00 по ПК61+00 | ЦЕНТРАЛЬГАЗ «TRANSGAZELIVRENG» RCS() |
| Норк. контр. | | | | | | | |