


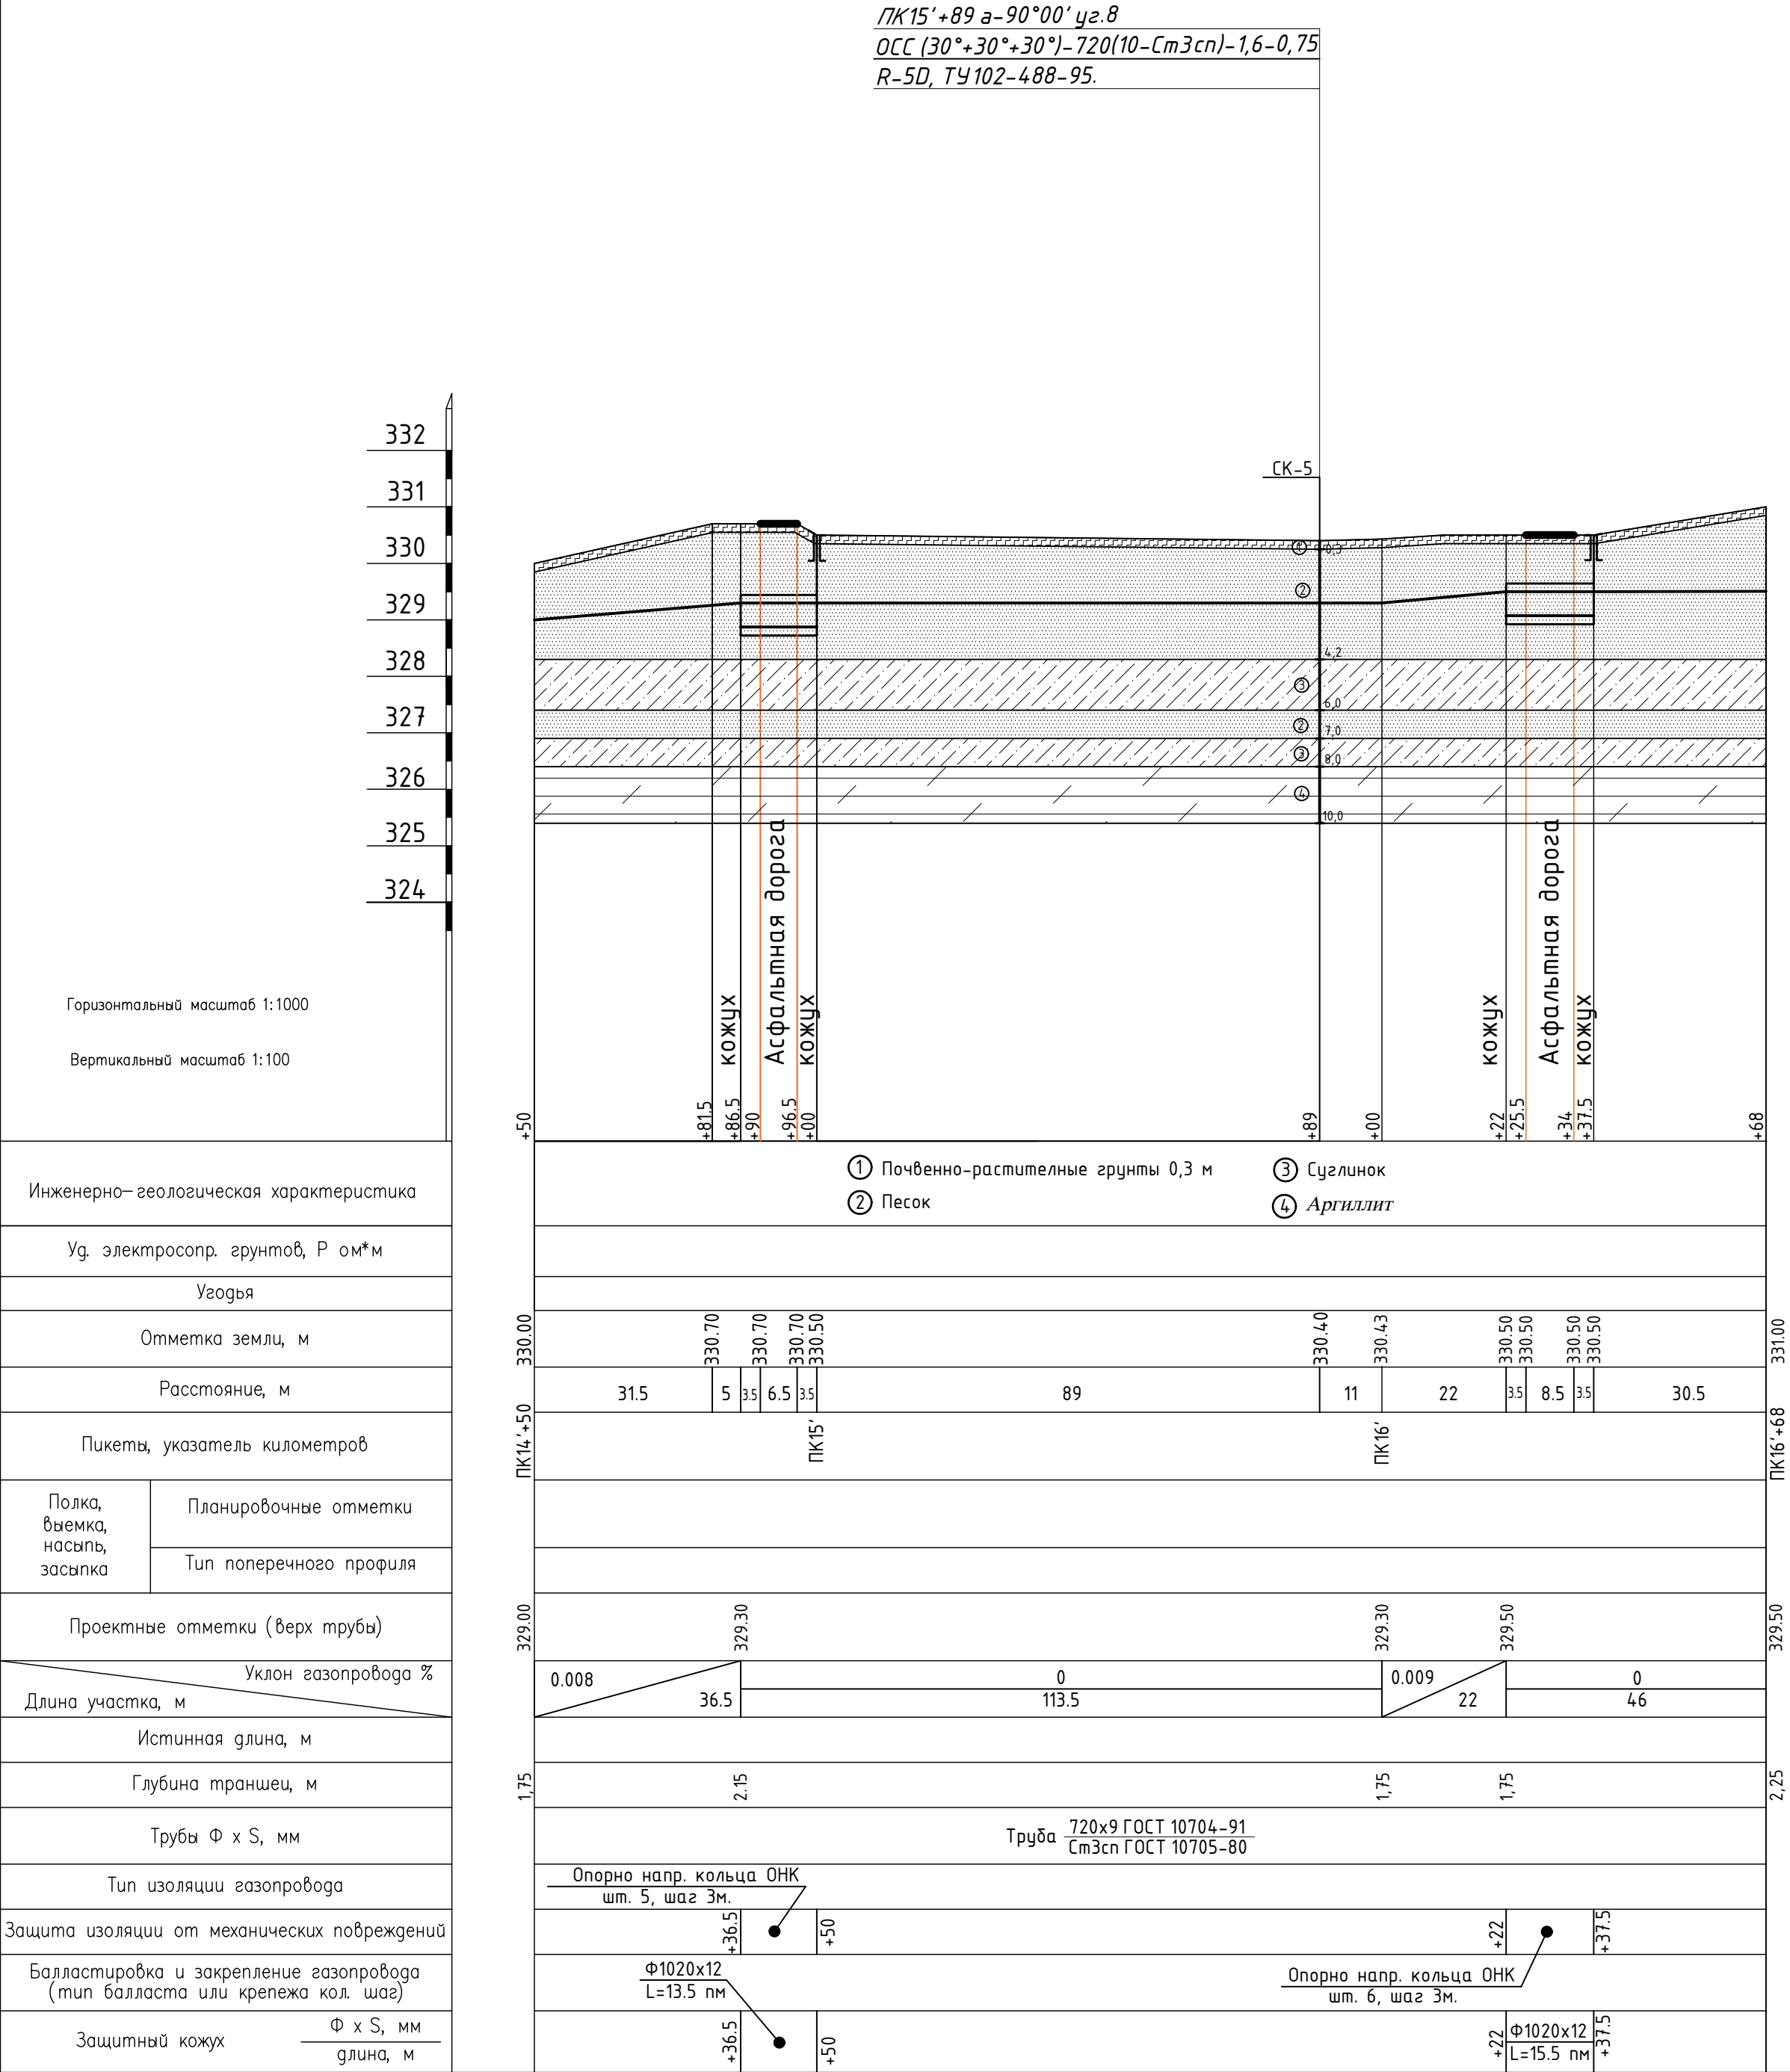

						029-26-ГСН			
						Магистральный газопровод -отвод со строительством новой ГРС подключением к МГ -отводу "Термиз" для газоснабжения новостроящейся парогазовой электростанции мощностью 1500-1600 МВт в Сурхандарьинской области			
Изм.	Колуч.	Лист	Идок.	Подп.	Дата	Газопровод высокого давления	Стадия	Лист	Листов
Нач. отд.							РП	3	3
Исполн.						Продольный профиль подземной части газопровода высокого давления от ПК0+00 по ПК2+69,5	 UZTRANS-GAZ «TRANSGAZINJINIRING» MCHJ		