

Ведомость рабочих чертежей основного комплекта

Лист	Наименование	Примечание
1	Общие данные.	
2	План расположения оборудования системы охранного видеонаблюдения. 1:100.	
3	Структурная схема системы охранного видеонаблюдения.	
4	Принципиальная схема телекоммуникационного шкафа	
5	Установочный чертеж стойки для камеры.	

телекоммуникационного шкафа

Ведомость ссылочных и прилагаемых документов

Обозначение	Наименование	Примечание
	Прилагаемые документы	
000-26- ГРС -ВН.С	Спецификация оборудования, изделий и материалов	
000-26- ГРС -ВН.ВР	Ведомость объемов работ	

ОБЩИЕ УКАЗАНИЯ

Рабочие чертежи разработаны в соответствии с действующими нормами, правилами и стандартами.

Данным проектом предусматривается организация системы периметрального видеонаблюдения проектируемого объекта.

Для унификации проектируемого оборудования проектом предусматривается установка видеокамер с вариофокальным объективом с фокусным расстоянием 2,8-12 мм. Угол обзора данной видеокамеры составляет от 35° до 106°. Питание видеокамер осуществляется по технологии PoE. Камеры работают в расширенном диапазоне температур от -40 до +60°С и имеют степень влагозащищенности IP 67. Видеокамера оснащена инфракрасной подсветкой до 30 м. Камеры установить на опора со светильником на отметке 3,0м от уровня земли.

На участке от всепогодного шкафа до настенного шкафа предусматривается прокладка четырехволоконного оптического кабеля ОКЦБ-П-4Е-(1х4)-7кН. На площадке ГРС от влагозащищенного шкафа до видеокамер предусматривается кабель UTP-4х2х0,52, категория 5е.

Для отображения и записи видеоизображений проектом предусматривается установка видеорегистратора на 14 канала. Объем жестких дисков рассчитан на время записи не менее 30 дней.

Для отображения видеоизображений проектом предусматривается установка 43" LED телевизора в доме операторов. Сетевой видеорегистратор установить 4G модем типа Mikrotik LtAP mini LTE Kit с антенной, блоком питания и каналом 4G/LTE на рабочем месте оператора.

Для сбора данных с видеокамер и питания по технологии PoE предусматривается установка коммутаторов. Коммутаторы поддерживают подключение видеокамер на расстояние до 461м.

Для бесперебойного электропитания системы видеонаблюдения проектом предусматривается установка источника бесперебойного питания с дополнительной аккумуляторной батареей.

Для размещения видеорегистратора, коммутационного оборудования и ИБП с аккумуляторной батареей проектом предусматривается установка телекоммуникационного шкафа в помещении операторной и на ГРС всепогодный шкаф.

Все оборудование должно быть надежно заземлено. Заземление телекоммуникационного шкафа предусматривается от электротехнического защитного заземления.

От всепогодного шкафа на площадке ГРС до телекоммуникационного шкафа в доме операторов ВОР проложить в траншее на глубине 0,8 м.

Все электромонтажные работы вести в соответствии с ПУЭ-2013г.

Взам. инв. №


Подп. и дата

Инв. № подл.


						000-26 -ГРС -0- ВН.			
						"Surxondaryo viloyatidagi quvvati 1500–1600 MVt bo'lgan bug'-gaz elektr stansiyasini tabiiy gaz bilan ta'minlash"			
Изм.	Кол.уч.	Лист	№ док	Подп.	Дата	Система охранного видеонаблюдения	Стадия	Лист	Листов
Нач. отд.		Бабаев					РП	1	5
						Общие данные			
Исполн		Ахмедов							

Формат А4х3

Коммуникационный шкаф 8U(XB-01)

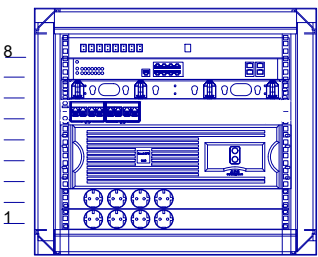


Шкаф настенный 400х600х530 IP 40, DIN

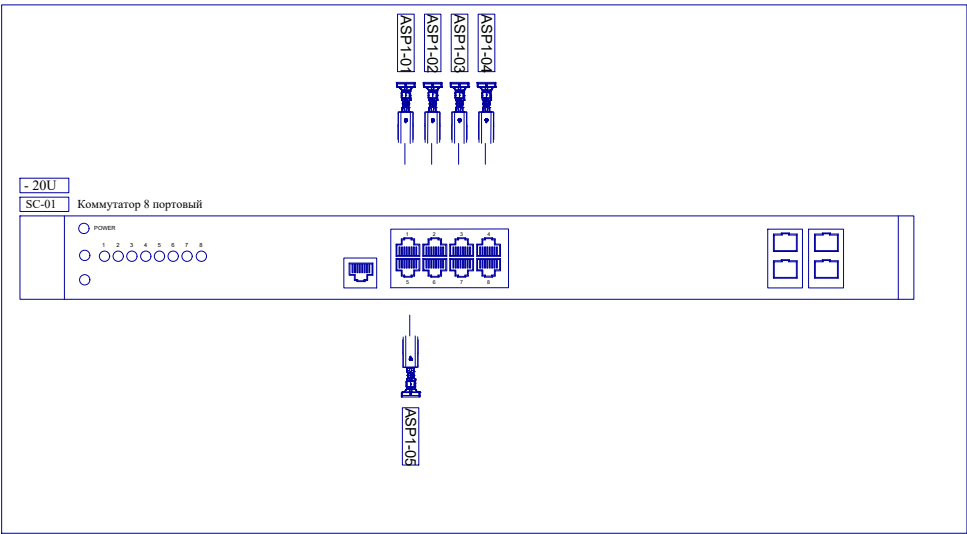

Наименование материала в серверном шкафу./
The name of the material in the server cabinet.

№	Наименование	Кол-во/
Шкаф-ХВ-01/ Cabinet-ХВ-01		
8	Оптический патч панель	Fiber Optic Panel 1
7	Коммутатор 8 порт	Network switch (Net) 1
6	Сетевой коммутатор (ВН)	Network switch (Net) 2
4	Патч-панель 8 Port.	Patch Panel 8 Port. 2
5	Кабельный организер	Cable organizer 2
1,2	Панель распределительная 8 гнезд (пилот)	Distribution panel 8 sockets (pilot) 2
3	UPS	UPS 1

Инв. № подл.	Изм.	Кол.уч	Лист	№ док	Подп	Дата	000-26 - ГРС - ВН.С		
Инв. № подл.	Исполн	Ахмедов					Система охранного видеонаблюдения		
							Стадия	Лист	Листов
							РП	4	5
							Принципиальная схема телекоммуникационного шкафа		
							 UZTRANS GAZ «TRANSGAZINJINIRING» MCHJ		

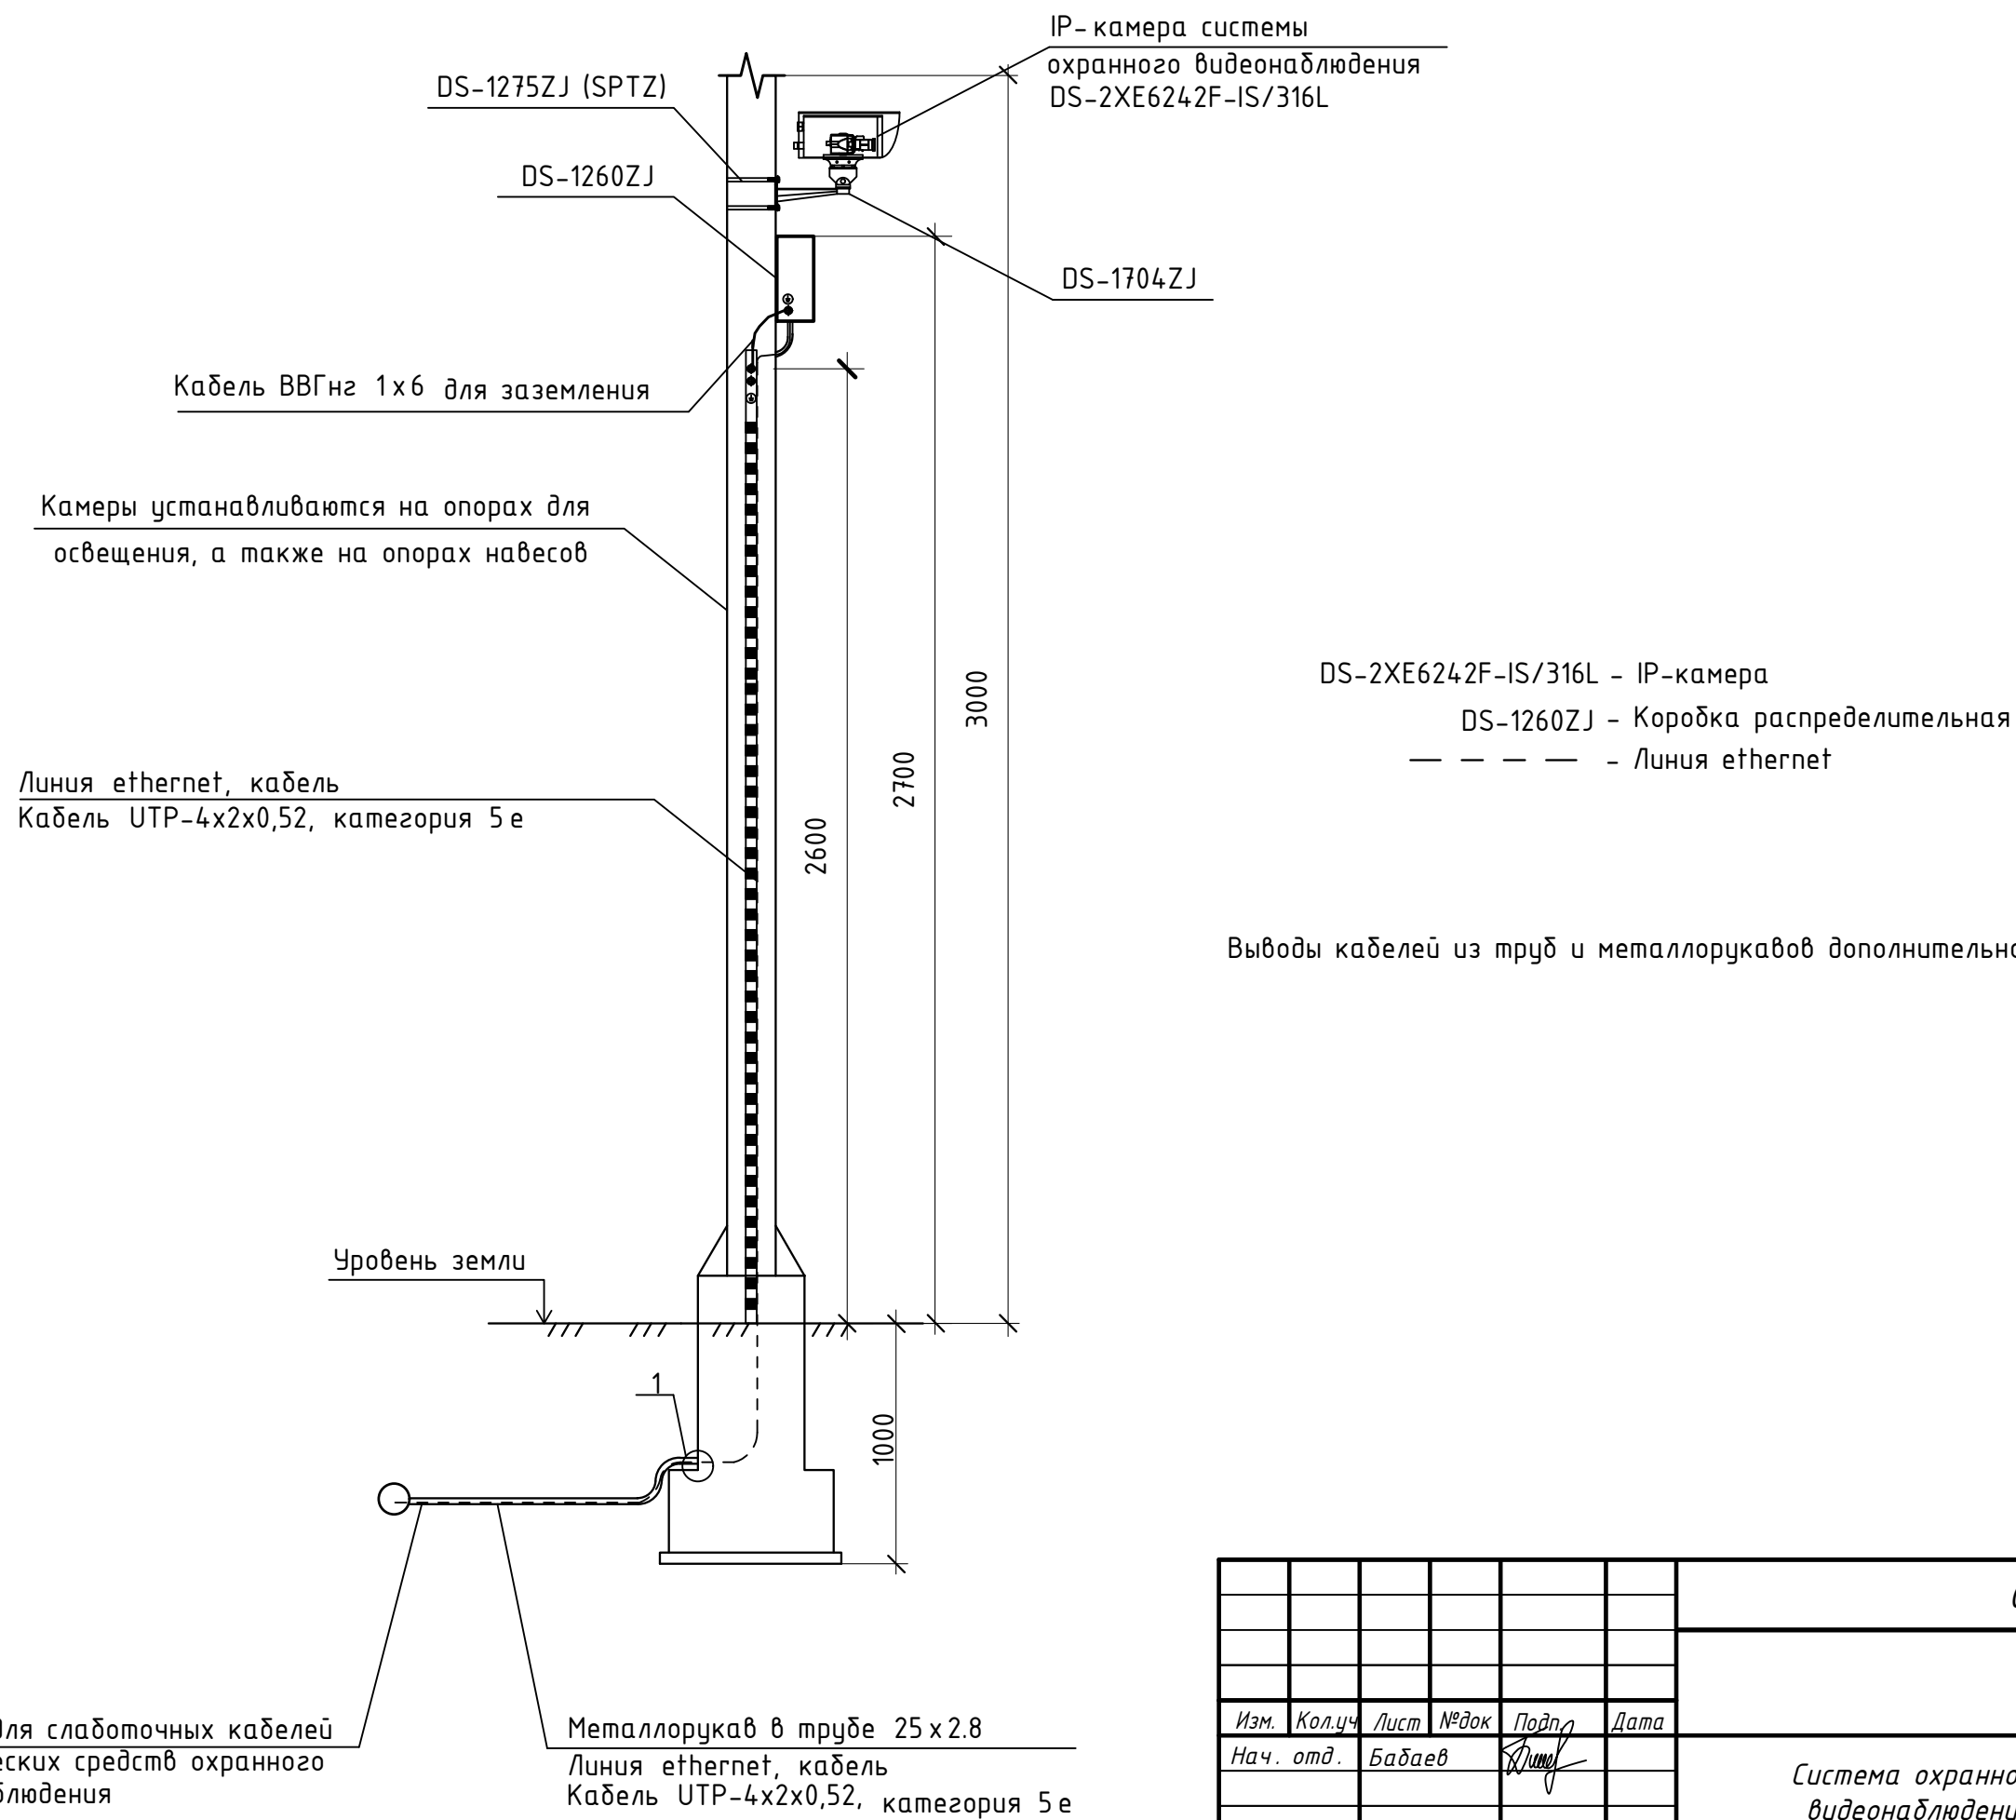

Инв. № подл.	Подп. и дата	Взам. инв. №

						000-26- ГРС -ВН			
Изм.	Кол.уч	Лист	№ док	Подп.	Дата	Система охранного видеонаблюдения	Стадия	Лист	Листов
Нач. отд.		Бабаев					РП	5	5
						Установочный чертеж стойки для камеры	 UZTRANSGAZ «TRANSGAZINJINIRING» MCHJ		
Исполн		Ахмедов							

Инв. N подл.	Подпись и дата	Взам. инв. N

Пози- ция	Наименование и техническая характеристика	Тип,марка, обозначе- ние документа опросного листа	Код обо- рудования, изделия, материала	Завод - изготовитель	Единица измере- ния	Коли- чество	Масса единицы, кг	Приме- чание
	Участок трассы ВОЛС от ГРС до Дома операторов							
1	Четырехволоконный оптический кабель	ОКЦБ-П-4Е-(1х4)-7кН		ООО "Kabel Tech Fiber"	м	5		
2	Защитно-сигнальная лента			ЗАО "СВЯЗЬСТРОЙДЕТАЛЬ"	км	-		
3	Труба БНТ 100-2950	ГОСТ 31416-2009			шт	8		
4	Столбик замерный железобетонный	ТР-К-СС 2.8			шт	-		
5	Металлорукав Ø25 мм с прокладкой кабелем изнутри	РЗ-ЦХ			м	167		
6	Труба 108х6	ГОСТ 3262-85			м	-		
7	Коммутатор на 8 порта	DS-3E1309P-EI		Hikvision	шт	2		
8	Оптическая одномодовый пигтейл SC, 1м				шт	8		
9	Оптическая патч панель 4хSC, SM, DIN 35 mm				комплект	2		
10	Оптическая патч-корд SC\SC, SM, duplex, 1 м				шт	2		
11	Кабель UTP-4х2х0,52, категория 5е				м	461		
12	Коннектор RJ-45				шт	25		
13	Патч-корд RJ-45, UTP категории 5 е, 1 м				шт	2		
14	Сетевой видеорегистратор 16 канала	DS-7716NI-I4		Hikvision	шт	1		
15	HDD SATA 1 ТБ				шт	1		
16	Блок бесперебойного питания	СКАТ-2400P20-24V/3.5A			шт	1		
17	4Мп уличная цилиндрическая IP-камера с ИК-подсветкой до 30м	DS-2XE6242F-IS/316L		Hikvision	шт	5		
18	Монтажная коробка	DS-1280ZJ-S		Hikvision	шт	5		

						000-26- ГРС -ВН.СО			
Изм.	Кол.уч	Лист	№док	Подп	Дата	Система охранного видеонаблюдения	Стадия	Лист	Листов
Нач. отд.	Бабаев						РП	1	3
						Спецификация оборудования, изделий и материалов	 UZTRANSGAZ «TRANSGAZINJINIRING» MCHJ		
Исполн	Ахмедов								

Инва. N подл.

Подпись и дата

Взам. инв. N

Пози- ция	Наименование и техническая характеристика	Тип,марка, обозначе- ние документа опросного листа	Код обо- рудования, изделия, материала	Завод - изготовитель	Единица измере- ния	Коли- чество	Масса единицы, кг	Приме- чание
19	Крепления камеры	DS-1704ZJ		Hikvision	шт	5		
20	Кронштейн для крепления камеры на столб	DS-1275ZJ(SPTZ)		Hikvision	шт	5		
21	Телевизор 43", SMART в комплекте с кронштейном				шт	1		
22	Кабель HDMI				м	30		
23	Шкаф всепогодный уличный настенный 400х600х530 IP 67, DIN				шт	1		
24	Шкаф настенный 400х600х530 IP 40, DIN				шт	1		
25	USB мышь				шт	1		
26	Монокристаллическая солнечная панель 550 Вт	"Einnova Solarline ESM-550S"			шт	1		
27	4G модем на базе Router OS с внешней антенной	Mikrotik LtAP mini LTE Kit			шт	1		
28	SIM карта сотовой связи				шт	1		
29	Электропитание удлинитель 10м				шт	1		
30	Гелевый аккумулятор 100 А	Axioma Energy AX-Gel-100 12V			шт	1		см. примечание на данном листе
31	Инвертор 12/220 В 800 Вт	Invertor Growatt MID 1000			шт	1		

Примечание :
Гелевые аккумуляторные блоки имеют глубина разряда 50%

№ п/п	Наименование работ	Ед. изм.	Кол.	Примечание
	<u>Земляные работы</u>			
1	Рытье траншеи и обратная засыпка в грунтах II группы	м ³	167	
2	Установка замерных столбиков	шт	-	
3	Гидроизоляция замерных столбиков	м ²	-	
4	Отсыпка щебнем для замерных столбиков	м ³	-	
	<u>Работы по прокладке оптического кабеля</u>			
1	Ввод кабеля ВОК в стальной трубе Ø57х3,5 в помещение операторной	ввод	1	
2	Ввод кабеля ВОК в стальной трубе Ø57х3,5 в подвесн. шкаф	ввод	1	
3	Прокладка кабеля в операторной о стене	м	3	
4	Укладка кабеля в уличном подвесном шкафу	м	2	
5	Измерение волоконно-оптического кабеля на кабельной площадке с числом волокон 4	кабель	1	
6	Измерение затухания на смонтированном участке в одном направлении с числом волокон 4	у-к	1	
	труба Ø57х3,5 (гилза)	м	1	

[illegible]

000-26 - ГРС - ВН.ВР

[illegible]

000-26 - ГРС - ВН.ВР