

Ведомость рабочих чертежей основного комплекта

Лист	Наименование	Примечание
1	Общие данные.	
2	План трассы водопровода к ГРС. М 1:500.	
3	План систем В1; Т1 на отм. 0,000.	
	Схемы сетей В1; Т1.	
4	План системы К1. Схемы сети К1.	
5	Сечения каналов	

Ведомость ссылочных и прилагаемых документов

Обозначение	Наименование	Примечание
	<u>Прилагаемые документы</u>	
000-26 -ГРС -ВК. СО	Спецификация оборудования, изделий и материалов	

Условия строительства

Сейсмичность района – 8 баллов.
Категория грунтов по разработке согласно ШНК 4.02.01-04:
см. табл.1-1а – первый абзац п.5
см. табл.1-1в – первый абзац п.7
Глубина промерзания грунта – 0,70 м.
Тип просадочности грунта – не просадочный.

Общие указания

Данный проект выполнен на основании задания от технолога.
Рабочие чертежи разработаны в соответствии с действующими нормами, правилами и стандартами Республики Узбекистан.

За относительную отм. 0,000 принята отметка чистого пола.

В здании запроектированы:

- В1- хозяйственно-питьевое водоснабжение;
- Т1- горячее водоснабжение (подающий трубопровод);
- К1- бытовая канализация;

Сети системы В1 принимаются из полипропиленовых труб диаметрами 20х1,9

Система Т1 запроектирована из полипропиленовых труб диаметрами 20х1,9

Трубопроводы системы К1 запроектированы из полиэтиленовых канализационных труб диаметрами 50 по ГОСТ 22689.2 –89.


Монтаж трубопроводов производить в соответствии с КМК 3.05.01-97

“Внутренние санитарно – технические системы”.

Примечание – провести гидроиспытание и промывку в сетях В1; Т3; К1, а также дезинфекцию трубопроводов В1; Т1.

Инв. № подл.	Подп. и дата	Взам. инв. №


						000-26 -ГРС -ВК						
Изм.	Кол.уч	Лист	№Док	Подп.	Дата	Операторная			Стадия	Лист	Листов	
Нач. отд.		Бабаев							РП	1	5	
Исполн.		Ахмедов				Общие данные			 UZTRANS-GAZ «TRANS-GAZINJINIRING» MCHJ			

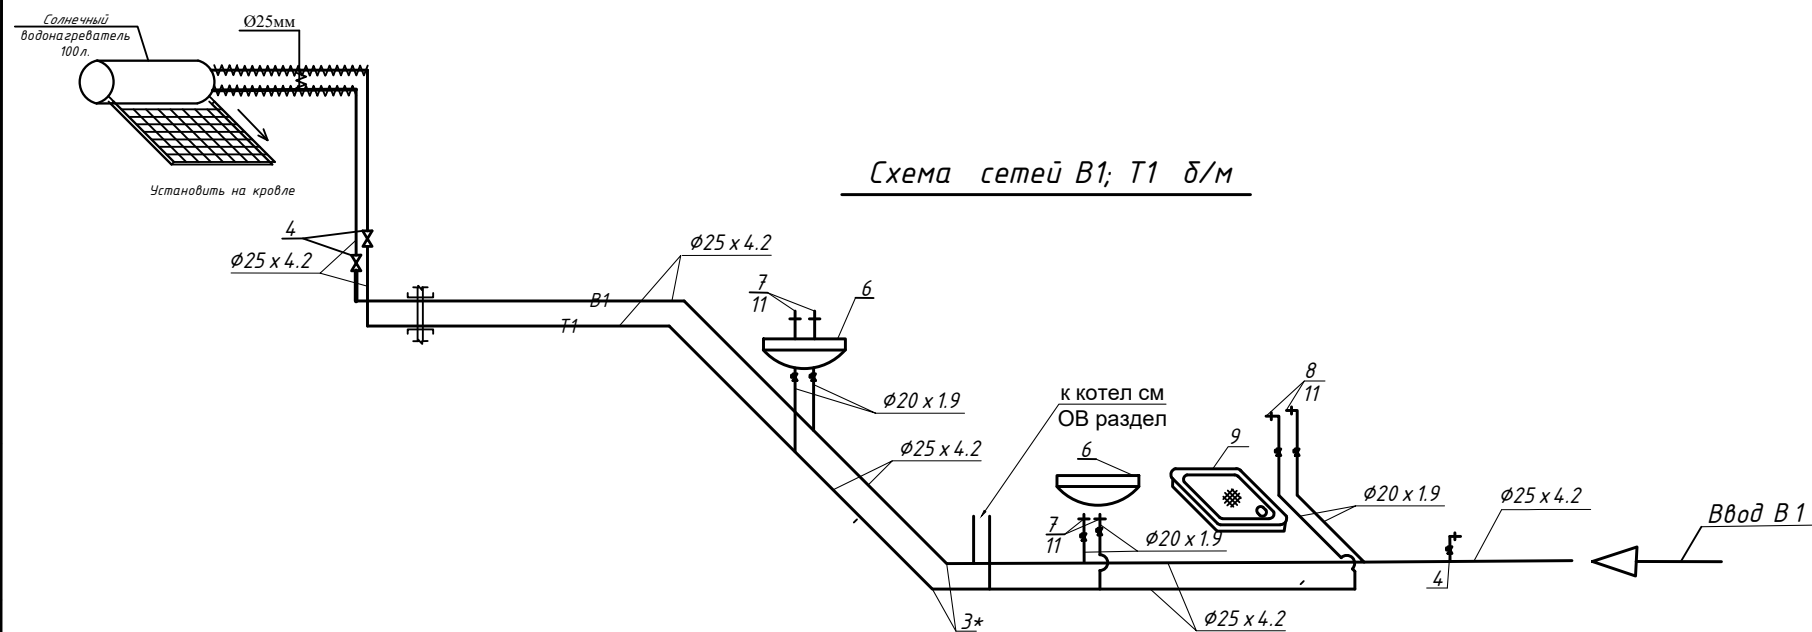


Ведомость потребности материалов на водоснабжение

Поз.	Обозначение	Наименование	Ед изм.	кол- во
1	ГОСТ 18599-2001	Труба полипропиленовая PN 1,0		
		диаметром 25х4,2 питьевая	м	50
2	ТУ 2248-004-88742502-2002	Отвод 90° P0401 Ф20	шт	18
2*	ТУ 2248-004-88742502-2002	Отвод 90° P0401 Ф25	шт	12
3	ТУ 2248-004-88742502-2002	Тройник P0801 Ф25х20х25	шт	5
3*	ТУ 2248-004-88742502-2002	Тройник P0801 Ф25х25х25	шт	2
4		Вентиль полипропиленовый P4601 DN 25	шт	4
4*		Вентиль полипропиленовый P4601 DN 20	шт	6
5	ГОСТ 8732-2001	Труба гильза Ф63х3.8мм (L=400мм)	шт	1
6	ГОСТ 23695-2016	Мойка МСН с сифоном в комплекте	шт	3.0
7	ГОСТ 25809-96	Смеситель для умывальника СМ - УМОЦБА	шт	3.0
8	ГОСТ 25809-96	Смеситель для душа	шт	1,0
9		Поддон для душа с сифоном в комплекте	шт	1.0
10		Носос водяной ЕРА EVN-A200-3 в	шт	1.0
11	ГОСТ 18599-2001	Труба полипропиленовая PN 1,0		
		диаметром 20х1,9 для горячей воды	м	13

						000-26 - ГРС -0- ВК.		
Изм.	Кол.	Лист	№ док.	Подпись	Дата			
Нач. отд.		Бабаев				Холодное и горячее водоснабжение операторной	Стадия	Лист
							РП	3
Исполн.		Ахмедов				План систем В1; Т1 на отм. 0,000. Схема сетей В1, Т1.	 UZTRANSGAZ «TRANSGAZINJINIRING» MCJ	

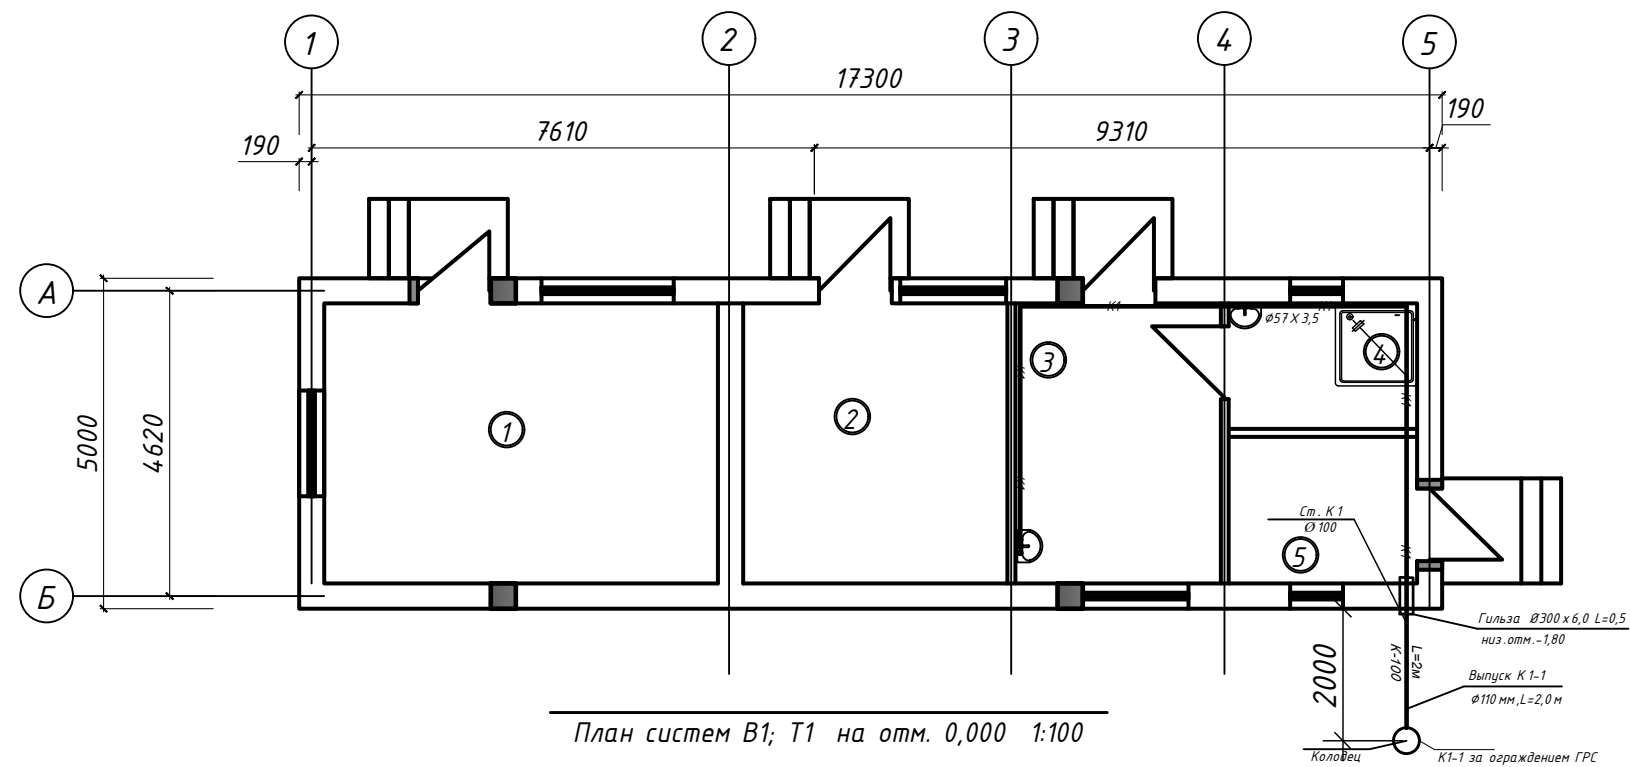

План систем В1; Т1 на отм. 0,000 1:100

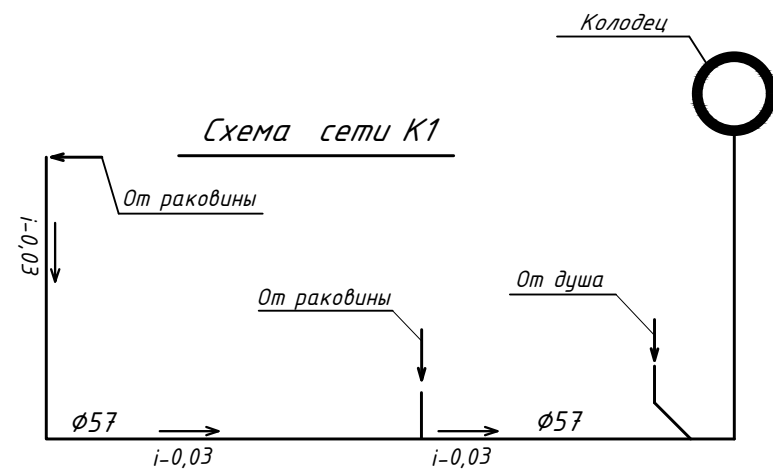

Экспликация помещений

Номер помещения	Наименование	Площадь м²
1	Рабочий кабинет	25.27
2	Комната отдыха	16.96
3	Кухня	13.2
4	Душевая	5.41
5	Эл. щитовая	5.98
		7.52

Ведомость потребности материалов на канализацию

Поз.	Обозначение	Наименование	Ед изм.	Количество
1	ГОСТ 22689.2	Труба ТК 100-6000-ПНД	м	5,0
2	ГОСТ 22689.2	Труба ТК 50-6000-ПНД	м	14,0
3	ГОСТ 22689.2	Отвод О 90° 100К х 100к-ПНД	шт	2,0
4	ГОСТ 22689.2	Отвод О 90° 50К х 50к-ПНД	шт	3,0
5	ГОСТ 22689.2	Тройник Т 50К х 50к х 50К-ПНД	шт	2,0
6	ГОСТ 22689.2	Заглушка З 50-ПНД	шт	1,0
7	ГОСТ 22689.2	Переход D110 х 50-ПНД	шт	1,0
8		Канализационный колодец Ø700 мм	шт	1,0


000-26 -ГРС -0- ВК.

Изм.	Кол.	Лист	№ док.	Подпись	Дата			
Нач. отд.		Бабаев				Холодное и горячее водоснабжение операторной	Стадия	Лист
							РП	4
Исполн.		Ахмедов				План систем В1; Т1 на отм. 0,000. Схема сетей В1, Т1.		

Сечения каналов

СПЕЦИФИКАЦИЯ ЭЛЕМЕНТОВ

Инв. № подл.	Подп. и дата	Взам. инв. №

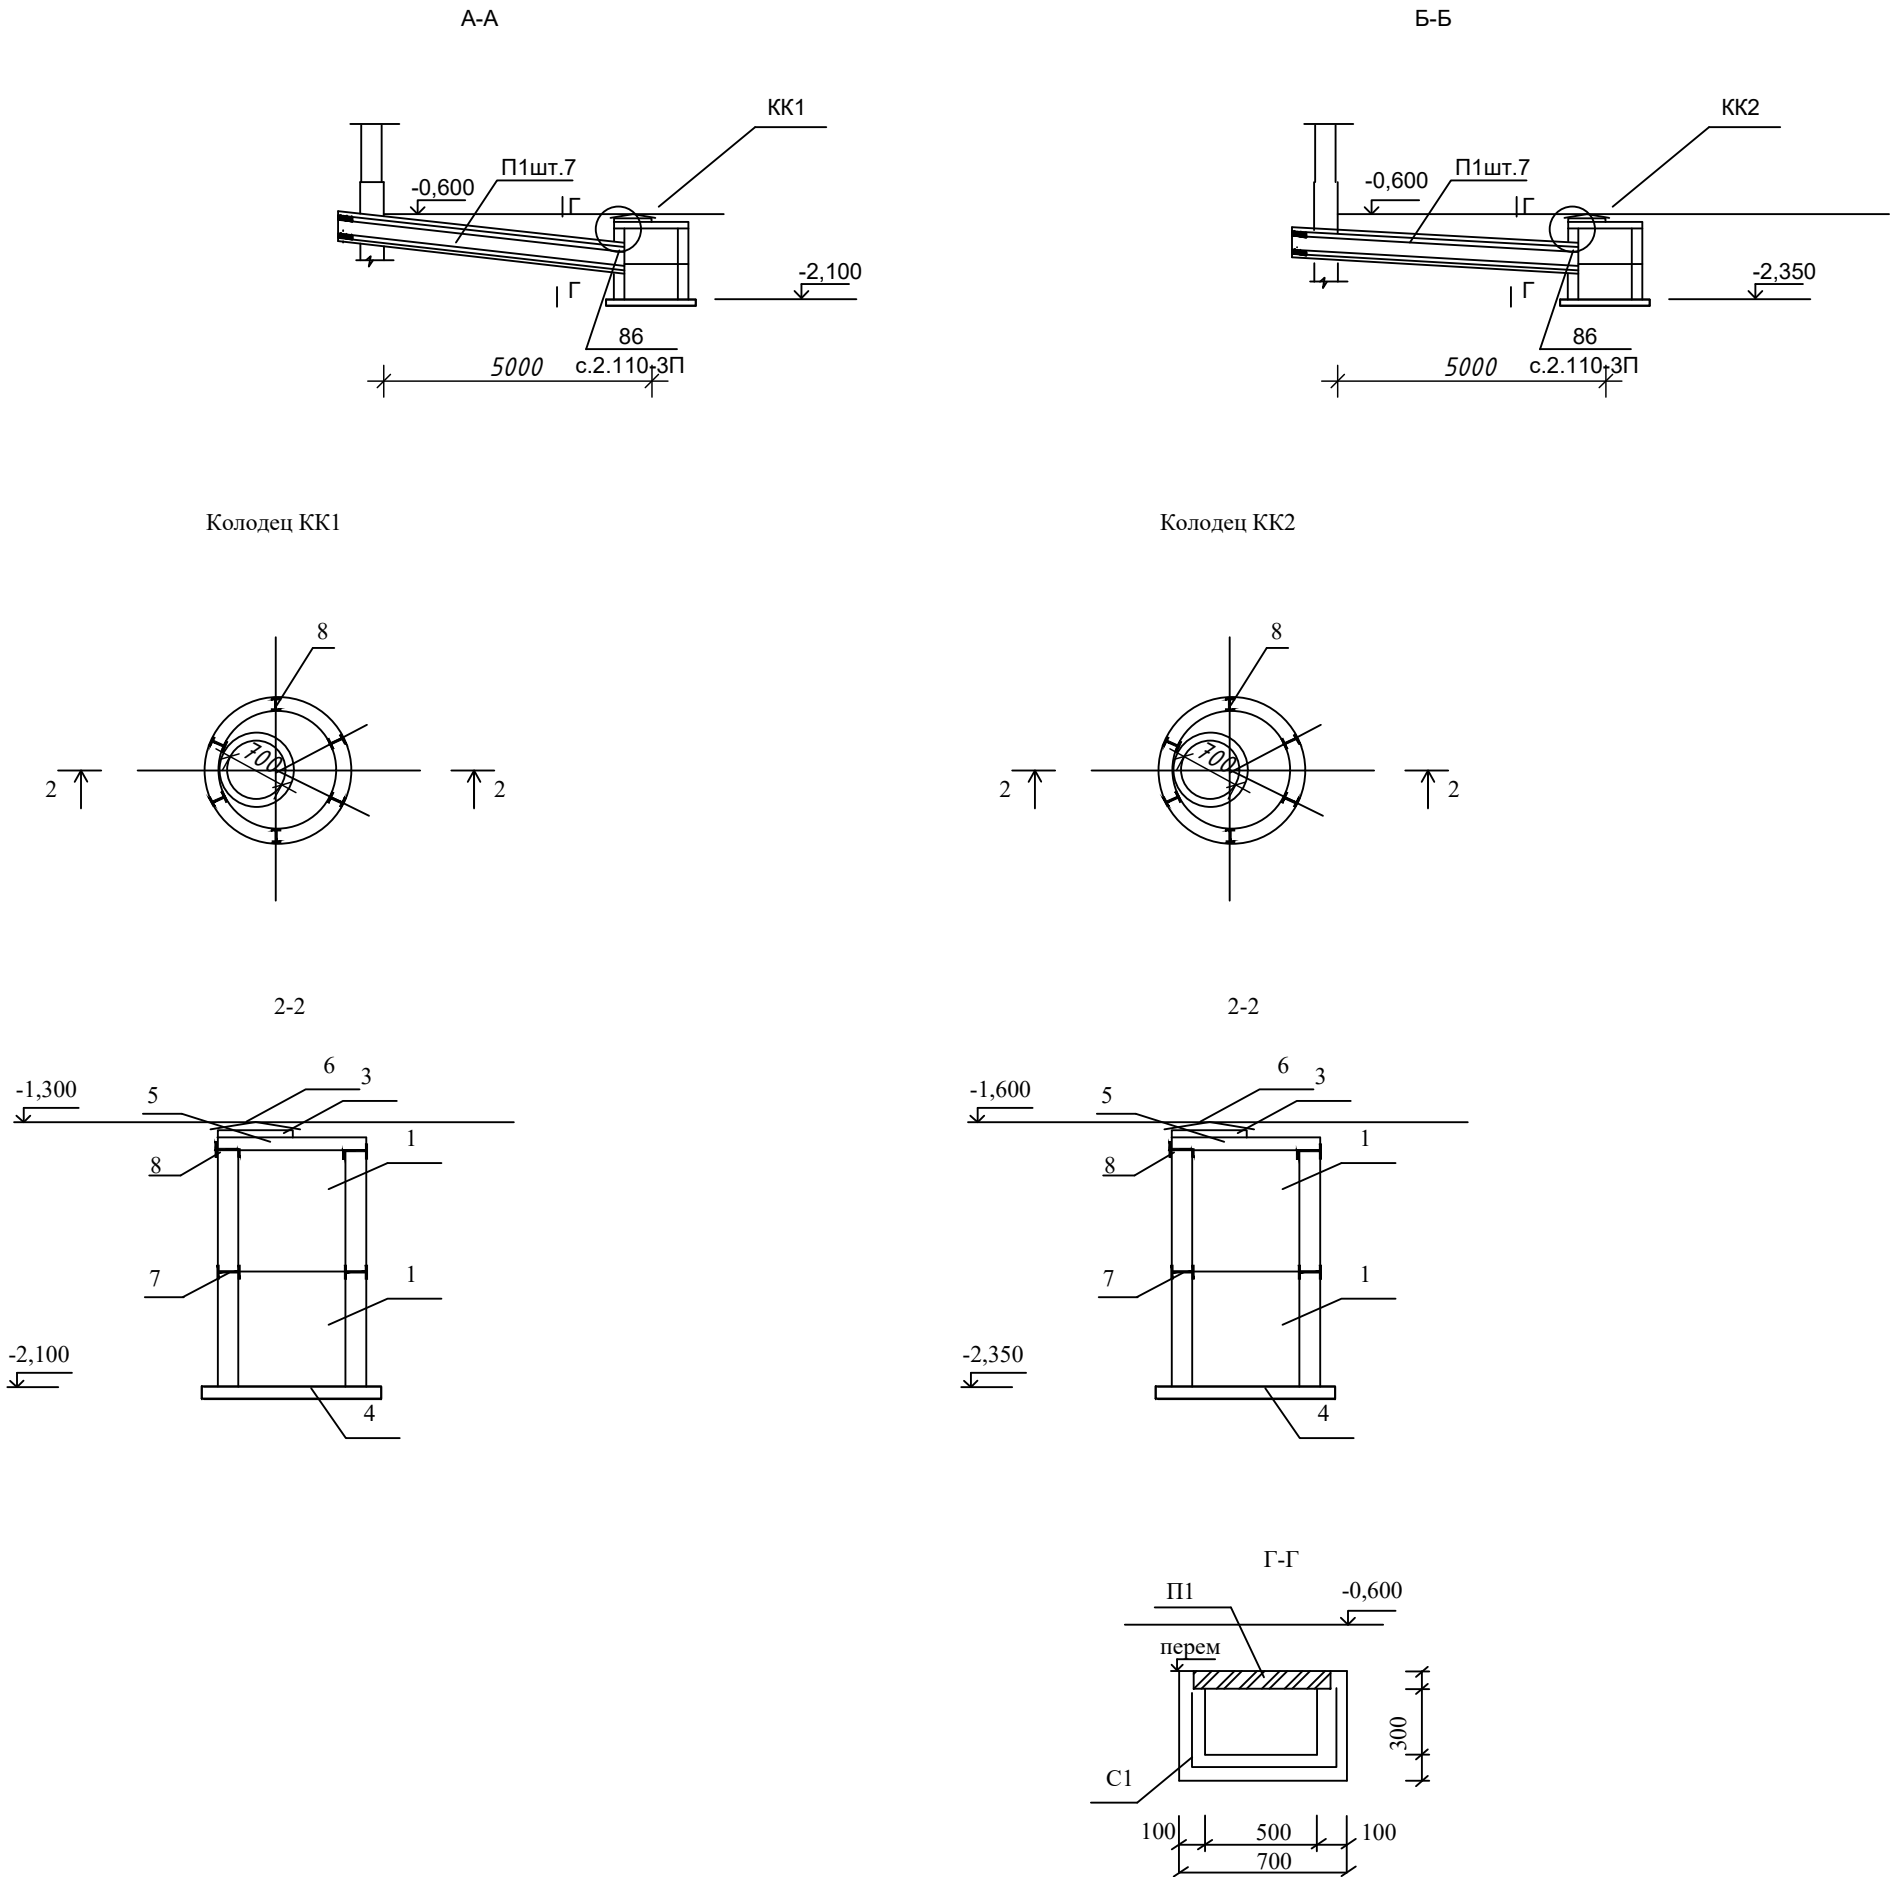

Поз.	Обозначение	Наименование	Кол.		Масса ед.кг	Примеч.
			КК1			
			5			
1	3.900.1-14	Кольцо стеновое КС10-7	2		260кг	
3	"	Кольцо опорное КО6	1		50кг	
4	"	Плита днища ПН10	1		0,45т	
5		Плита перекрыт. 1ПП10-2	1		0,25т	
6	ГОСТ 3634-89	Люк чугунный Ø700	1		79кг	
7	т.п. 902-09-84	соед. э-т МС3	12		2,01кг	
8	"	" МС7	6		1,83кг	

Примечание:

Под каналами предусмотреть бетонную подготовку - 2,5 м3 В12,5

						000-26 - ГРС - 0 - ВК.			
Изм.		Лист	№ Док	Прод	Дата	Холодное и горячее водоснабжение и канализация	Стадия	Лист	Листов
Нач. отд.	Бабаев						Р.П	5	
						Сечения каналов			
Исполн.	Ахмедов								

		Поз.	Наименование и техническая характеристика	Тип, марка, обозначение документа, опросного листа	Код продукции материала	Поставщик	Ед. измерения	Кол.	Масса 1 ед., кг	Примечание	
		1	2	3	4	5	6	7	8	9	
Взам. инв. №	Подп. и дата		Наружный водопровод								
		1	Труба полиэтиленовых труб PN 1,0 Ø25x4,2 питьевая				м	33			
		2	Труба полиэтиленовых труб PN 1,0 Ø20x1,9 питьевая				м	3			
		3	Вентиль полипропиленовый P4601 DN 25				шт	5			
		3	Вентиль полипропиленовый P4601 DN 20				шт	2			
		4	Отвод 90° P0401 Ø25				шт	5			
		5	Труба ППР Ø50x6,9 мм				п.м.	32			
			Холодное и горячее водоснабжение								
			1	Труба полипропиленовая PN 1,0							
				диаметром 25x4,2питьевая				м	50		
Инв. № подл.		2	Отвод 90° P0401 Ø25				шт	12			
		3	Тройник P0801 Ø25x25x25				шт	2			
		4	Тройник P0801 Ø25x20x25				шт	5			
		5	Вентиль полипропиленовый P4601 DN 20				шт	6			
		6	Вентиль полипропиленовый P4601 DN 25				шт	4			
		7	Труба гильза Ø63x3.8мм (L=400мм)				шт	1			
		8	Мойка МСН с сифоном в комплекте				шт	3.0			
		9	Смеситель для умывальника См - УМОЦБА				шт	3.0			
		10	Смеситель для душа				шт	1,0			
		11	Поддон для душа с сифоном в комплекте				шт	1.0			
		12	Носос водяной ЕРА EVN-A200-3 в				шт	1.0			
								000-26 -ГРС -0- ВК.СО			

Инв. N подл.	Изм. N подл.	Подп. и дата	Взам. инв. N										
Исполн.	Ахмедов	Джам	Бабаев	Лист	№ Док	Подп.	Дата	000-26 - ГРС - 0 - ВК .ВР					
Водоснабжение , теплоснабжение и канализация операторной								Стадия	Лист	Листов			
								РП	1	2			
Ведомость объемов сан. технических работ								 UZTRANS-GAZ «TRANS-GAZINJINIRING» MCHJ					

