

Общие указания

Настоящий проект выполнен на основании задания на проектирование от ГИПа и смежных отделов.

Рабочие чертежи разработаны в соответствии с действующими нормами, правилами и стандартами.

Настоящим проектом решается электроосвещение навеса

Электроосвещение.

Проектом предусмотрено общее рабочее освещение.

Напряжение у ламп рабочего освещения-220 V.

Установленная мощность рабочего освещения составляет 0,36кW.

Расчёт освещения произведён методом удельной мощности W/m^2 .

Величины освещенности выбраны в соответствии с КМК2.01.05-98.

Групповые сети освещения выполняются кабелем марки ВВГнг.

Управление освещением осуществляется автоматическими выключателями со щитка освещения в операторной.

Оружующая среда взрывоопасная категории ВІ-Г.

Защитные мероприятия.

Все металлические нетоковедущие части электрооборудования, нормально не находящиеся под напряжением заземлить, используя нулевые жилы кабелей питающих и распределительных сетей, специально проложенную от ближайшей ответвительной коробки третью жилу кабеля.

Все монтажные работы выполнить в соответствии с требованиями ПУЭ, КМК 3.05.06-97, ВСН-332-74.

Инв.№.N										
Подп. и дата							000-26 -ГРС -3- ЭМО			
	Изм.	Кол.	Лист	№Док.	Подпись	Дата				
Инв.№ подл.	Нач. отд.	Бабаев				ГРС. Навес (12,0x15,0м)		Стадия	Лист	Листов
								РП	1.1	2
	Исполн.	Ахмедов				Общие данные.		 UZTRANS-GAZ «TRANS-GAZINJINIRING» MCHJ		

ВЕДОМОСТЬ РАБОЧИХ ЧЕРТЕЖЕЙ ОСНОВНОГО КОМПЛЕКТА

Лист	Наименование	Примечание
1	Общие данные	2 листа
2	Расположение электрического оборудования и прокладки электрических сетей.	
	План на отм. 0,000. 1:100. Электроосвещение	


ВЕДОМОСТЬ ССЫЛОЧНЫХ И ПРИЛАГАЕМЫХ ДОКУМЕНТОВ

Обозначение	Наименование	Примечание
	<u>Прилагаемые документы</u>	
000-26 -ГРС -З- ЭМО.С	Спецификация оборудования	
000-26 -ГРС -З- ЭМО.ВР	Ведомость объемов работ	

Инв. N подл.	Подп. и дата	Взам. инв. N							
							000-26 - ГРС - 3- ЭМО		Лист
Изм.	Кол.	Лист	N док	Подп.	Дата				1.2

И.нв. N подл.	
Подпись и дата	
Взам.инв N	

Навес . 12,0х15,0м. Электроосвещение. План на отм. 0,000. 1:100.

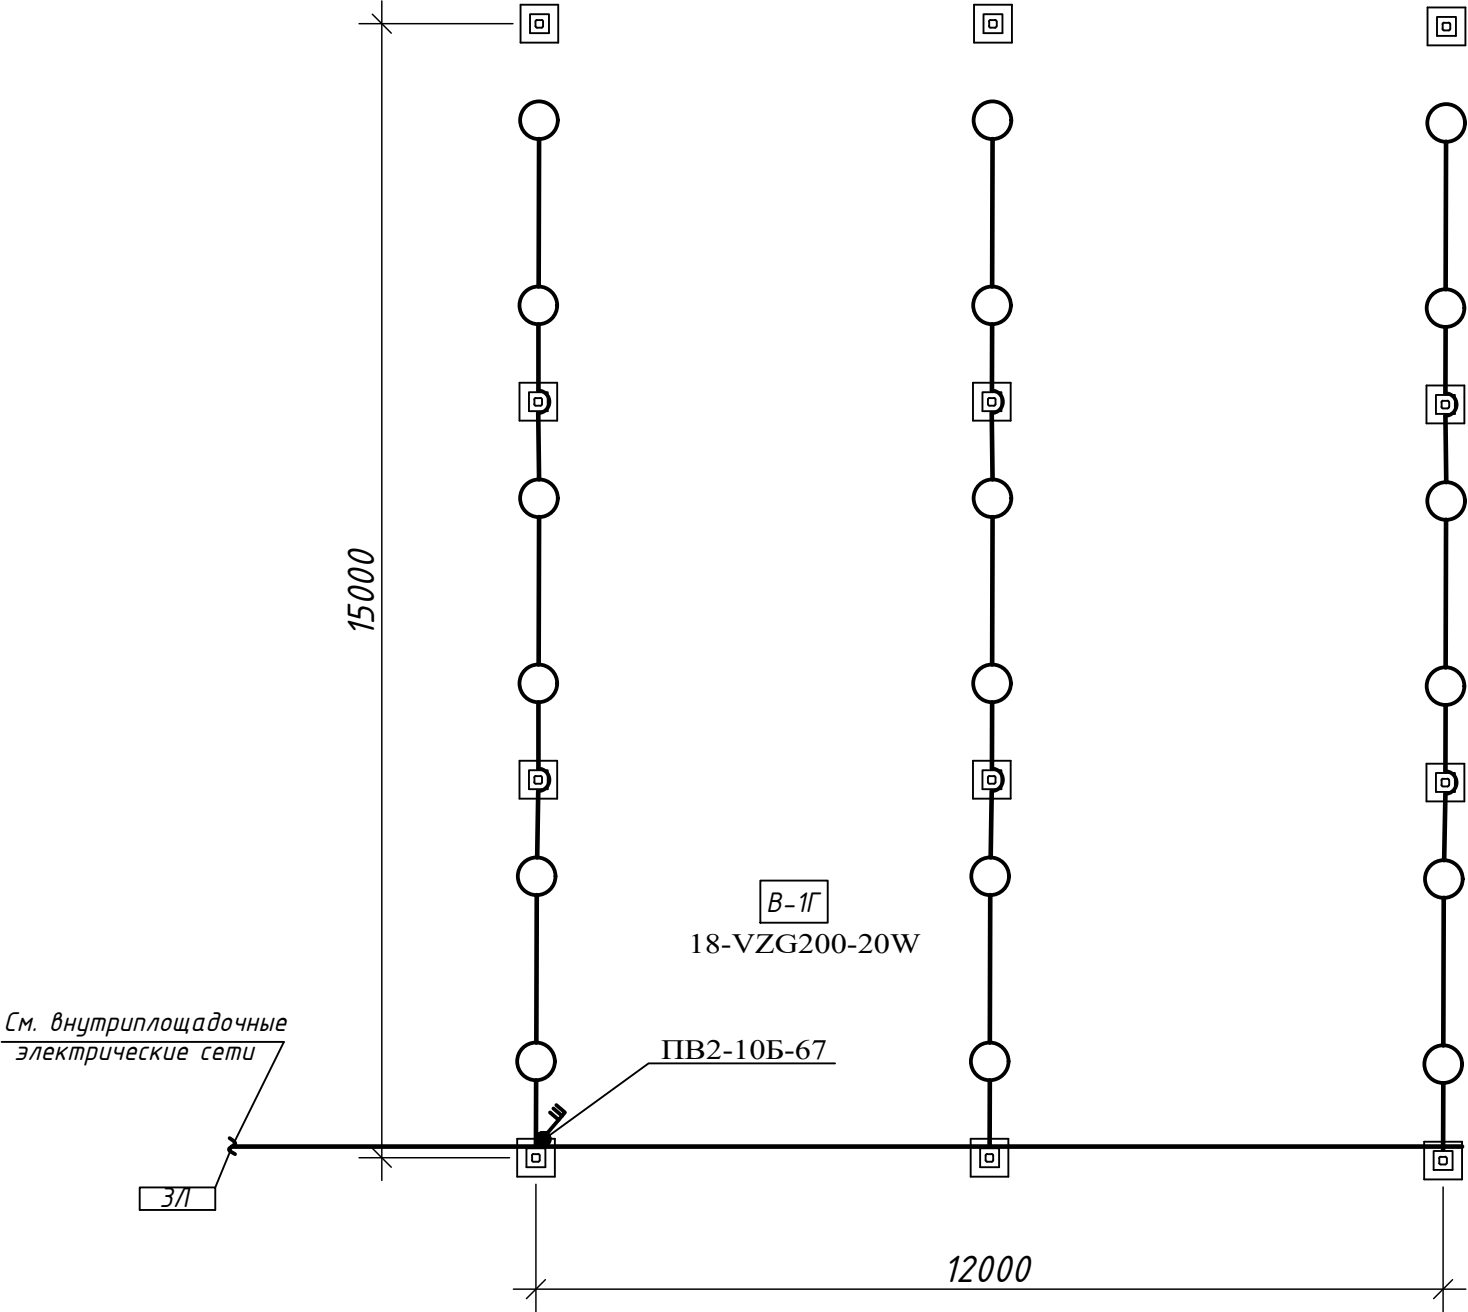

Ведомость узлов установки электротехнического оборудования на плане расположения				
Поз.	Обозначение	Наименование	Кол.	Примечание
1		Светильник светодиодный VZG200 20Вт,220В	18	
2		Светодиодная лампа 20 Вт;220 В	18	
3	ГОСТ 16442-80	Кабел и провода ВВГнг-0,06 сеч.3х4мм2	70	м
4	ТУ36-1859-80	Коробка У409У1	18	
5	ТУ36-1434-82	Полоса К200У2 L=2,0 м	60	м
6	ГОСТ3262-75	Труба стальная водогазопроводные Ф20х2,8мм	60	м
7		Метизы	0,5	кг

						000-26 -ГРС -3- ЭМО			
Изм.	Кол.уч	Лист	№ док.	Подр.	Дата	ГРС. Навес (12,0х15,0м)	Стадия	Лист	Листов
Нач. отд.		Бабаев					РП	2	
Исполн.		Ахмедов				Расположение электрического оборудования и прокладки электрических сетей. План на отм. 0,000. 1:100. Электроосвещение		 UZTRANS-GAZ «TRANSGAZINJINIRING» MCHJ	

