

Общие указания

Настоящий проект выполнен на основании задания на проектирование от ГИПа и смежных отделов.

Рабочие чертежи разработаны в соответствии с действующими нормами, правилами и стандартами.

Настоящим проектом решается электроосвещение и силовое электрооборудование операторной 1

Электроосвещение силовое электрооборудование.

Проектом предусмотрено общее рабочее освещение.

Напряжение у ламп рабочего освещения-220 V.

Установленная мощность электроприемников составляет 14,888kW,
расчетная-12,0kW.

Расчет освещения произведен методом удельной мощности W/m^2 .

Величины освещенности выбраны в соответствии с КМК2.01.05-98.

Групповые сети освещения выполняются кабелем марки ВБШвнг по полосе.

Управление освещением осуществляется автоматическими выключателями со щитка освещения в приборной.

Оружающая среда нормальная.


Защитные мероприятия.

Все металлические нетоковедущие части электрооборудования, нормально не находящиеся под напряжением заземлить, используя нулевые жилы кабелей питающих и распределительных сетей, специально проложенную от ближайшей ответвительной коробки третью жилу кабеля.

Все монтажные работы выполнить в соответствии с требованиями ПУЭ, КМК 2.04.17-19, ВСН-332-74.

Инв. N подл.	Изм.	Кол.	Лист	№ Док.	Подпись	Дата	000-26- ГРС -1- ЭМО	Стадия	Лист	Листов
Инв. N подл.	Исполн.	Ахмедов					ГРС. Операторная (проект.) поз.1	РП	1.1	3
Инв. N подл.	Исполн.	Ахмедов					Общие данные.		UZTRANS-GAZ «TRANS-GAZINJINIRING» MCHJ	
Инв. N подл.	Исполн.	Ахмедов					Общие данные.		UZTRANS-GAZ «TRANS-GAZINJINIRING» MCHJ	
Инв. N подл.	Исполн.									

ВЕДОМОСТЬ РАБОЧИХ ЧЕРТЕЖЕЙ ОСНОВНОГО КОМПЛЕКТА									
Лист		Наименование					Примечание		
1		Общие данные					2 листа		
2		Расположение электрического оборудования и прокладки электрических сетей.							
		План на отм. 0,000. 1:100. Электроосвещение и силовое электрооборудование							
3		ПР.Принципиальная электрическая схема							
ВЕДОМОСТЬ ССЫЛОЧНЫХ И ПРИЛАГАЕМЫХ ДОКУМЕНТОВ									
Обозначение			Наименование				Примечание		
			<u>Прилагаемые документы</u>						
000-26- ГРС -1- ЭМО.С			Спецификация оборудования						
000-26- ГРС -1- ЭМО.ВР			Ведомость работ						
Условные обозначения									
-светильник с люминесцентными лампами -коробка ответвительная 200lx -Освещенность в люксах ДСП1304-18W -Количество светильников, тип светильника, мощность ламп и высота подвеса									
Инв.№ подл.	Подп. и дата	Взам. инв. №					000-26- ГРС -1- ЭМО		Лист
									1.2
			Изм.	Кол..	Лист	№ док.			Подп.

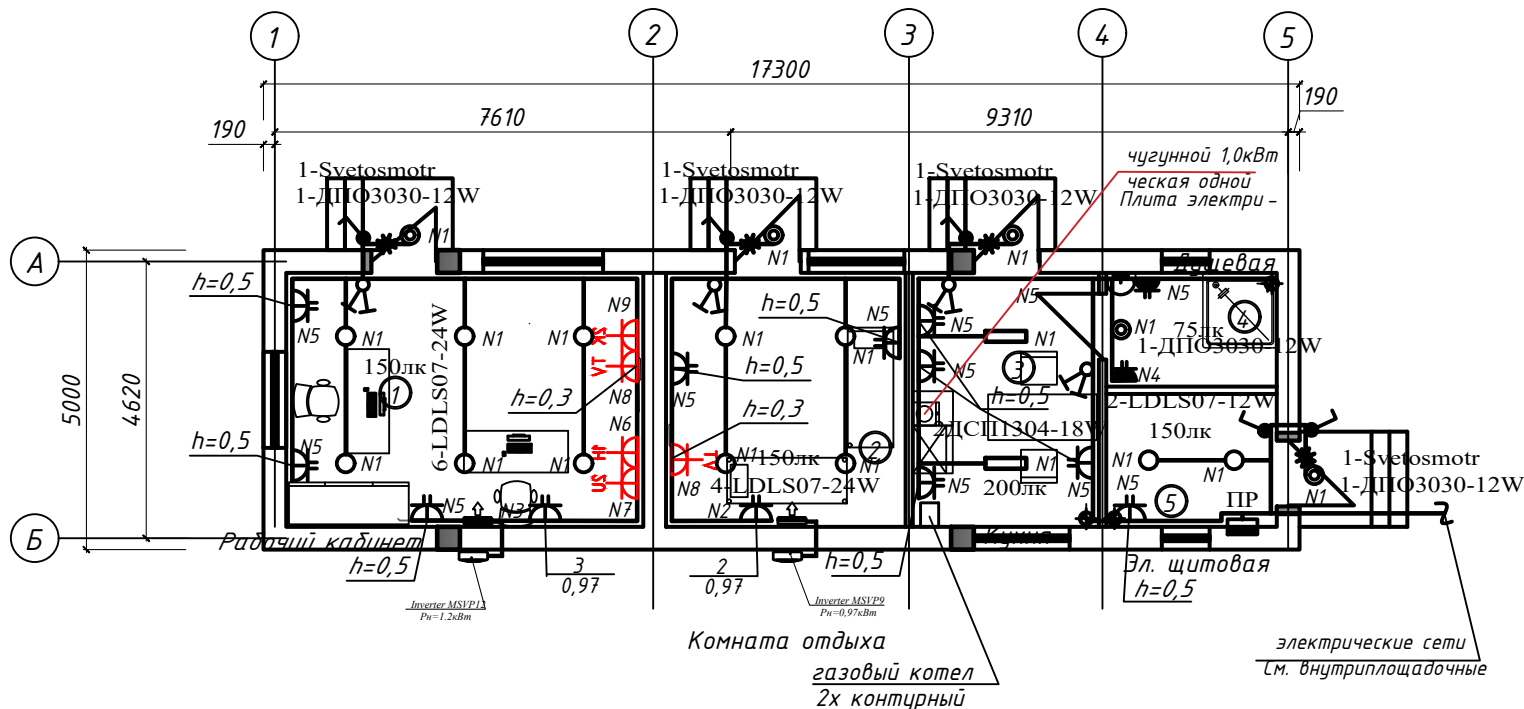

- Розетка HDMI Кабель HDMI TELECOM 19M/M
- Розетка 2-USB Кабель usb 2.0 а вилка -usb а розетка, удлинитель 5 м
- Розетка TV Кабель телевизионный Rexant RG-59U+Cu
- Розетка 2-RJ45 4-х и 8-ми жильный
- Вентилятор


Экспликация помещений

Номер помещения	Наименование	Площадь, м.²	Кат. помещения
1	Рабочий кабинет	25.27	Д
2	Комната отдыха операторов	16.96	Д
3	Кухня	13.2	Д
4	Душевая	5.41	Д
5	Электрощитовая	5.98	Д

Поз.	Обозначение	Наименование	Кол.	Примечание
1		Светильник светодиодный LDLS07-24W	10	
		LDLS07-12W, ДСП1304-18W, ДПО-3030-12W	2/2/5	
		220В IP20, 220В IP56, 220В IP65		
2	ОАО "UZELEKTROAPPARAT"	Пункт распределительный навесной ПР8503С-1069	1	ПР
		с вводным автоматическим выключателем		
		ВА47-29/3 In=63A Ip=50A-1шт		
		Автоматические выключатели на отх. линиях:		
		ВА47-29/1 In=63A Ip=16A-23шт		
		Шины N и PE -1компл.		
3	ГОСТ 6323-79	Кабель ВБбШвнг 2х2,5	60	м
4		3х2,5	165	м
5		Коробка У192	15	
		Полоса К200	60	
6	"WESSEN"	Выключатель двухклавишный 220 В, 10,0 А	4	
		открытой установки IP20 ВС 10-2-0-КБ		
7		Выключатель одноклавишный 220В, 10,0А	5	
		скрытой установки IP54 ВС20-1-0-ФСр		
8	"WESSEN"	Розетка двухместная 2х полюсная для скрытой	12	
		установки 250В; 16А с заземляющим		
		контактом IP20. РС12-3-КБ		
9	АРТ-2000В	Инвертер (Стабилизатор)	1	
10	ЕРА EVN-A200-2 в	Насос водяной автоматический 200Вт	1	шт
11		Розетка двухместная 2х полюсная для открыт. ус -	2	
		тановки 250 В; 16 А с заземляющим контактом IP54		
		РС8 22-3- ФСр		

						000-26- ГРС -1- ЗМО			
Изм.	Кол.	Лист	№ док.	Подпись	Дата				
Нач. отд		Бабаев				ГРС.		Стадия	Лист
						Операторная (проект.) поз.1		РП	2
Исполн.		Ахмедов				Расположение электрического оборудования и прокладки электрических сетей. План на отм. 0,000. 1:100. Электроосвещение и силовое электрооборудование		UZTRANS GAZ «TRANSGAZINJINIRING» MCHJ	

Взаим. ш.ВН
Лист. и дата
Мин.Мод.Л.

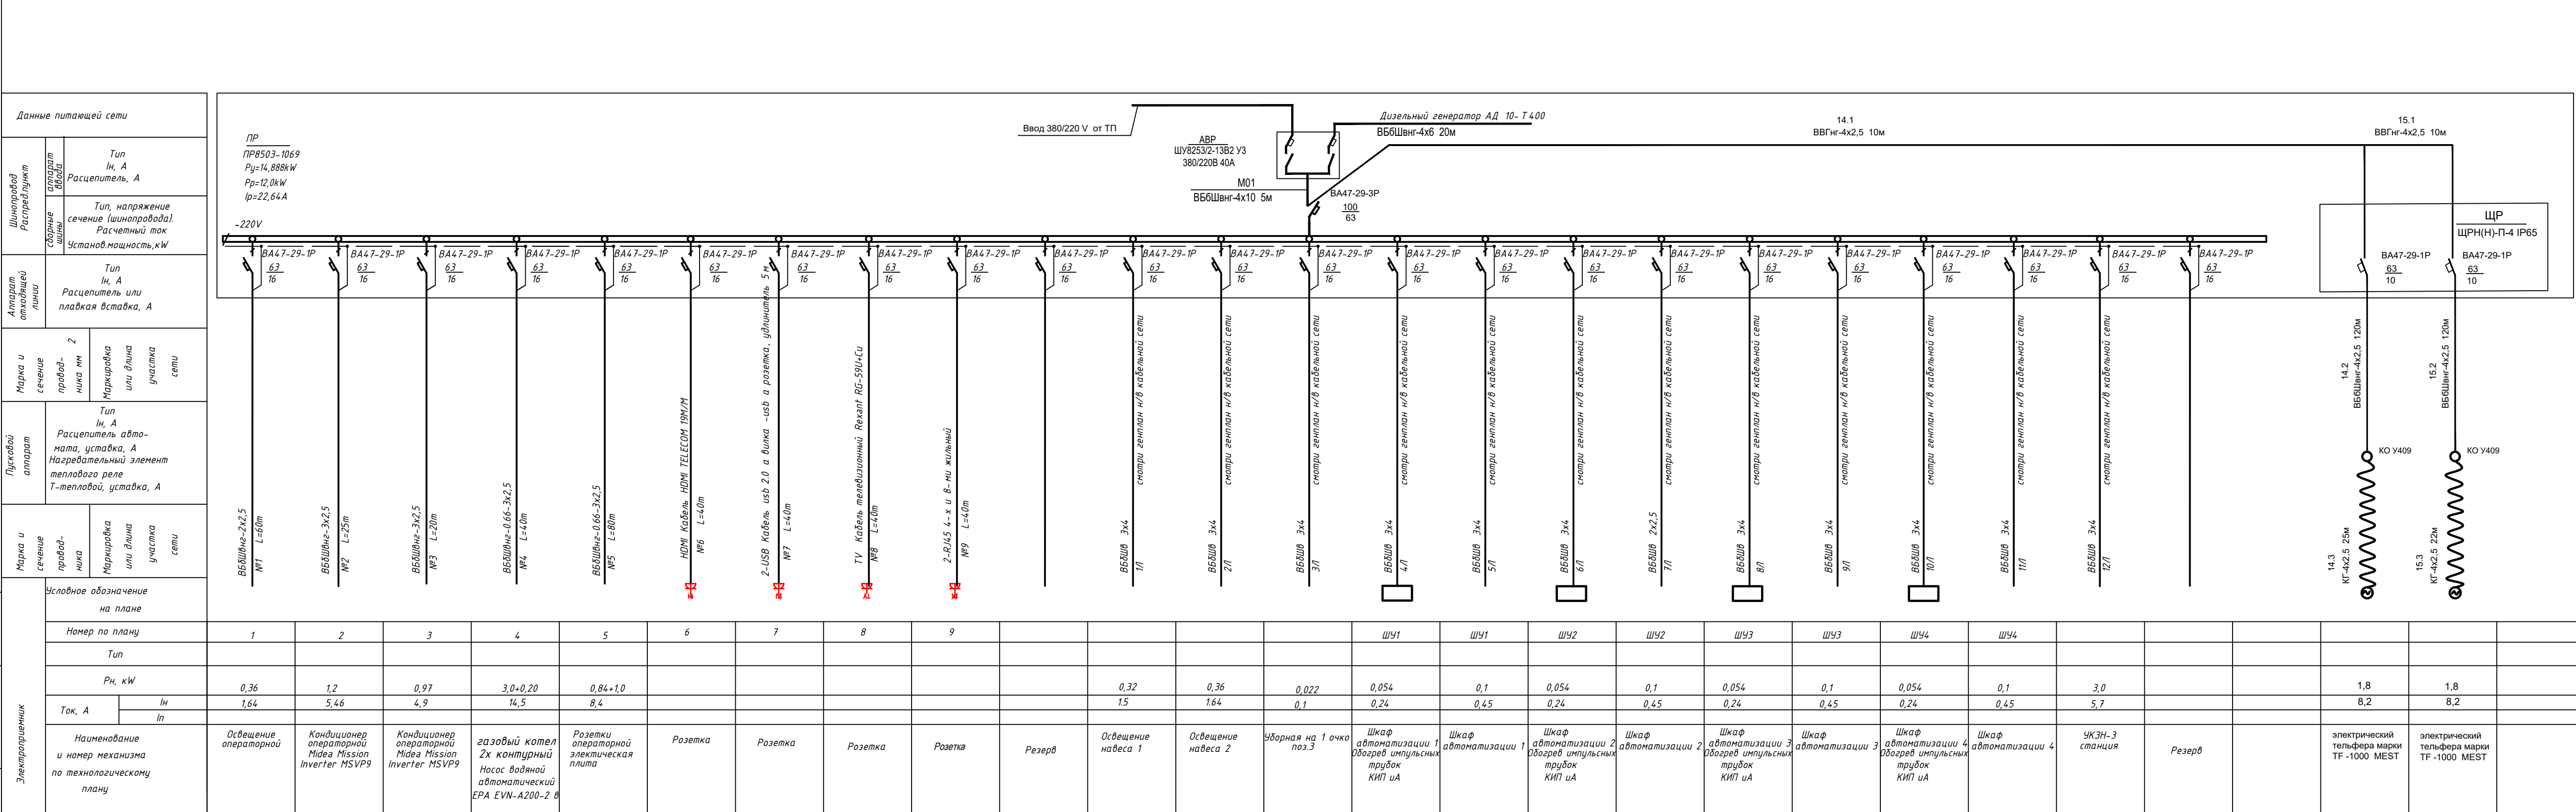

Инв.№ подл.	Подп. и дата	Взам.инв.№

Формат А3

[illegible][illegible]

