


План ограждения ГРС М1:200

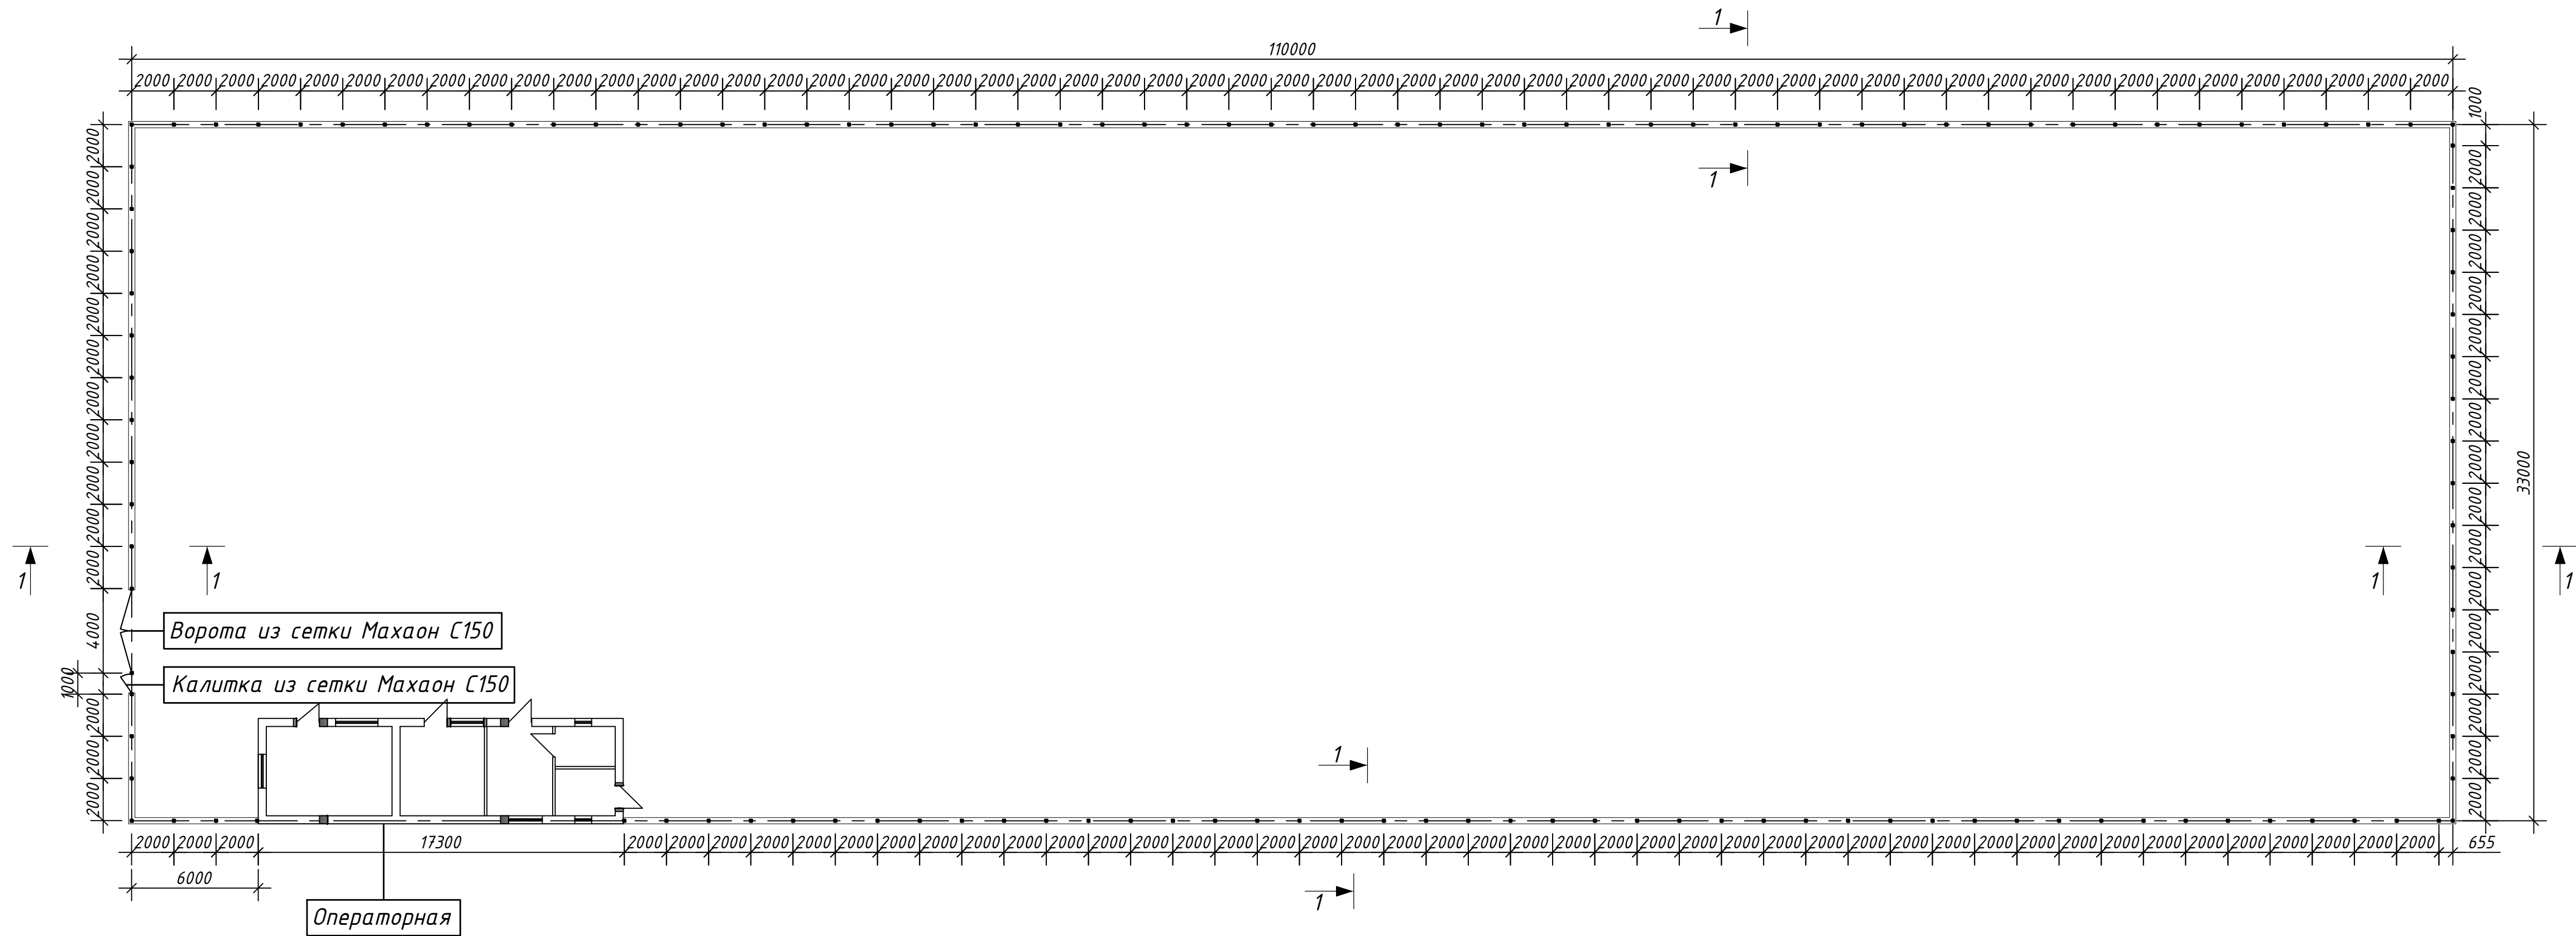


№ п.п	Наименование работ	Ед. изм.	Кол.
	Ограждения		
	<i>1. Земляные работы</i>		
1	Разработка грунта 2 группы экскаватором ковша 0,25 м³ в котловане	м³	101,2
2	Обратная засыпка пазух котлована мех. способом с послойным трамбованием и поливкой водой	м³	75,0
3	Засыпка излещинного ГПС по площадке	м³	26,2
	<i>2. Антикоррозийные мероприятия</i>		
1	Устройство щебёночной подготовки с пропиткой битумом до насыщения, толщина 0,1м	м³	6,4
2	Устройство обмазочной гидроизоляции горячим битумом		
	за 2 раза (данная площадь указана за один слой)	м²	284,2

Примечание :

1. Данный проект является предварительным для организации строительных работ.

Дата выдачи проекта: 10.07.2026

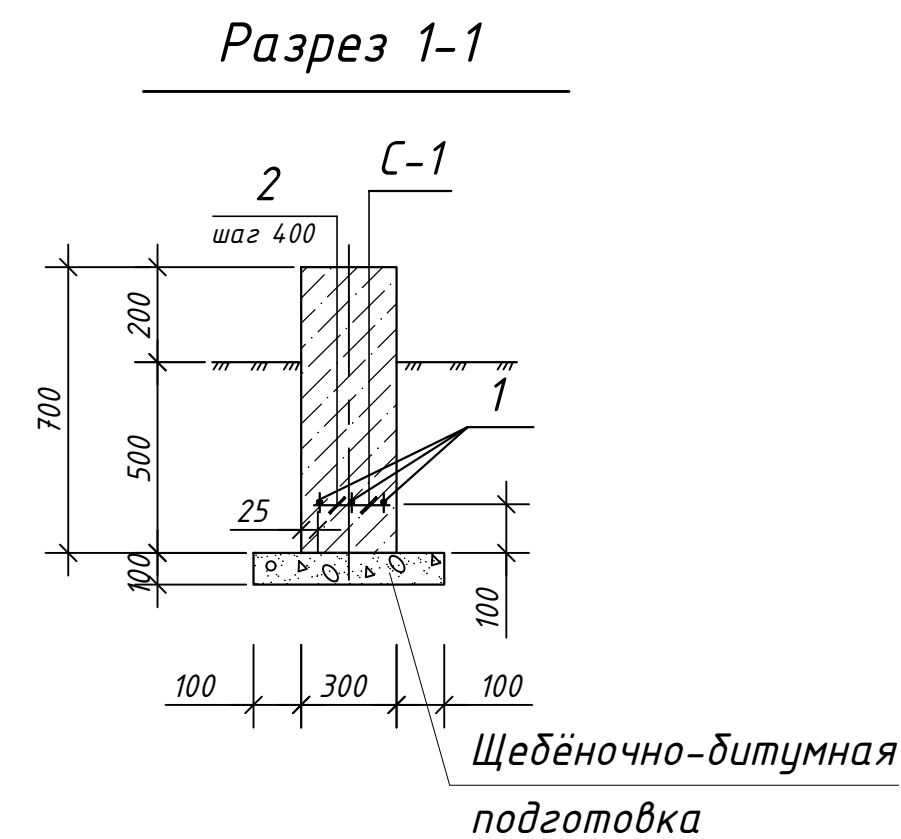


Спецификация металла на ограждение площадки ГРС.

Поз.	Обозначение	Наименование	Кол. шт	Масса ед. кг	Примеч.
1	2	3	4	5	6
ЗД-1	данный лист	Закладная деталь ЗД-1	136	1,06	144,2
1	ГОСТ 19903-74*	-150x150x6 мм	1,0	1,06	1,06

Спецификация элементов на фундамент ограждения ГРС.

Поз.	Обозначение	Наименование	Кол. шт	Масса ед. кг	Примеч.
1	2	3	4	5	6
		Фундамент под ограждение	264,0 п.м		
		Сетка С-1			
1	ГОСТ 5781-93	Ø10AIII Лодж -264000 мм	3,0	162,9	488,7
2	ГОСТ 5781-93	Ø10AIII Лодж -250 мм	662	0,15	99,3
		Бетон кл В 12.5 (М-150)		56,4 м ³	
		на сульфатостойком			
		цементе			

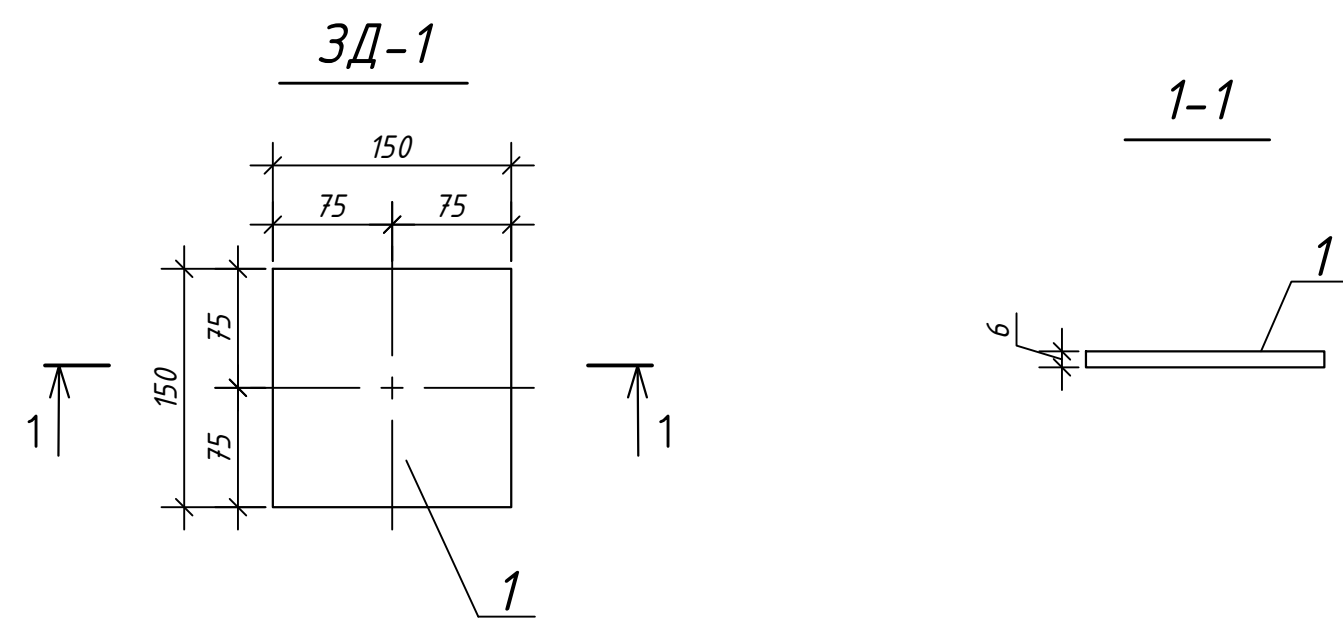

Примечание:

1. Данный лист сотреть совместно с листом АС-2.
2. Сварку производить электродами Э-42 А по ГОСТ 9467-93.
3. Под фундамент выполнить щеденочную подготовку с пропиткой битумом до насыщения толщиной 100мм см лист АС-5.
4. Основание подготовки уплотнить с послойным трамбованием и поливкой водой.
5. Закладные детали ЗД-1 установить в теле фундамента ограждения.

Антикоррозийные мероприятия.

В основании фундаментов выполнить щебеночную подготовку с пропиткой битумом до насыщения. Боковые поверхности плит, соприкасающиеся с грунтом, обмазать горячим битумом за 2 раза.

						Строительство нового ГРС для газоснабжения ТЭЦ мощностью 1500-1600МВт							
Изм.	Колуч	Лист	№ док.	Подп.	Дата								
Нач. отд.	Бабаев						Газораспределительная станция						
							<table><tr><td>Стадия</td><td>Лист</td><td>Листов</td></tr><tr><td>РП</td><td>1</td><td>2</td></tr></table>	Стадия	Лист	Листов	РП	1	2
Стадия	Лист	Листов											
РП	1	2											
Исполнит.	Одилов					План ограждения. Разрез 1-1							
						<table><tr><td></td><td>UZTRANS-GAZ «TRANSGAZINJINIRING» MCHJ</td></tr></table>		UZTRANS-GAZ «TRANSGAZINJINIRING» MCHJ					
	UZTRANS-GAZ «TRANSGAZINJINIRING» MCHJ												