

Вид со стороны неохраняемой территории

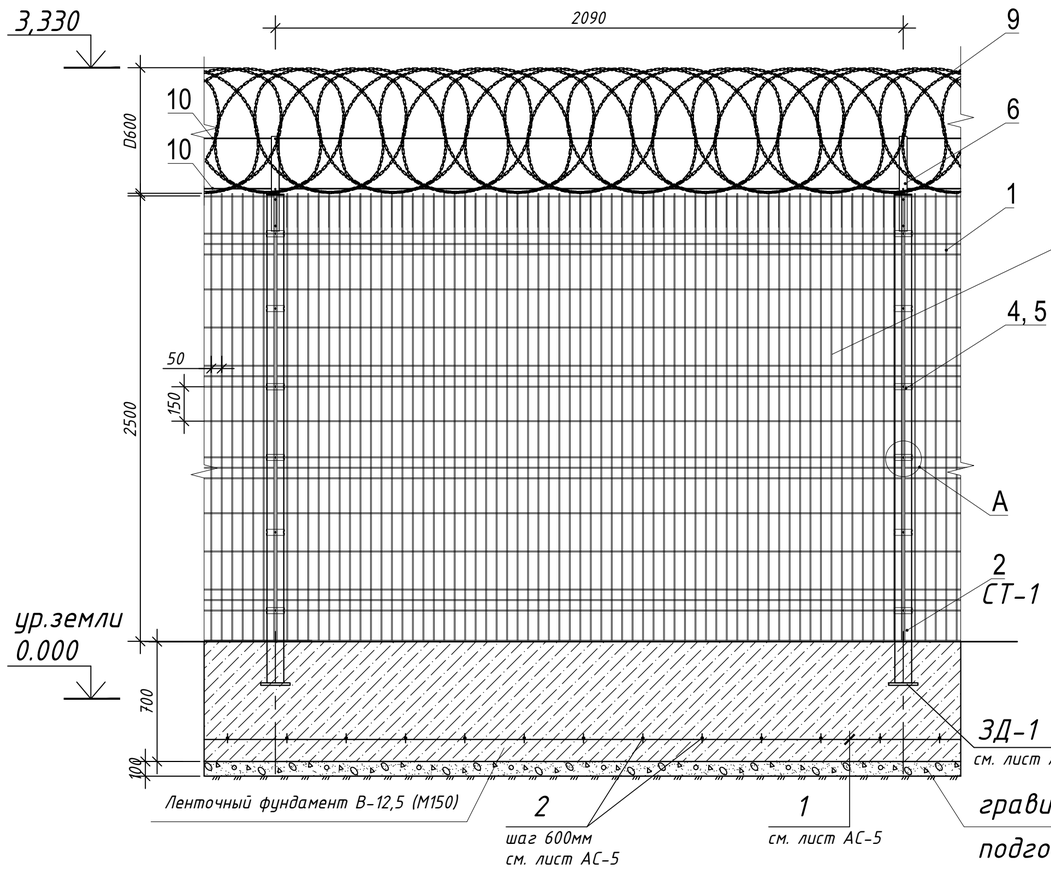



Ограждение

"МАХАОН-С-150"


Разрез 1-1

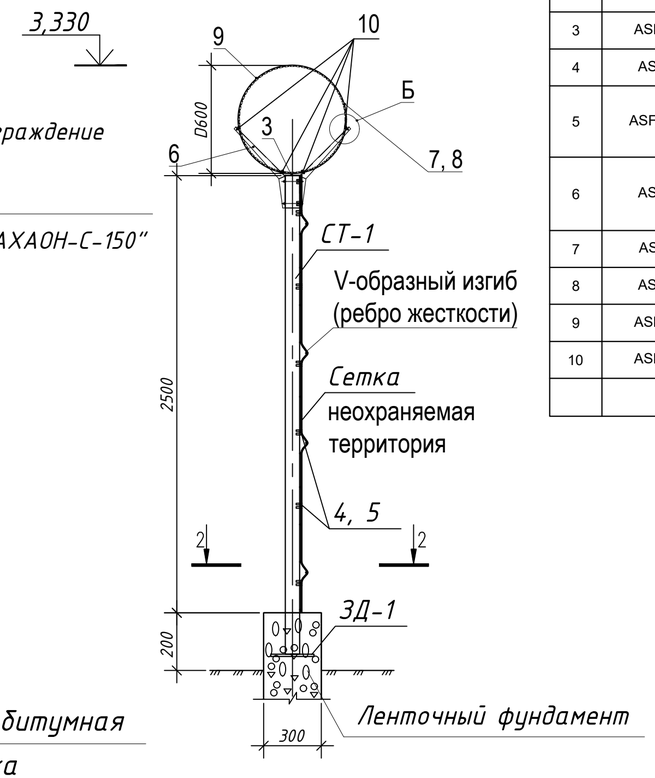

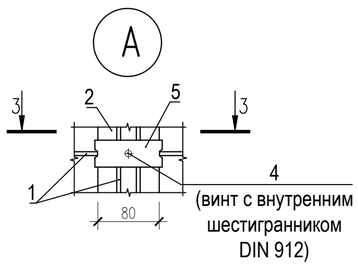


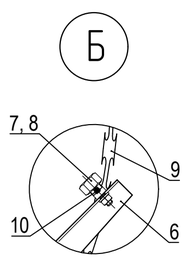


3 - 3

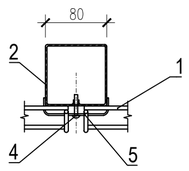

2- 2

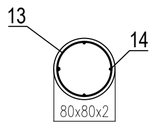

Крепление V-образной насадки

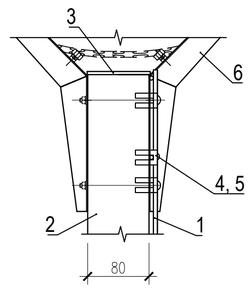

Спецификация элементов основного ограждения. Длина 2600 м.п.

Поз.	Обозначение	Наименование	Кол-во	Ед. изм.	Примечание
1	ASF_15724N	Панель усиленная ASF HxW 2030x2500 мм., ячейка 50x150мм, пруток 5мм, V-образных изгибов - 5, (Анти.корр. защита ; Вариант исполнения: стандарт; Цвет: Зеленый RAL 6005)	132	шт.	
2	ASF_13891	Столб ограждения: профиль 80x80x2 мм, L 3000 мм, под бетонирование (Антикор. защита: горячецинкованный прокат 100-275 г/м2+ полимер 60-100 мкм; Вариант исполнения: резьбовые отверстия (термосверление) под винт, без заглушки; Цвет: Зеленый RAL 6005)	136	шт.	
3	ASF_15180	Пластиковая заглушка ASF 80x80мм (Цвет: Зеленый RAL 6005)	136	шт.	
4	ASF_8932	Комплект метизов ASF для скобы (4 компл.) (винт М6)	136	шт.	
5	ASF_15512K	Комплект скоб ASF "стандарт" (4комп.) (Анти.корр защита горячецинкованный прокат 100-275 г/м2+ полимер 60-100 мкм; Исполнение стандарт; Цвет: Зеленый RAL 6005)	136	шт.	
6	ASF_8930	Насадка ASF V-образная (Размер: стандарт; Ант.корр.защита: горячецинкованный прокат 100-275 г/м2+ полимер 60-100 мкм; комплект крепежа под СББ; Цвет: Зеленый RAL 6005)	136	шт.	
7	ASF_8921	Комплект метизов ASF для скобы к насадке (4 компл.)	136	компл.	
8	ASF_8927	Комплект ASF крепления СББ к насадке (4 компл.)	136	компл.	
9	ASF_13988	СББ из АКЛ: D бухты 600 мм, витков в п.м. = 4,2; 5 клепок ГОСТ 7372-79 (рабочая длина бухты 10 м)	270	м	
10	ASF_14999	Струна для крепления СББ/ПББ оцинкованая d2,5 мм (Длина бухты 400 м)	1080	м	

Примечание :

1. Данный проект является предварительным для организации строительных работ.

Дата выдачи проекта: 10.07.2026

Антикоррозийные мероприятия.

В основании фундаментов выполнить щебеночную подготовку с пропиткой битумом до насыщения. Боковые поверхности плит, соприкасающиеся с грунтом, обмазать горячим битумом за 2 раза.

Изм.	Кол.уч	Лист	№док.	Подп.	Дата	Строительство нового ГРС для газоснабжения ТЭЦ мощностью 1500-1600МВт			
Нач. отд.		Бабаев				Газораспределительная станция	Стадия	Лист	Листов
							РП	2	2
Исполнит.		Одилов				Фрагмент ограждения Махаон	UZTRANSGAZ «TRANSGAZINJINIRING» MCHJ		

Взам.инв.№ | Подп. и дата | Инв.№подл.

Формат А 2