

Общие указания

Настоящий проект разработан на основании задания на проектирование от заказчика.

Рабочие чертежи разработаны в соответствии с действующими нормами, правилами и стандартами.

Для предупреждения возможности развития пожара проектом предусмотрено устройство системы пожарной сигнализации.

В качестве приемного устройства принят прибор пожарной сигнализации типа "ППСУ-10" установленный в операторной (поз.1 по ГП).

В помещениях, контролируемых от пожара приняты дымовые оптико-электронные извещатели типа Аврора-ДН, а также ручные извещатели WR2001:R.

Во взрывоопасных зонах к установке приняты взрывобезопасные ручные извещатели WR4001 I.S.

По степени обеспечения надежности электроснабжения электроприемники ОПС относятся к первой категории.

Для бесперебойной работы "БРОП" и извещателей проектом предусмотрено резервное питание от аккумулятора 12V/2.2 А*ч.

Внутриплощадочные сети выполнены кабелями марок КВБбШв 4х1,5, проложенным в траншее на глубине 0,7м

При пересечении с подземными коммуникациями и дорогами, кабель следует проложить в асбестоцементных трубах.

Инв. № подл.	Взам. инв. №										
Подп. и дата								000-26 -ГРС -ПС			
								"Surxondaryo viloyatidagi quvvati 1500–1600 MVt boʻlgan bugʻ-gaz elektr stansiyasini tabiiy gaz bilan taʼminlash"			
		Изм.	Кол.уч	Лист	№ док.	Подп.	Дата				
		Нач. отд.	Бабаев								
								ГРС Пожарная сигнализация	Стадия	Лист	Листов
Инв. № подл.									РП	1.1	8
		Исполн.	Ахмедов					Общие данные	 UZTRANS-GAZ «TRANS-GAZINJINIRING» MCHJ		


ВЕДОМОСТЬ РАБОЧИХ ЧЕРТЕЖЕЙ ОСНОВНОГО КОМПЛЕКТА											
Лист		Наименование						Примечание			
1.1-1.3		Общие данные									
2		Внутриплощадочные сети (поз.0 по ГП) 1:100									
3		Операторная (поз.1 по ГП). План на отм. 0,000. 1:100									
4		Схема электрическая соединений устройств									
5		Схема соединений шлейфов пожарной сигнализации (начало)									
6		Схема соединений шлейфов пожарной сигнализации (окончание)									
ВЕДОМОСТЬ ССЫЛОЧНЫХ И ПРИЛАГАЕМЫХ ДОКУМЕНТОВ											
Обозначение			Наименование						Примечание		
			Прилагаемые документы								
000-26 -ГРС -ПС.С1			Спецификация оборудования								
			Внутриплощадочные сети (поз.0 по ГП)								
000-26 -ГРС -ПС.С2			Спецификация оборудования								
			Операторная (поз.1 сущ. по ГП).								
ВЕДОМОСТЬ ССЫЛОЧНЫХ И ПРИЛАГАЕМЫХ ДОКУМЕНТОВ											
Обозначение			Наименование						Примечание		
			Прилагаемые документы								
000-26 -ГРС -ПС.ВР1			Ведомость объемов работ.								
			Внутриплощадочные сети (поз.0 по ГП)								
000-26 -ГРС -ПС.ВР2			Ведомость объемов работ.								
			Операторная (поз.1 сущ. по ГП).								
000-26 -ГРС -ПС.Ж			Кабельный журнал.								
Инв. № подл.											
								000-26 -ГРС -ПС			
		Изм.	Колуч	Лист	Ндок.	Подп	Дата				
Взам. инв. №											
Подп. и дата											
Лист											
1.2											

УСЛОВНЫЕ ОБОЗНАЧЕНИЯ

	Станция пожарной сигнализации БРОП
	Звуковой оповещатель ЕМА1224
	ПУЦ ,ЩМП
	Дымовой извещатель Аврора - ДН
	Тепловой взрывозащищенный извещатель 5451EIS
	Ручной пожарный извещатель WR 2001:R ,WR4001 I.S
	Извещатель охранный на открывание СМК
	Извещатель охранный Икар -2
	Ответвительная коробка УК-2 П
	Провод ППВ 2 х 1,5
	Кабель КПСВВ 1 х 2 х 0,5 , КСВПВ 2 х 2 х 0,50 , КВБДШв 4 х 1,5 ,
	Кабели КВБДШв 4 х 1,5 ,
	Кабели КВБДШв 4 х 1,5 , в а/ц труде

Инв. № подл.	Подп. и дата	Взам. инв. №

						000-26 -ГРС -ПС	Лист
							1.3
Изм.	Кол.уч	Лист	Ндок.	Подп	Дата		

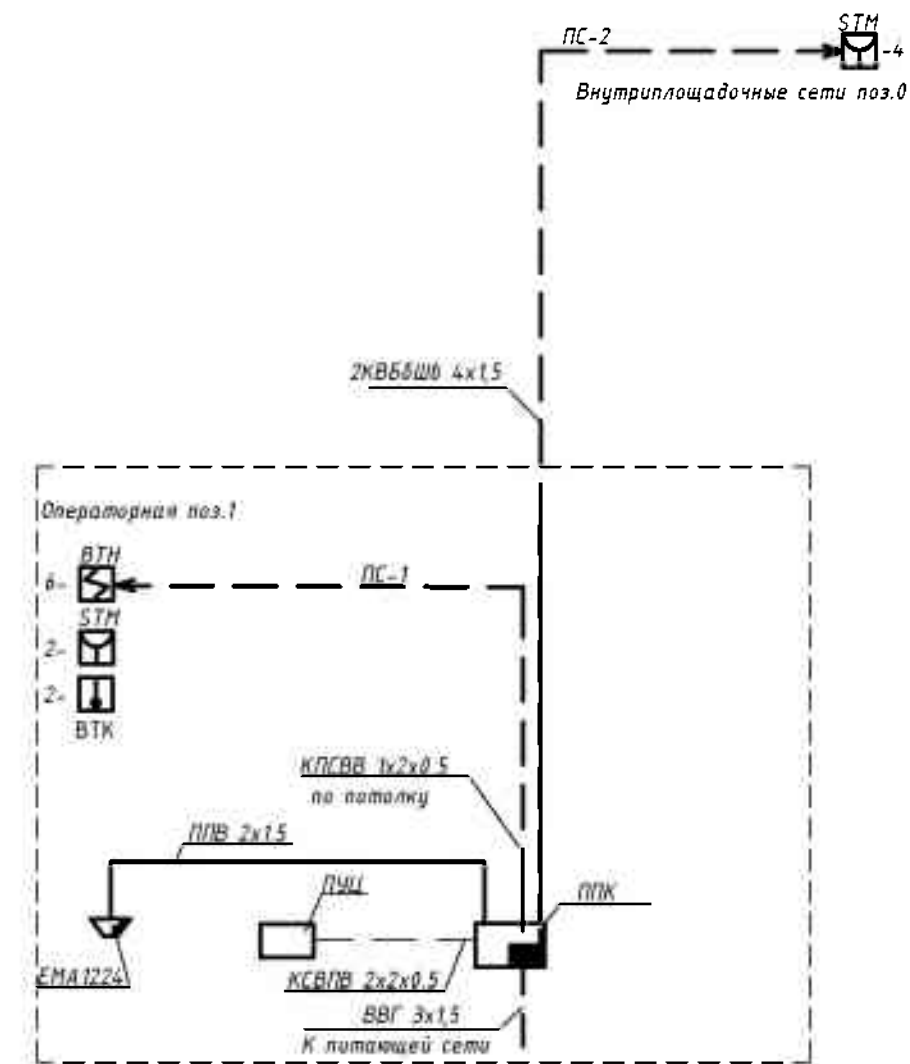[illegible]

Номер помещения	Наименование	Площадь м ²
1	Рабочий кабинет	21.03
2	Кухня	7.52
3	Комната отдыха	12.04
4	Душевая	5.9
5	Эл. щитовая	5.9
6	Коридор	7.52

						000-26 - ГРС - ПС			
Изм.	Кол.	Лист	№ док.	Подпись	Дата				
Нач. отд.	Бабаев					ГРС.		Стадия	Лист
						Пожарная сигнализация		РП	3
						Операторная (поз.1 по ГП).			
Исполн	Ахмедов					План на отм. 0,000. 1:100		 UZTRANS-GAZ «TRANSGAZINJINIRING» MCHJ	


Формат А3х4

АППВ 3х2,5
~220V от ПР

ППСУ-10

X5	
Конт	Цель
1	Сеть ~220V
2	Сеть ~220V

X6	
Конт	Цель
1	В0-1
2	В0-2
3	В0-3

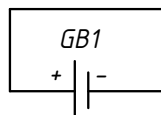

Акк(+)
Акк(-)

Корпус

X1									
Конт	Цель	ВИ-	ВИ+	ОШ	ОП	-12V	+12V	СИР+	СИР-
1									
2									
3									
4									
5									
6									
7									
8									
9									
10									

ЕМА 1224	
Цель	Конт
ОПОВ	1
ОПОВ	2

ППВ 2х1,5

X4	
Цель	Конт
+Ш1	1
-Ш1,2	2
+Ш2	3
+Ш3	4
-Ш3,4	5
+Ш4	6
+Ш5	7
-Ш5,6	8
+Ш6	9
+Ш7	10
-Ш7,8	11
+Ш8	12
+Ш9	13
-Ш9,10	14
+Ш10	15

X3	
Цель	Конт
ПУЛ+	3
ПУЛ-	2
+5V	1

X2			
Конт	Цель	СЛ-	СЛ+
1			
2			
3			

ПУЦ	
Цель	Конт
+5V	1
СЛ+	2
СЛ-	3

Цель	Конт
К+	1
К-	2
Д+	3


КПСВВ 1х2х0,5

2КВБШВ 4х1,5
(см.внутриплощадочные сети)

КСВПВ 2х2х0,5

Взам.инв.№											
Подп. и дата							000-26 - ГРС - ПС				
	Изм.	Кол.уч	Лист	И док.	Подп.	Дата					
	Нач. отд.	Бабаев									
Инв.№-подл.							ГРС. Пожарная сигнализация		Стадия РП	Лист 4	Листов
	Исполн	Ахмедов					Схема электрическая соединений устройств		UZTRANS-GAZ «TRANSGAZINJINIRING» MCHJ		
									Формат А3		


Инв.№ подл.	Подп. и дата	Взаим.инв.№

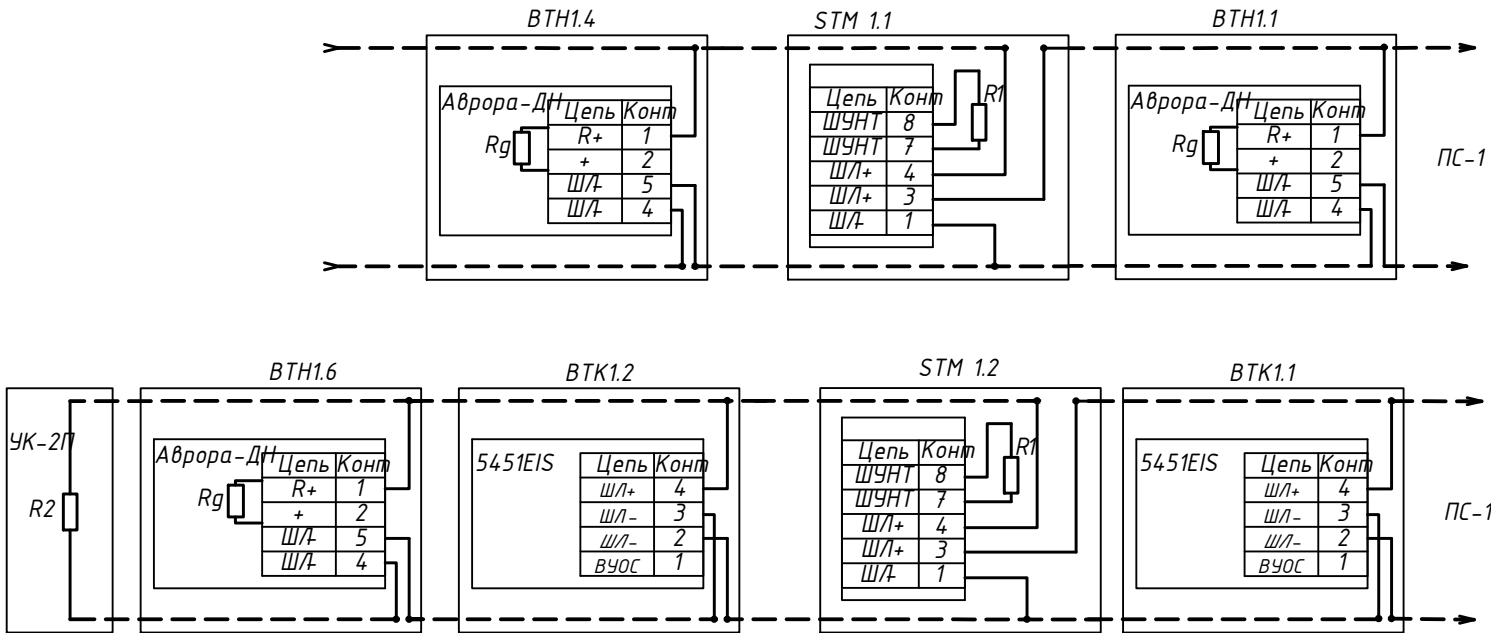

						000-26 -ГРС -ПС		
Изм.	Кол.	Лист	№ Док.	Подпись	Дата	ГРС. Пожарная сигнализация	Стадия	Лист
Нач. отд.		Бабаев					РП	5
Исполн		Ахмедов				Схема соединений шлейфов пожарной сигнализации (начало)	 UZTRANS-GAZ «TRANSGAZINJINIRING» MCHJ	

Инв.№ подл.	Подп. и дата	Взаим.инв.№

Внутриплощадочные сети поз.0

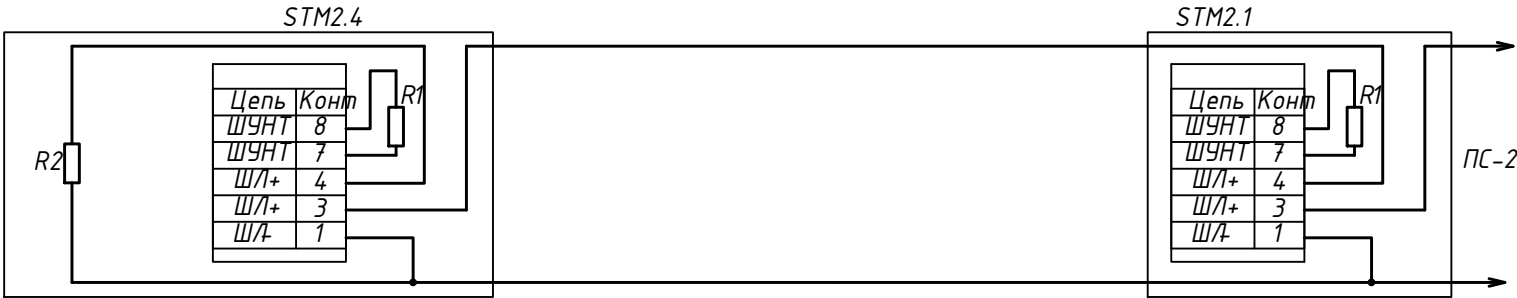

						000-26 - ГРС - ПС			
Изм.	Кол.	Лист	N Док.	Подпись	Дата	ГРС. Пожарная сигнализация	Стадия	Лист	Листов
Нач. отд.	Бабаев						РП	6	
						Схема соединений шлейфов пожарной сигнализации (окончание)	 UZTRANSGAZ «TRANSGAZINJINIRING» MCHJ		
Исполн	Ахмедов								

[illegible]

Формат А3

Инв. № подл.	Взам. инв. №
Подп. и дата	

Пози- ция	Наименование и техническая характеристика	Тип, марка обозначение документа опросного листа	Код оборудования изделия материала	Завод - изготовитель	Еди- ница изме- рения	Коли- чество	Масса единицы, kg	Примечание
	<u>Поставка заказчика</u>							
1	Ручной пожарный извещатель для взрывоопасных зон (исп. IP67)	WCP3A-R000SF-S214-01IS		"System-Sensor"	шт.	4		
				г.Москва				
2	Кабель контрольный с медными жилами бронированный сеч. 4 x 1,5 мм ²	КВБбШв			км	0,268		
		ГОСТ 1508-78						
	<u>Поставка подрядчика</u>							
1	Труба асбестоцементная БНТ 100, l=2950 мм	ГОСТ 1839-80			шт	6		
2	Труба 25x2,8	ГОСТ 3262-75			м	18		
3	Швеллер L=2 м	K240Y2			шт	3		

						000-26 - ГРС - ПС.С 1					
Изм.	Кол.уч	Лист	N док.	Подп.	Дата				Стадия	Лист	Листов
Нач. отд.	Бабаев					ГРС. Пожарная сигнализация			РП		1
Исполн	Ахмедов					Спецификация оборудования. Внутриплощадочные сети (поз.0 по ГП)			 UZTRANSGAZ «TRANSGAZINJINIRING» MCHJ		

Инв. № подл.	Подп. и дата	Взам. инв. №



UZTRANS-GAZ
«TRANSGAZINJINIRING»
MCHJ

Инв. № подл.	Взам. инв. №	Подп. и дата	000-26 - ГРС - ПС. ВР 1 ГРС. Пожарная сигнализация Ведомость объемов работ. Внутриплощадочные сети						Стадия РП	Лист	Листов 1
			Изм.	Кол.уч.	Лист	И док.	Подп.	Дата			
			Нач. отд.	Бабаев							
			Исполн	Ахмедов							

NN п/п	Наименование вида работ	Ед.изм.	Кол.	Примечание
1	Прокладка кабель контрольный с медными жилами бронированный КВБбШвнг сеч.4 х 1,5 мм ²	м	268	
2	Прокладка кабеля по конструкциям КВБбШвнг сеч.4х1,5мм ²	м	20	
3	-в трубе 25х2,8	м	10	
4	-в траншее в асбестоцементной трубе	м	18	
5	Укладка кабеля в траншею	м	230	
6	Крепление кабеля к швеллеру	м	2,0	
7	Укладка асбестоцементной трубы в траншею	шт.	6	
8	Установка швеллера К240У2	шт.	3	
9	Крепление извещателя WRIS/4001 F к швеллеру	шт.	4	
10	Установка и монтаж ручного пожарного извещателя	шт	4	
	<u>Земляные работы</u>			
9	Рытье траншеи ручным способом для прокладки кабеля в грунте 2-й категории			
	L=230м	м ³	161,0	
10	Обратная засыпка траншеи	м ³	161,0	
11	Копание ям ручным способом (4 ямы)	м ³	1,5	
12	Засыпка ям ручным способом (4 ямы)	м ³	1,5	

№ п/п	Наименование вида работ	Ед.изм.	Кол.	Примечание
1	Установка и монтаж прибора приемно-контрольного охранно-пожарного ППСЧ-10 на стене	шт	1	
2	Установка и монтаж аккумулятора 12 V/2.2Ah в ППСЧ-20 на стене	шт	1	
3	Установка и монтаж звукового оповещателя ЕМА 1224 на стене	шт	1	
4	Установка и монтаж дымового пожарного оптико-электронного извещателя Аврора-ДН на потолке	шт	6	
5	Тепловой взрывозащищенный извещатель	шт	2	
6	Установка и монтаж ручного пожарного извещателя WR 2001:R на стене	шт	1	
7	Установка и монтаж резистора C2-33H-0.25-1.0кОм+5 % в основании извещателя	шт.	5	
8	Установка и монтаж резистора C2-33H-0.25-5.6кОм+5 % в ответвительной коробке УК-2П	шт.	3	
9	Прокладка кабеля КПСВВ 1х2х0,5 по стене	м	30	
	-по потолку	м	30	
10	Прокладка провода ППВ 2х1,5 по стене	м	10	
11	Установка и монтаж ответвительной коробки УК-2П на стене	шт.	1	
12	Установка и монтаж барьера искрозащиты KFDO-CS-Ex1.51P в ШМП-1-074 У2	шт	1	
13	Установка и монтаж контактного винтового зажима ЗВИ 3 в ШМП-1-074У2	шт	1	