




Фундамент под пылеуловитель Ø2400мм М1:50

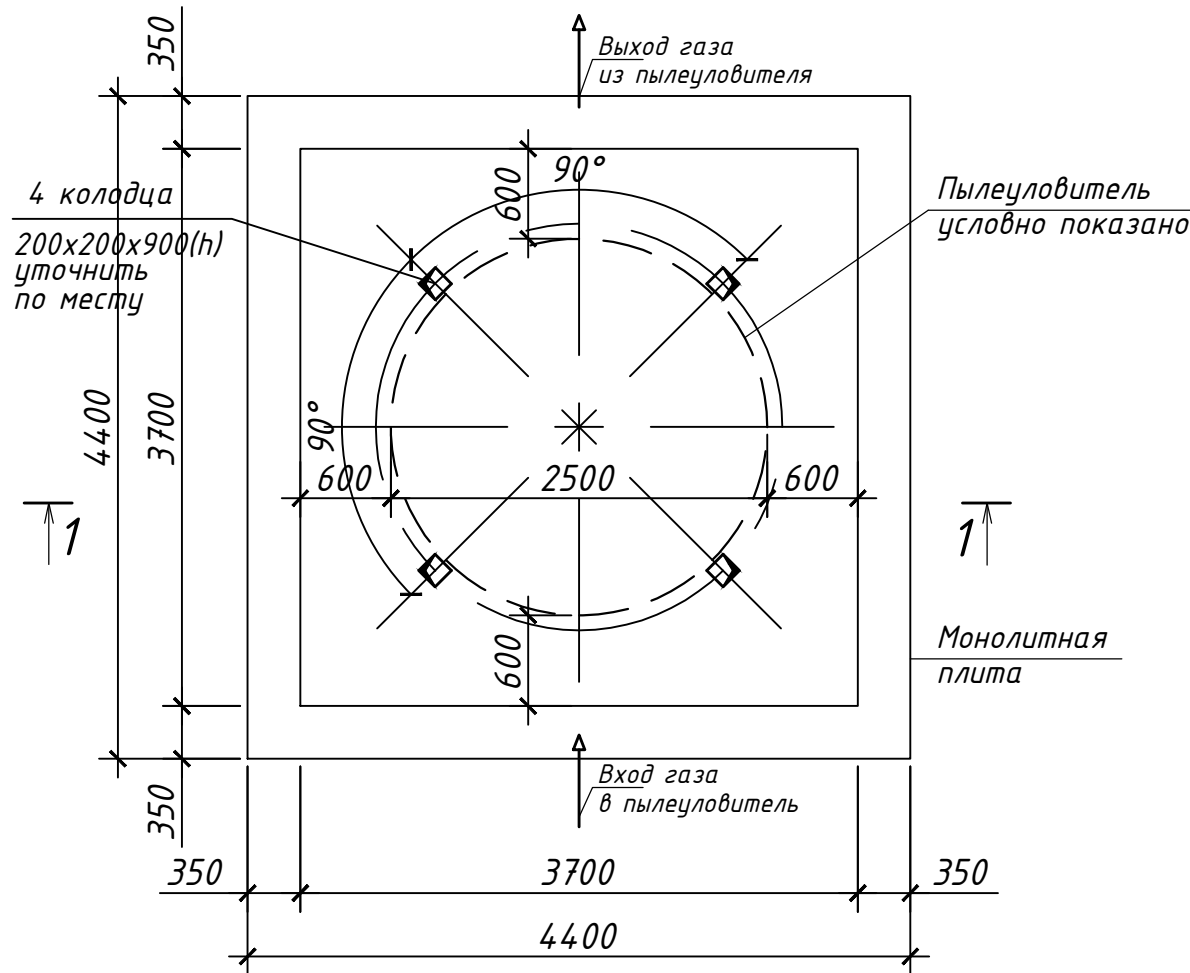


Разрез 1-1

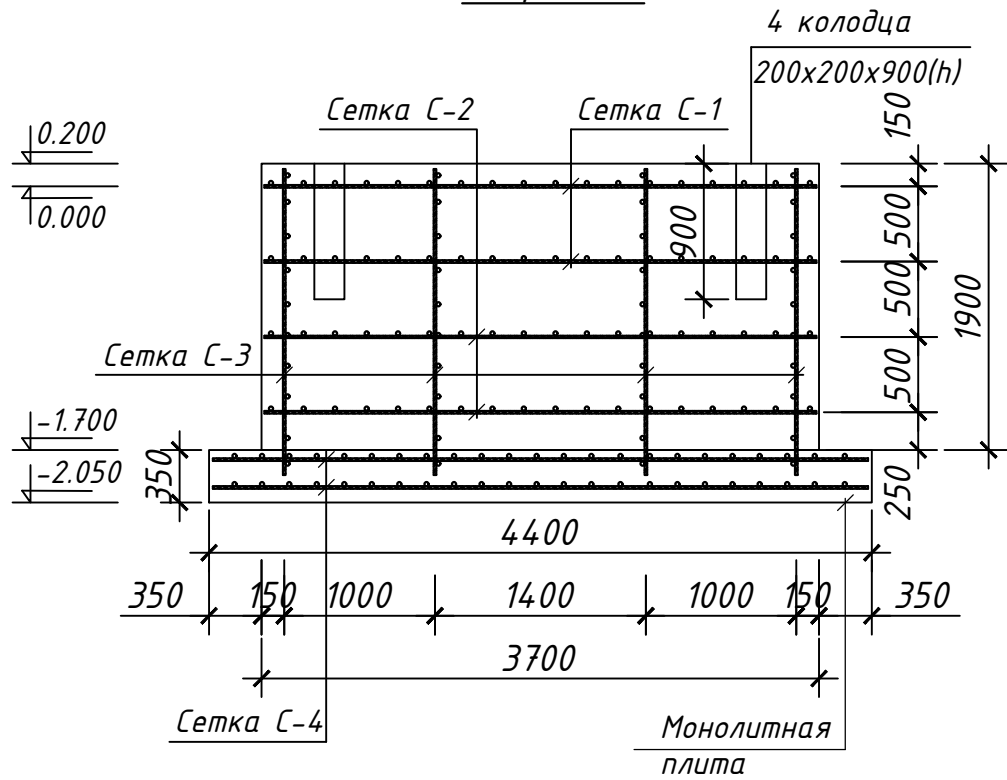


Деталь установки
арм.сетки

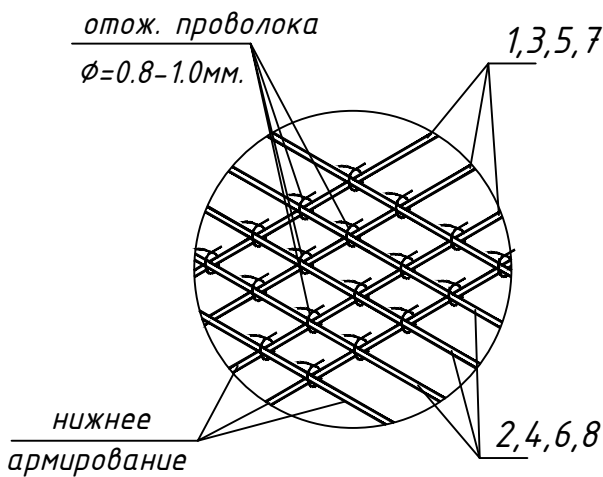


Арматурная сетка С-1 (С-2) М1:50

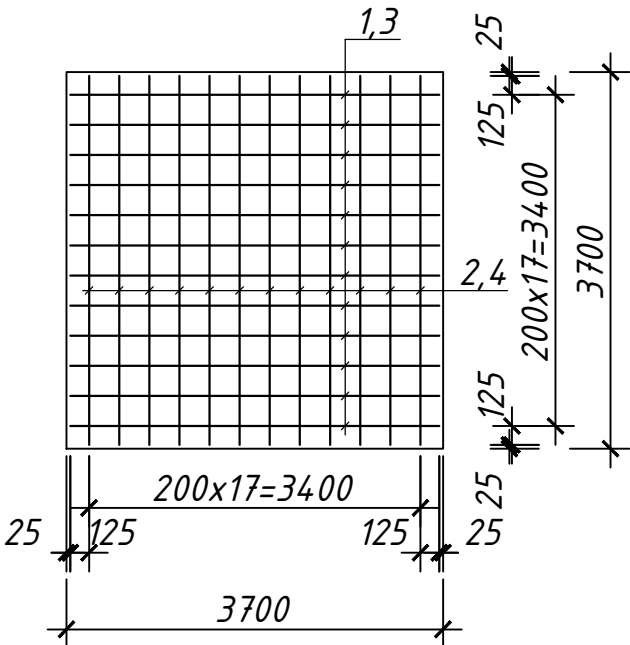

Арматурная сетка С-3 М1:50

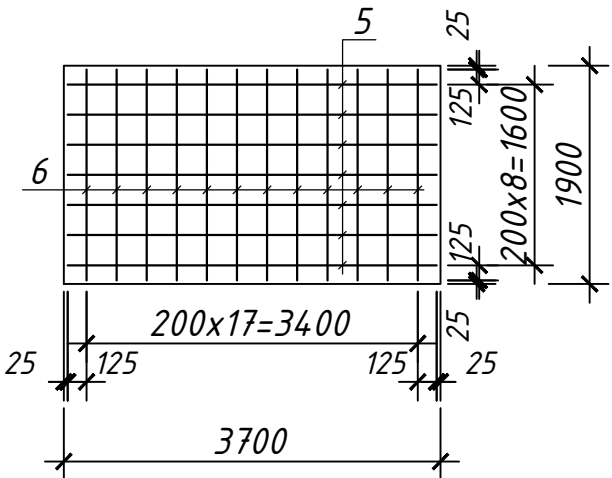

Арматурная сетка С-4 М1:50

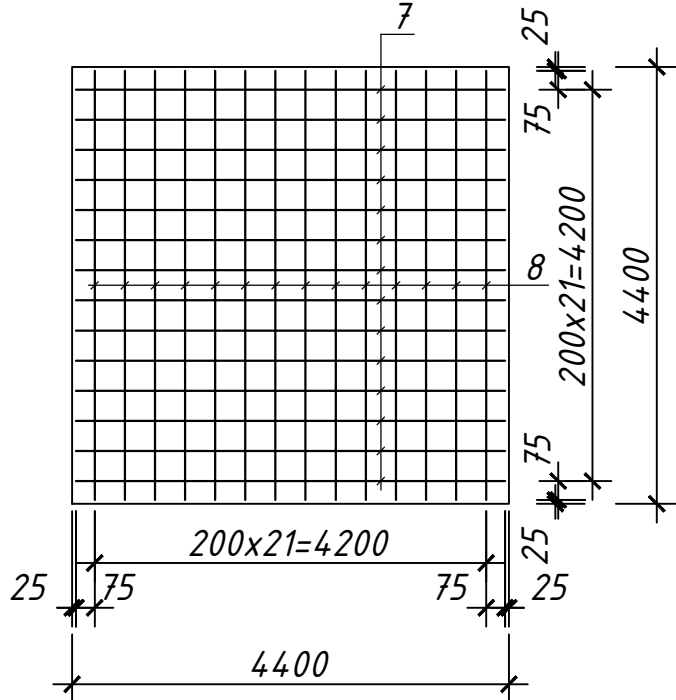

Спецификация материалов на вес фундамент

Поз.	Обозначение	Наименование	Кол-во штук	Масса, ед. кг	Примечание
		Фундамент Ф-1	1		
		Сетка С-1	2	116,6	233,2
1	ГОСТ 5781-93	Ø12 А-III L-3650мм	18,0	3,24	58,3
2	ГОСТ 5781-93	Ø12 А-III L-3650 мм	18,0	3,24	58,3
		Сетка С-2	2	116,6	233,2
3	ГОСТ 5781-93	Ø12 А-III L-3650мм	18,0	3,24	58,3
4	ГОСТ 5781-93	Ø12 А-III L-3650 мм	18,0	3,24	58,3
		Сетка С-3	4	69,5	278,0
5	ГОСТ 5781-93	Ø12 А-III L-3650мм	9,0	3,24	29,2
6	ГОСТ 5781-93	Ø14 А-III L-1850 мм	18,0	2,24	40,3
		Сетка С-4	2	231,0	462,0
7	ГОСТ 5781-93	Ø14 А-III L-4350мм	22,0	5,25	115,5
8	ГОСТ 5781-93	Ø14 А-III L-4350 мм	22,0	5,25	115,5
		Материалы:			
	на фундамент Ф-1	Бетон кл В25 Марка бетона (М350)			26,30м³
	на монолитную плиту	Бетон кл В25 Марка бетона (М350)			6,80м³

Примечание:

Использовать (строго) бетон на сульфатостойком цементе. Класс бетона В25.
Грунты по содержанию сульфатов сильноагрессивные к бетонам на портландцементе по ГОСТ 10178-85*.

Антикоррозийные мероприятия.

В основании фундаментов выполнить гравийную подготовку с пропиткой битумом до насыщения толщиной 30см. Боковые поверхности фундамента, соприкасающиеся с грунтом, обмазать горячим битумом за 2 раза. Общая площадь - 54,5 м2. Объем дан за 2 раза.

Примечание:

- Фундаментную монолитную плиту укладывать над уплотненный ГПС основание. Основание под плиту уплотнить с послойным трамбованием и поливкой водой. Соединения пересечений стержней в сетках вязанные стальной отоженной проволокой Ø=0.8-1.0мм. Применение ручной электродуговой сварки не допускается.
- Расход бетона на 1 фундамент Бетон кл. В25 - 26,30 м³.

Изм.	Кол.уч	Лист	№ док.	Подп.	Дата				
Нач. отд.	Бабаев					Газораспределительная станция	Стадия РП	Лист 1	Листов 1
Исполнит.	Одилов					Фундамент Ф-1 (под пылеуловитель)		 «UZTRANS-GAZ» «TRANSGAZINJINIRING» MCHJ	