

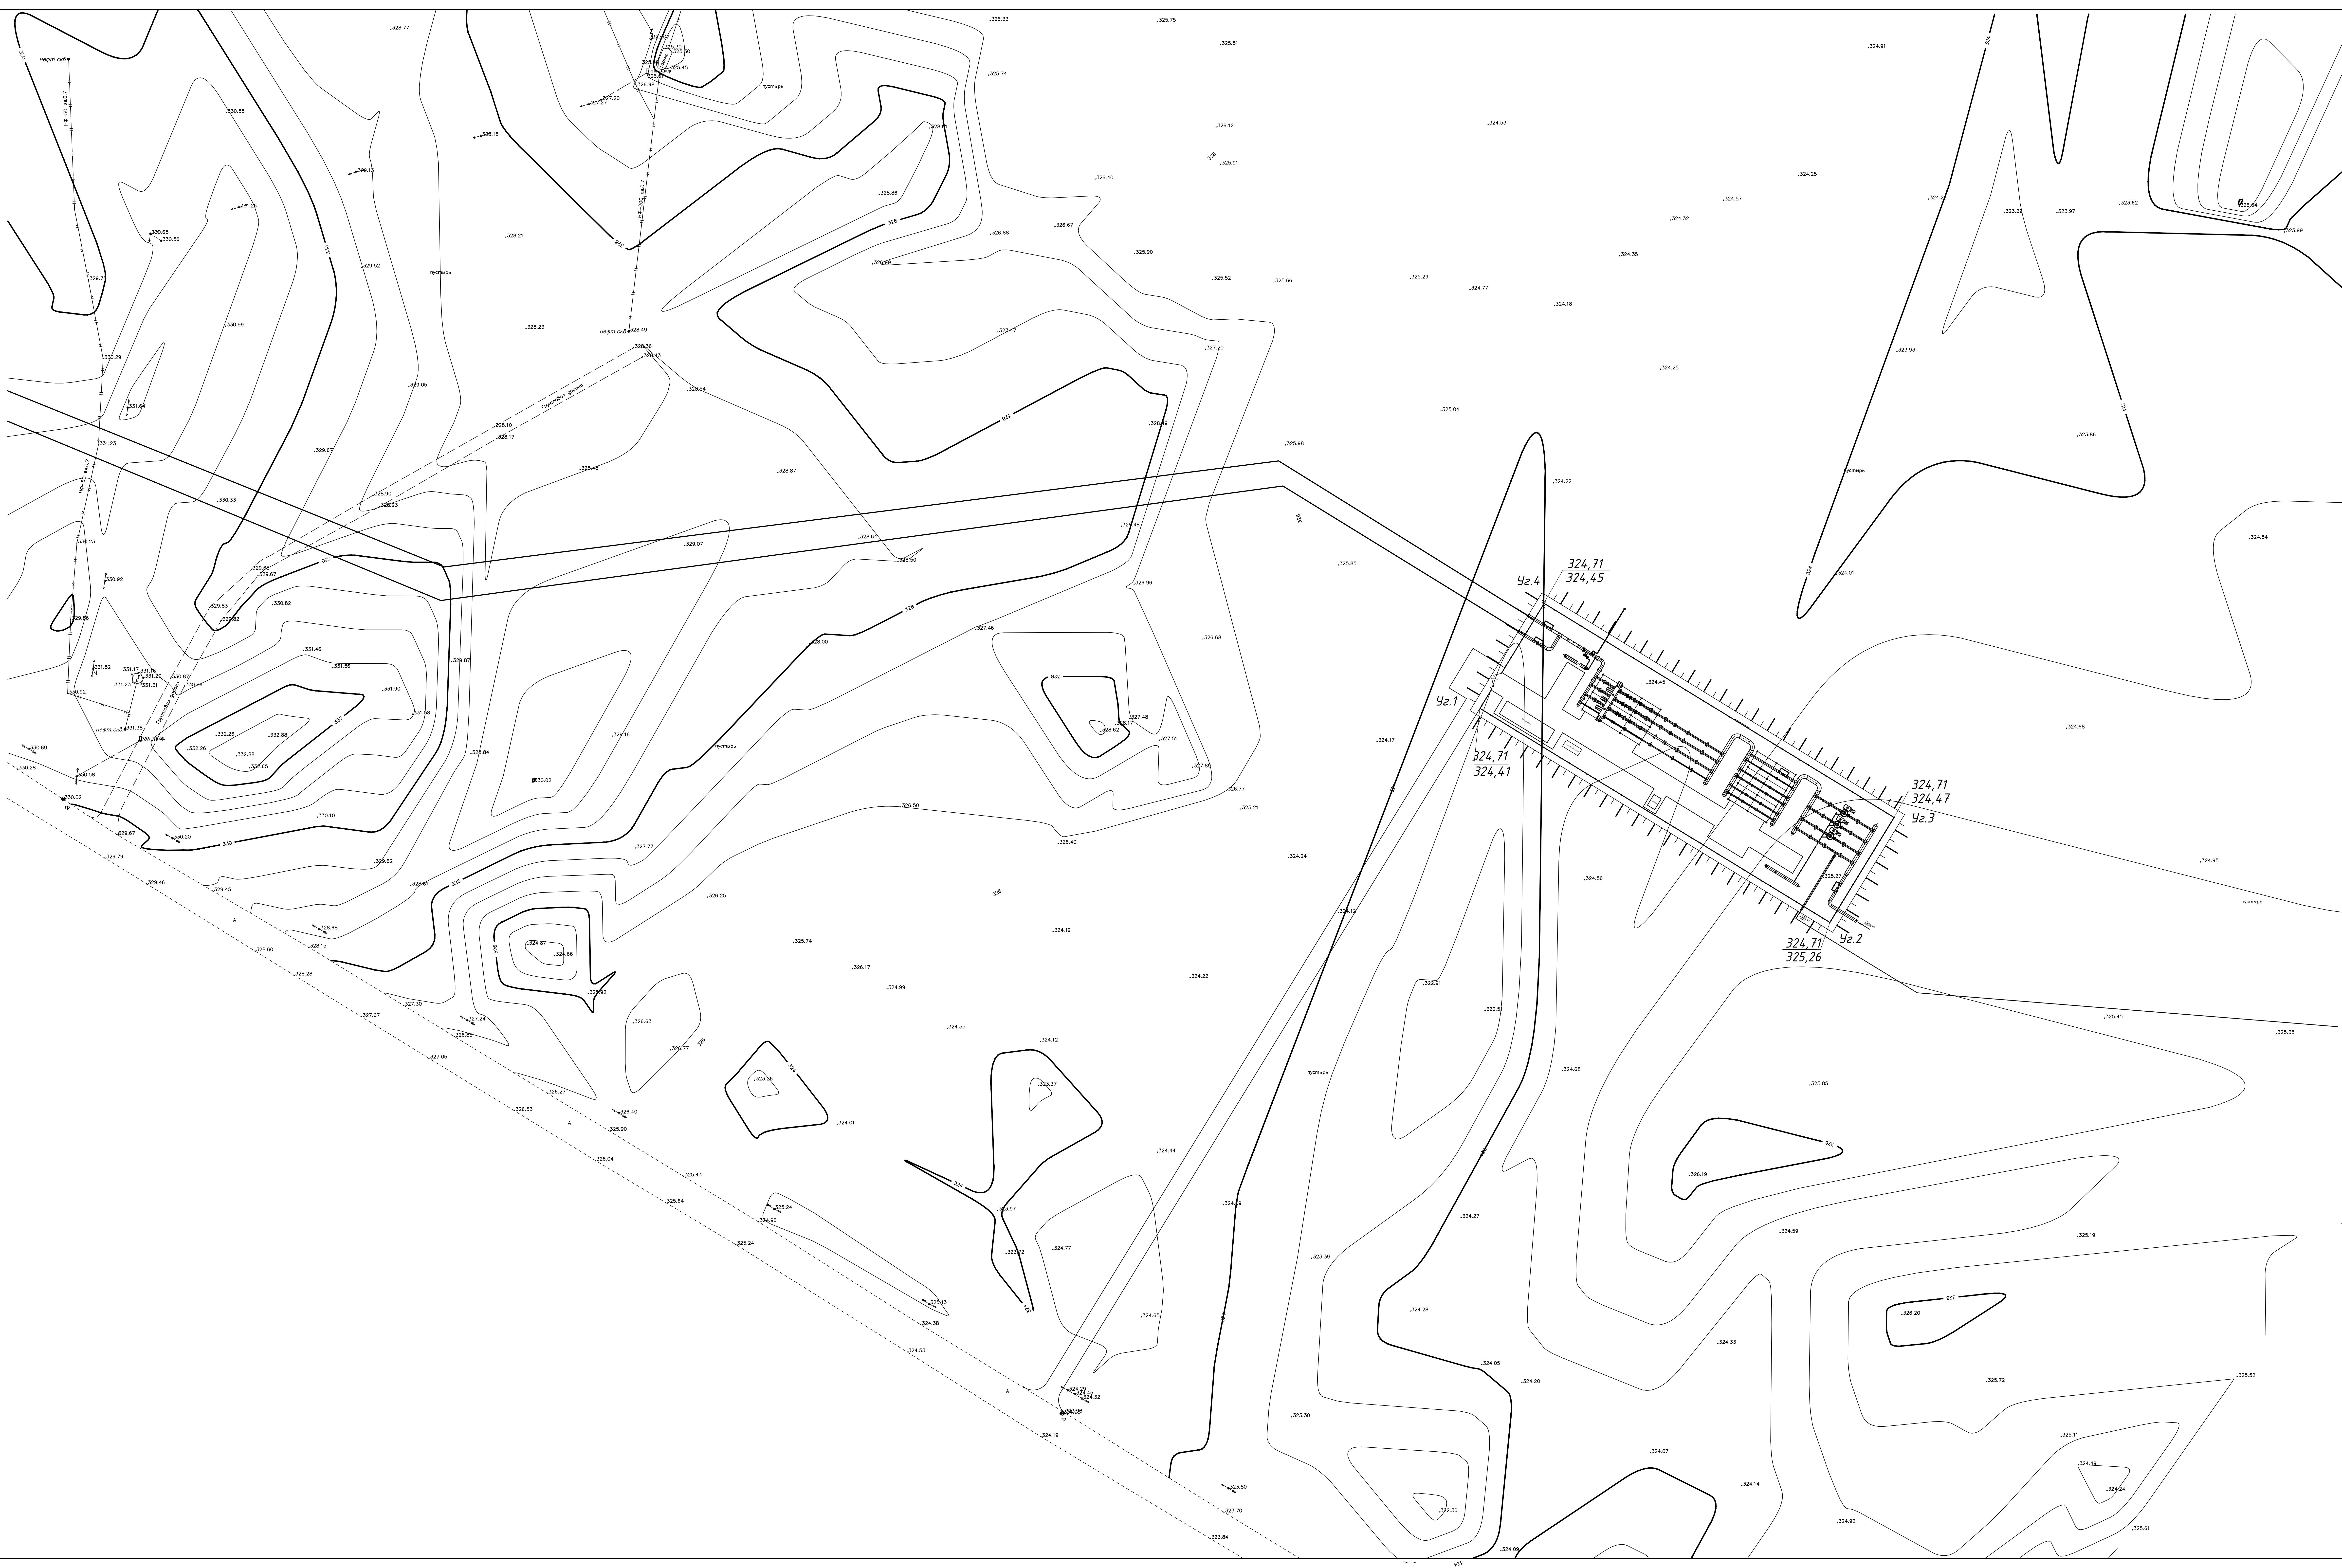


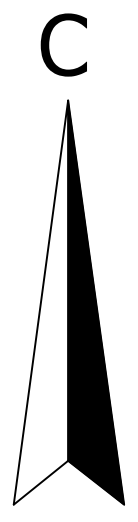


| Ведомость объемов работ площадки ГРС |   |          |               |        |
|--------------------------------------|---|----------|---------------|--------|
| №п/п                                 | Наименование работ                                                                                                   | Ед. изм. | Площадь ГРС   |        |
| 1. Вертикальная планировка           |   |          |               |        |
| 1                                    | Срезка грунта по площадной слое в 1м1 площадки ГРС. Бульдозером Т-132                                                | М3       | 2745,0        |        |
| 2                                    | Позировка с переоборудованием ГРС. Автомобильно-самосвалом на расстоянии до 10 км (до строительной площадки)         | М3       | 2390,0        |        |
| 3                                    | Разработка грунта 2. Грунты в карьерах экскаватором 3-100 с мощностью работы 0,5 м3                                  | М3       | 1900,0        |        |
| 5                                    | Подвозка грунта 2. Грунты. Автомобильно-самосвалом на расстоянии до 10 км с позировкой и выгрузкой.                  | М3       | 1900,0        |        |
| 6                                    | Планировка и переоборудование ГРС. Площадной слое. 30см. Измельчить площадку с помощью бульдозера Т-132              | М2       | 3920,0х2784,0 | 2 слоя |
| 7                                    | Уплотнение насыпного грунта. Катками. Весом до 25 тн                                                                 | М3       | 2390,0        |        |
| 8                                    | Планировка и переоборудование грунта 2. Грунты. Площадной слое. 20см. Измельчить площадку с помощью бульдозера Т-132 | М2       | 3920,0х2784,0 | 2 слоя |
| 9                                    | Уплотнение насыпного грунта. Катками. Весом до 25 тн. Поголово за 5 рядов площадной слое 20 см с помощью воды        | М3       | 1900,0        |        |

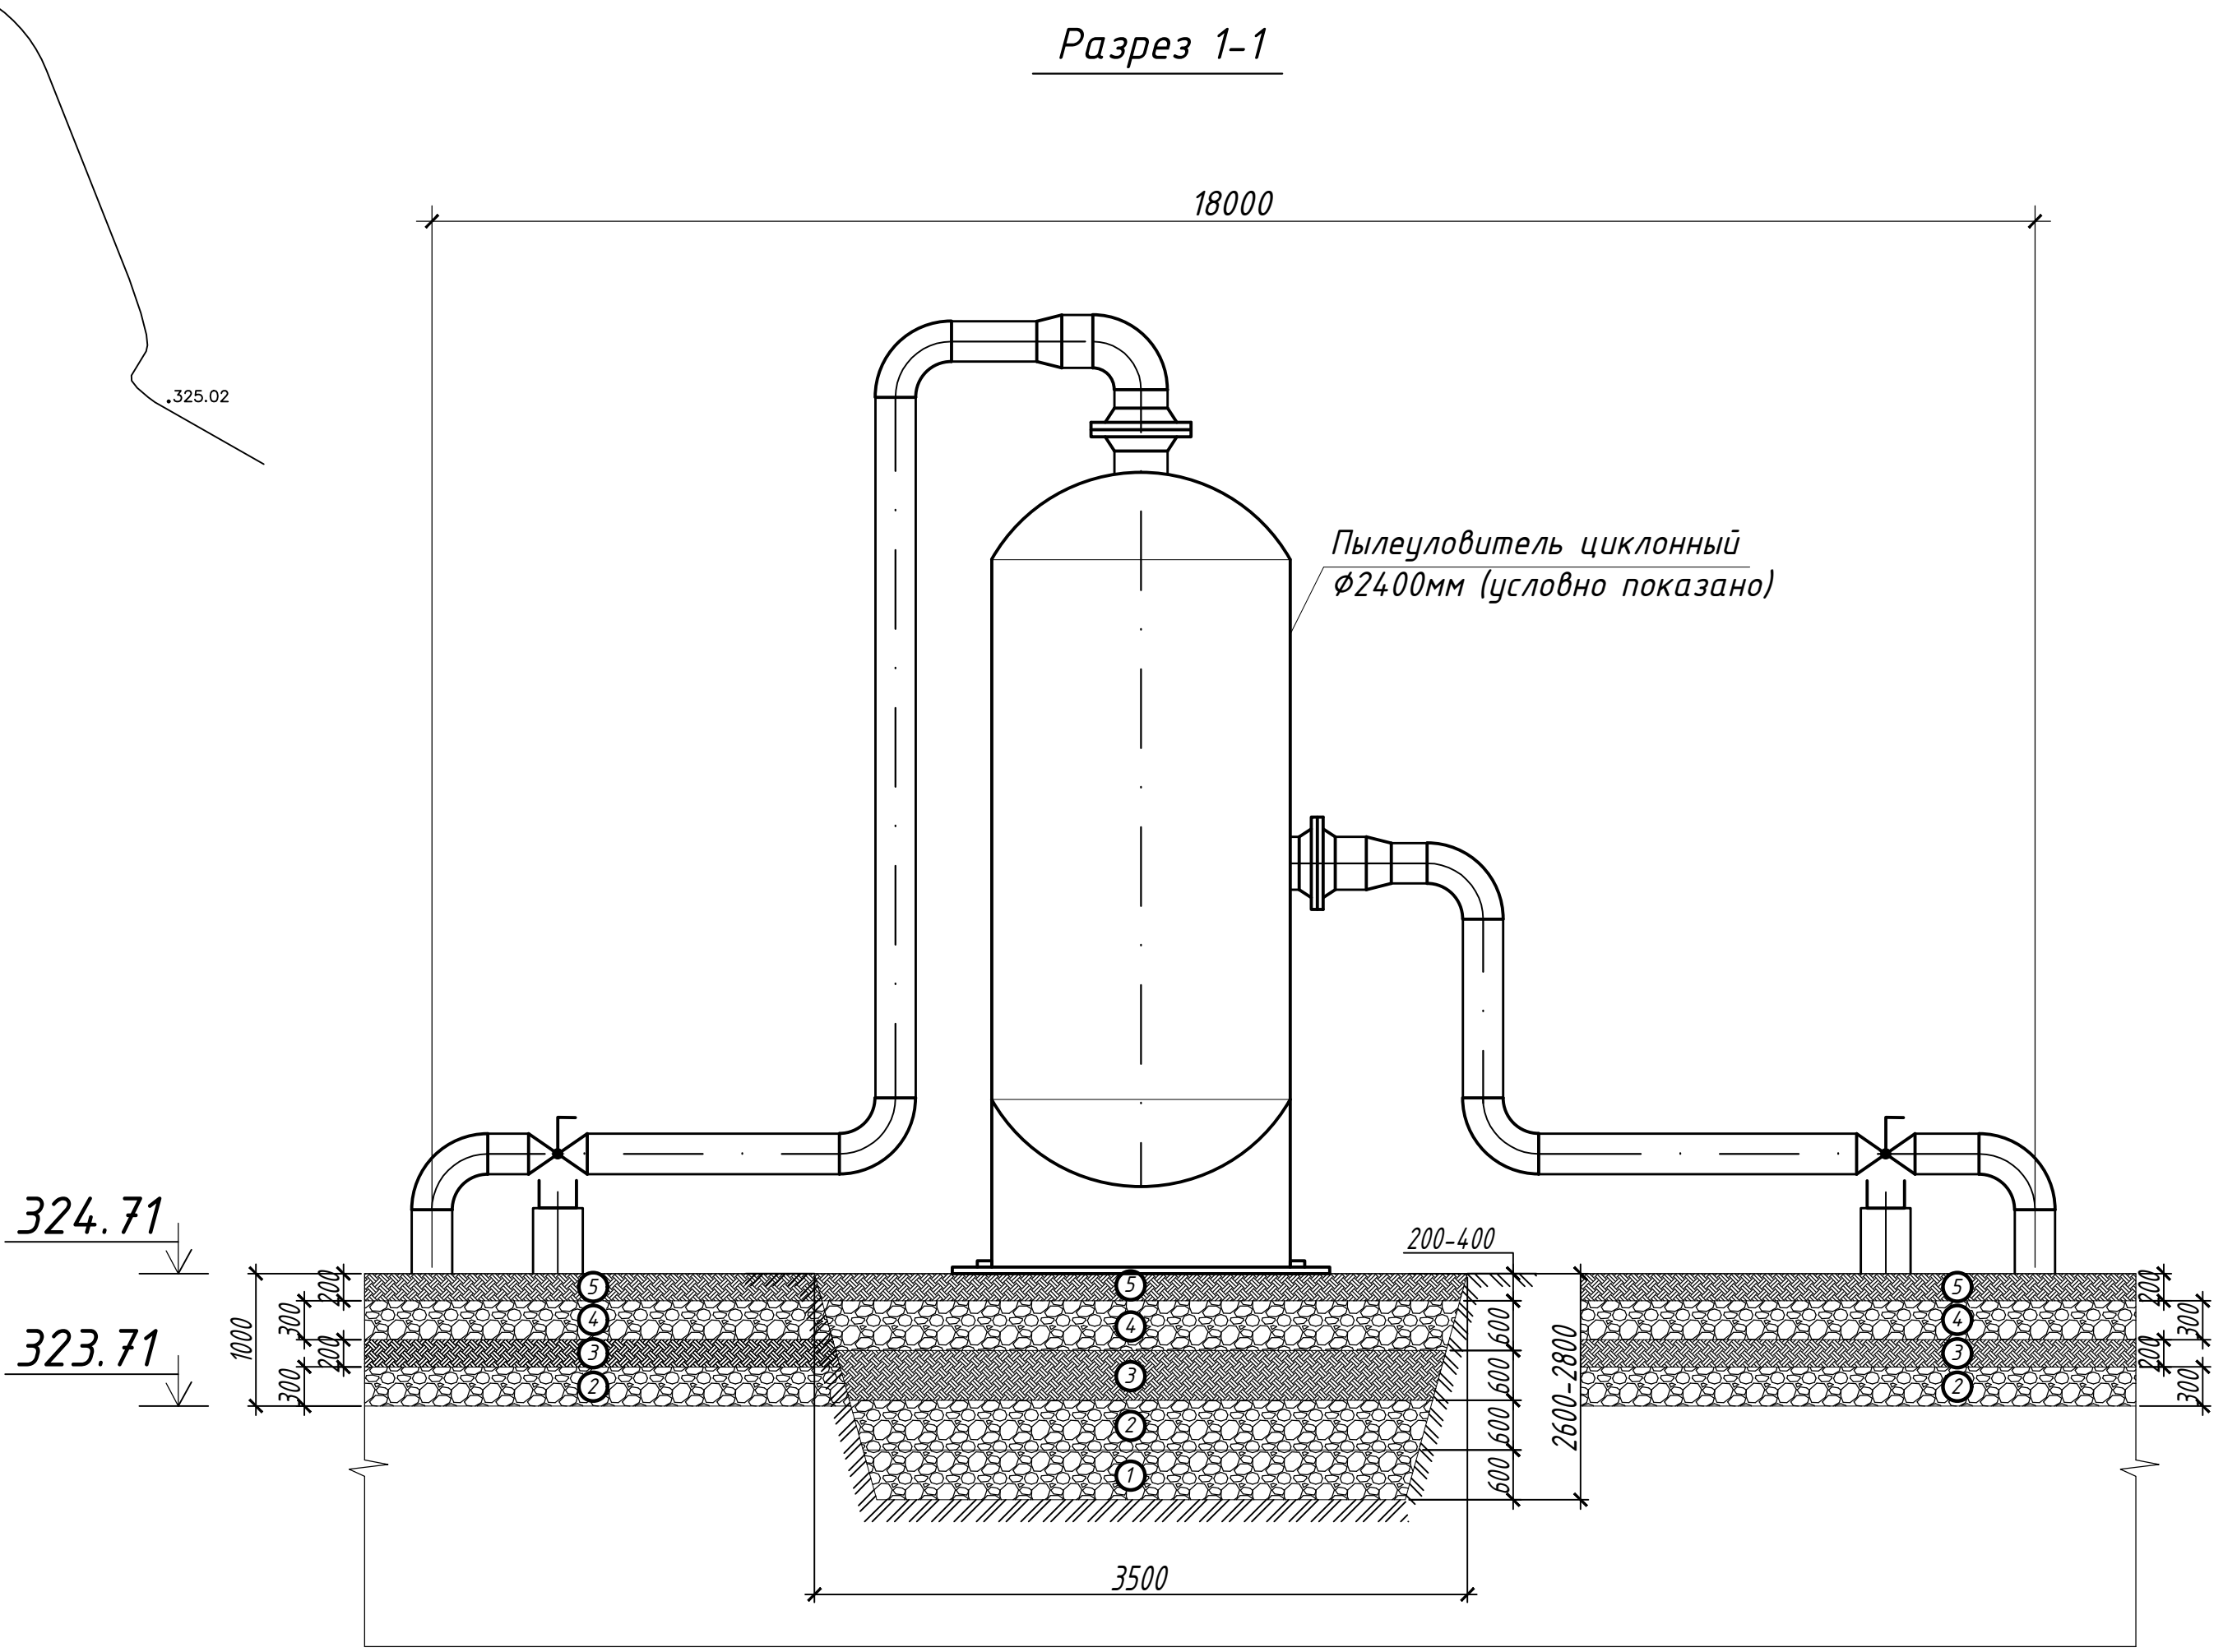

Условные обозначения:

- — Слой из ГПС
- — Слой из уплот-ного грунта

Разбивочный план площадки ГРС М1:500

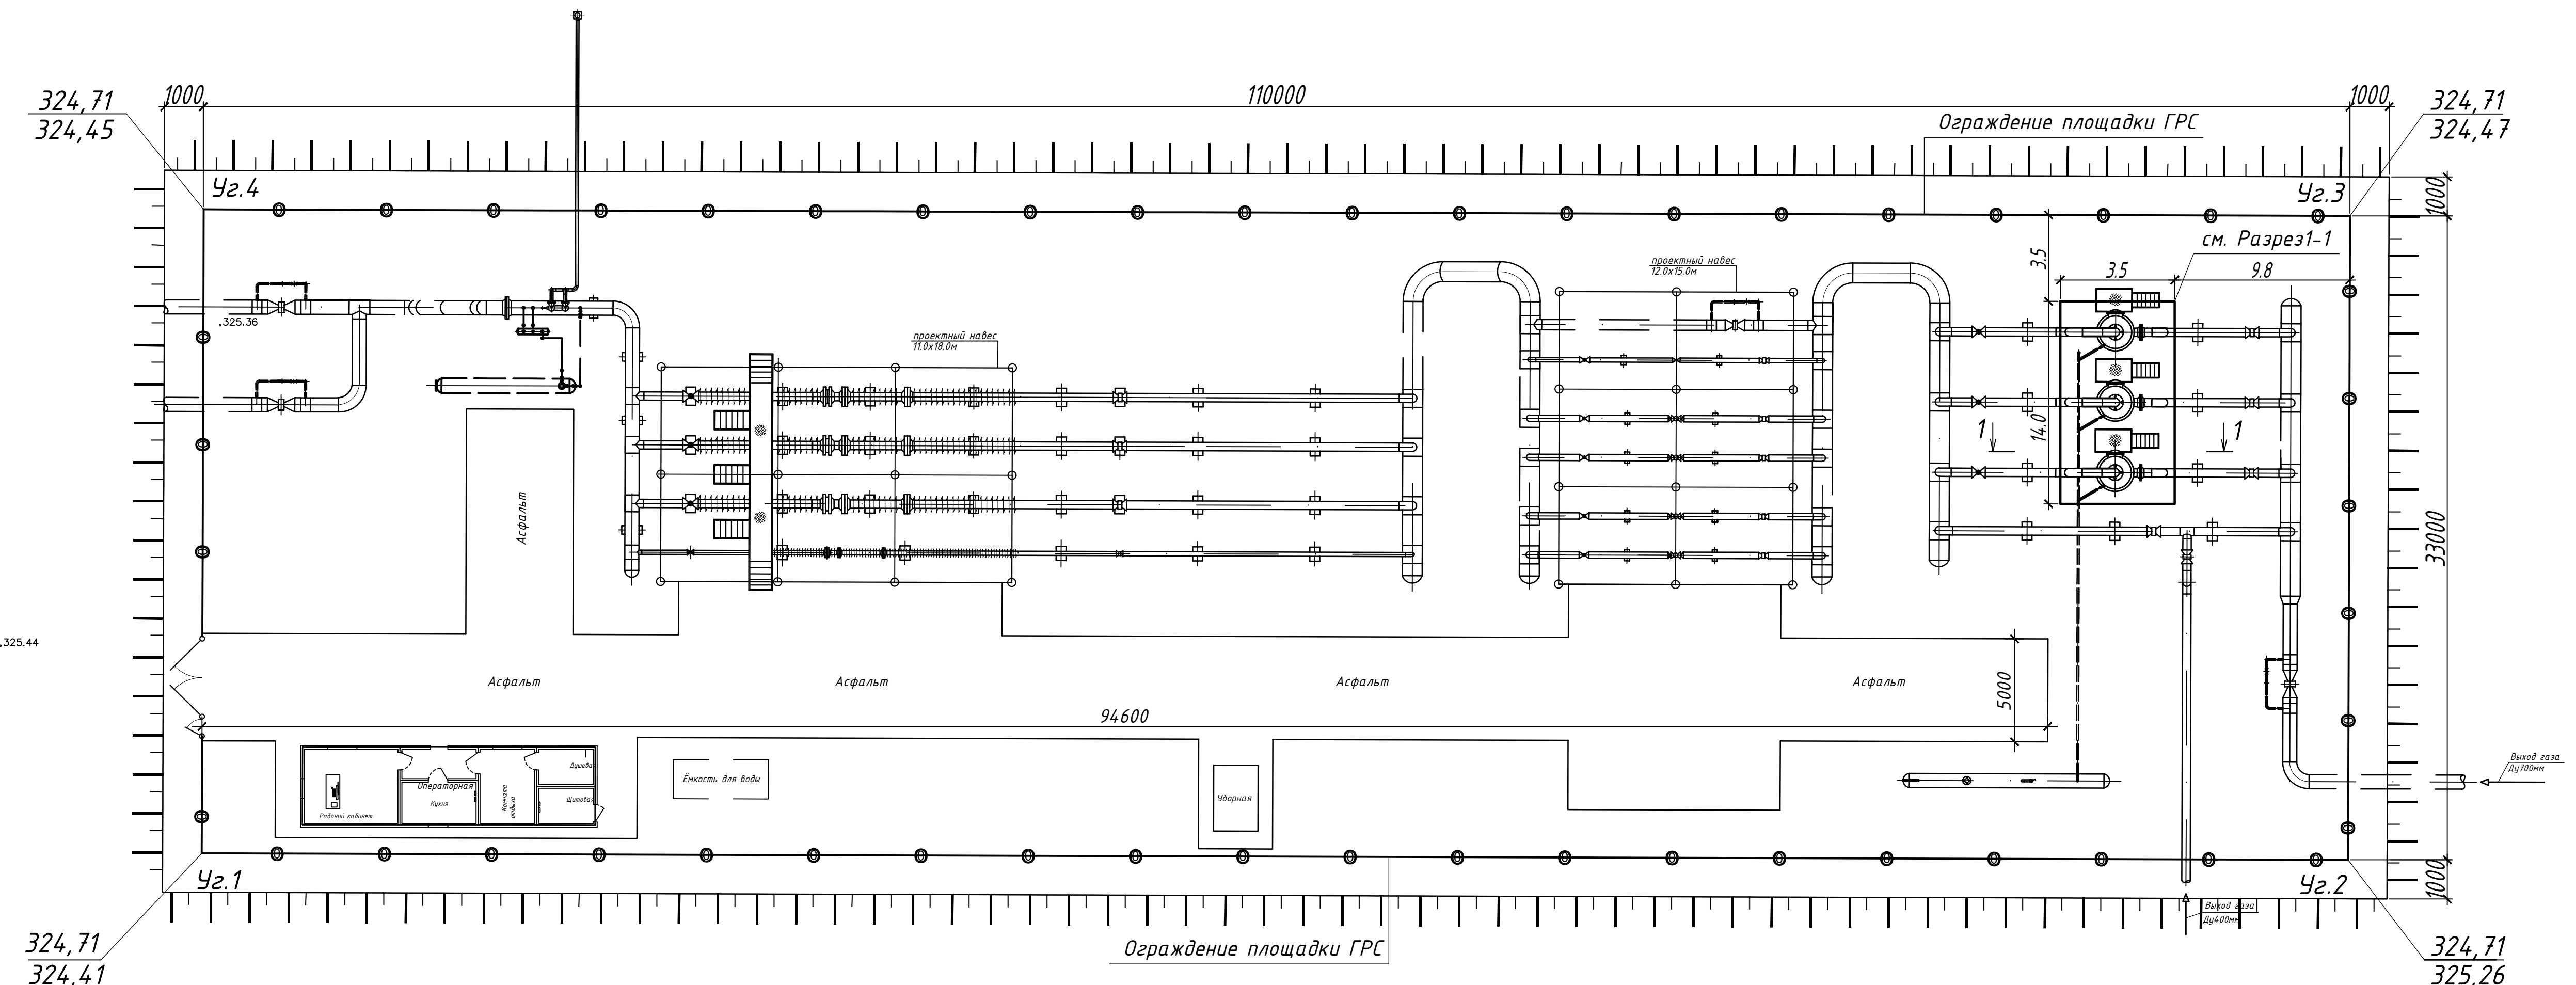

324,71 — Проектная отметка земли  
324,41 — Фактическая отметка земли

Проектируемую площадку ГРС приподнять от отметки 324,41 на 0,3 метров до отметки 324,71 с использованием насыпа из чистого грунта и ГПС.

Примечание :  
1. Данный проект является предварительным для организации строительных (земляных) работ.  
Дата выдачи проекта: 18.06.2026

|                           |                               |        |        |
|---------------------------|-------------------------------|--------|--------|
| Термез новый ГРС          |                               |        |        |
| Имя                       | Кол.                          | Лист   | Листов |
| Содерж.                   | Лист                          | Листов | Листов |
| Масштаб                   | 1:1000                        | РП     | 1      |
| Ситуационный план М1:5000 | Разбивочный план площадки ГРС |        |        |