

Ведомость рабочих чертежей основного комплекта АС

<i>№ п.п.</i>	<i>Наименование</i>	<i>Примечание</i>
<i>1</i>	<i>Общие данные</i>	
<i>2</i>	<i>План стен, фундаментов, стропил. Разрезы.</i>	
<i>3</i>	<i>Монолитная плита П-1. Вытяжная труба Т-1.</i>	
<i>4</i>	<i>Узлы крепления кирпичных стен. Спецификация</i>	

Конструктивные решения

Выгребная цборная имеет размеры в плане 1,76x1,76м.

- фундаменты монолитные бетонные из бетона кл. В-12,5
 - стены кирпичные толщиной 250 мм
 - плита перекрытия монолитная железобетонная из бетона кл. В-15.
 - перекрытие деревянное .
 - кровля из металлочерепицы по деревянной обрешетке из бруска.
 - выгреб перекрывается сборной ж/б плитой П-1 с отверстием Д-700мм.
- Опорное кольцо закрывается чугунным канализационным люком.
- дверь алюминиевый с фрамцгой.

Кладка стен из обыкновенного ж/кирпича М-75 по ГОСТ 530-80 на растворе М-25 с нормальным сцеплением $1.8 \text{ кг/см}^2 \geq R_{\text{тб}} \geq 1.2 \text{ кг/см}^2$. Стены оштукатуриваются цементно-известковым раствором и окрашиваются в/э краской за 2 раза. Деревянные конструкции перекрытия пропитываются антисептиком.

Инструкцию по заполнению проемов см. примечание 5, лист АС-3



Антикоррозионные мероприятия

Все бетонные и ж.б. конструкции выполнить из бетона на сульфатостойком цементе с W4 по водонепроницаемости. Боковые поверхности, соприкасающиеся с грунтом, обмазать горячим битумом за 2 раза. Под подошву ж/б конструкций выполнить щебеночную подготовку толщиной 100мм пролитую битумом.


Взам.инв.№	Боковые поверхности, соприкасающиеся с грунтом, обмазать горячим битумом за 2 раза Под подошву ж/б конструкций выполнить щебеночную подготовку толщиной 100мм пролитую битумом									
Подп. и дата										
Инв.№подл.	Изм.	Кол.	Лист	№док.	Подпись	Дата				
	Нач. отд.		Бабаев				Выгребная уборная на 1 очко	Стадия	Лист	Листов
								РП	1	4
	Исполнит.		Одилов				Общие данные	 UZTRANS-GAZ «TRANSGAZINJINIRING» MCHJ		

МП-1




Спецификация материалов на плиту П-1

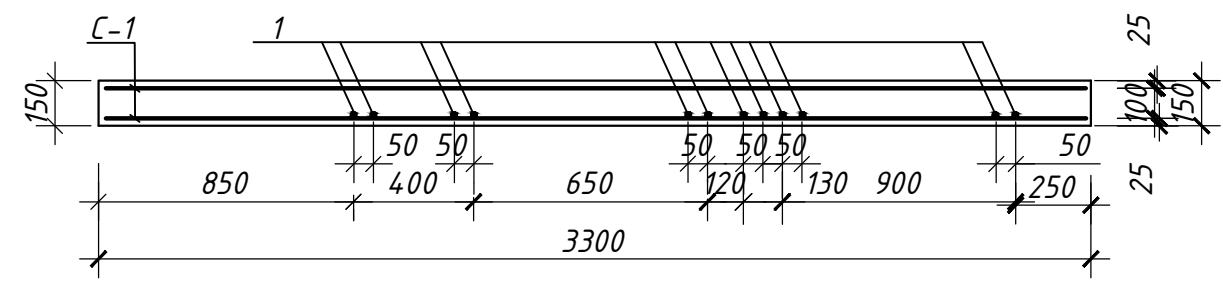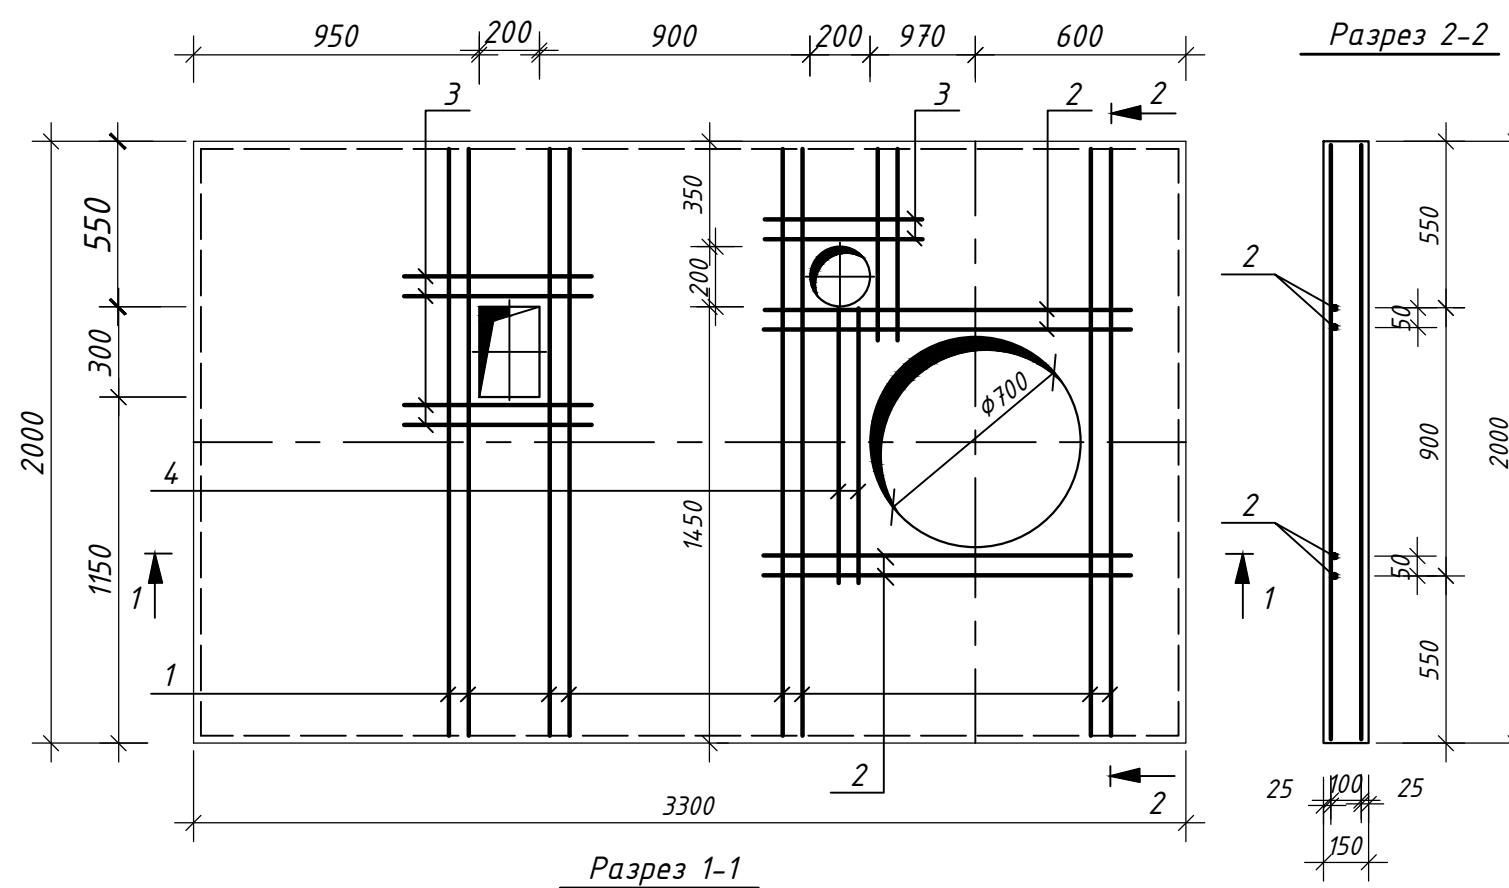

Монолитная Балка Б-1

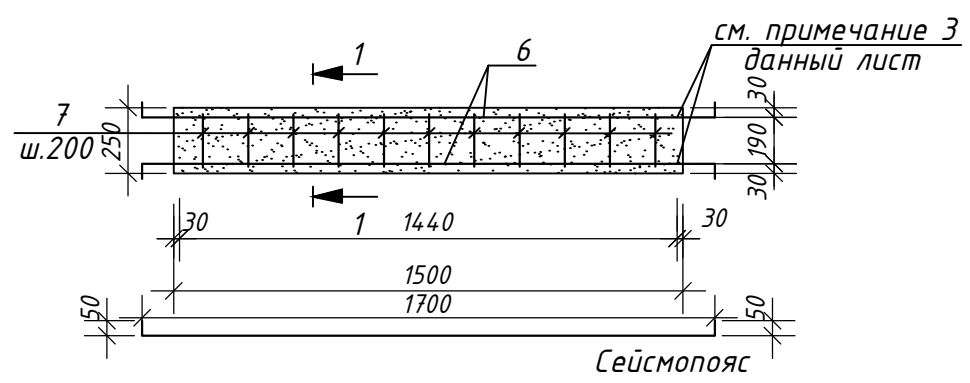

Сейсмопояс

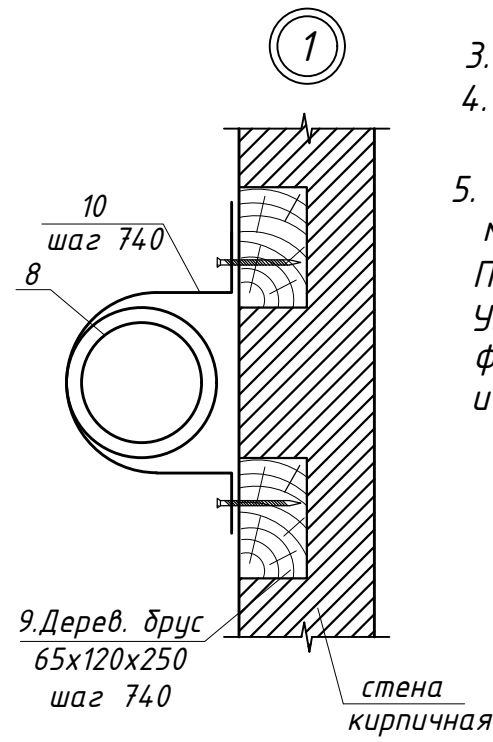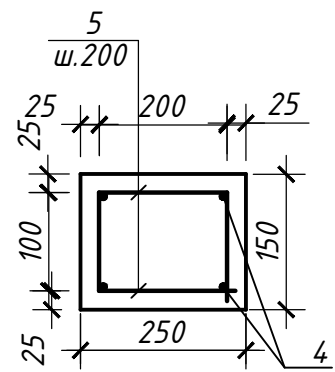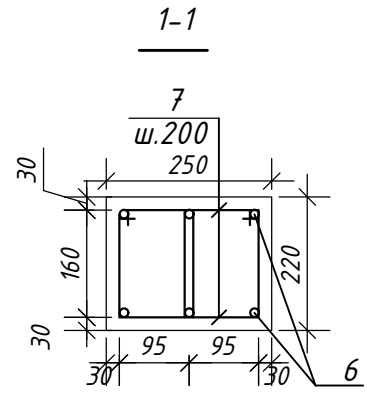

Марка Поз.	Обозначение	Наименование	Кол-во шт	Масса ед. кг.	Примеч.
Сборочные единицы					
С-1	РСТ Уз 866-98	Сетка $\phi 6A1$ 150x150 1960x3240	2,0	19,7	39,4
1	ГОСТ 5781-93	$\phi 10 A1$ L- 1960мм	8,0	1,21	9,7
2	ГОСТ 5781-93	$\phi 10 A1$ L- 1200мм	4,0	0,74	3,0
3	ГОСТ 5781-93	$\phi 10 A1$ L- 700 мм	6,0	0,43	2,6
Материалы:					
Бетон Кл. В-15					
0,72 м3					
Сейсмопояс					
4	ГОСТ 5781-93	$\phi 10 AIII$ Лощ- 7600мм	4,0	4,7	18,8
5	ГОСТ 5781-93	$\phi 6 A1$ L- 800мм	38,0	0,18	6,84
Материалы:					
Бетон Кл. В-15					
0,29 м3					
Монолитная Балка					
6	ГОСТ 5781-93	$\phi 12 AIII$ Лощ- 1800мм	6,0	1,60	9,60
7	ГОСТ 5781-93	$\phi 6 A1$ L- 770мм	16,0	0,17	2,72
Материалы:					
Бетон Кл. В-15					
0,083 м3					
Вытяжная труба Т-1					
8	ГОСТ 19034-82	Труба из ПВХ $\phi 250$ L-3800мм	1,0		
9	ГОСТ 24454 - 80*Е	Брус 120x65(h) L-250мм	8,0	0,002 м3	0,016 м3
10	ГОСТ 103-2006	-4x40, L-980	4,0	1,23	4,92
11	5.904 - 51	Круглый зонт $\phi 250$	1,0	2,90	2,90


Примечание:

- Отверстия в сетках вырезать по месту согласно опалубочного чертежа.
 - Отдельные стержни поз. 1,2,3 привязать вязальной проволокой к нижней сетке.
 - Стержни поз. 6 завести в бетон прямка на 150мм, концы арматуры огибать.
 - Для крепление вытяжной трубы Т-1 при кладки стен предусмотреть дерев. брус разм. 65x120x250 с шагом 740мм по вертикали.
 - Размеры дверей и окон уточнить по месту, они даны без учета зазоров между проемами и блоками. Размеры зазоров 30-35мм.
- Проектом представлены монтажные схемы окон и витражей.
Узлы креплений окон и витражей к конструкциям сооружения разрабатываются фирмой изготовителем. Фирма изготовитель уточняет все габариты дверей и окон по фактически выполненным проемам.

Изм.	Кол.уч	Лист	Ндок.	Подп.	Дата			
Нач. отд.	Бадаев					Выгребная уборная на 1 очко		
Исполнит.	Одилов					Монолитная плита П-1. Вытяжная труба Т-1.		
						Стадия	Лист	Листов
						РП	3	
						UZTRANS-GAZ MCHJ		


Деталь установки горизонтальной армирующей сетки СГ-1 в стене

Деталь отмостки

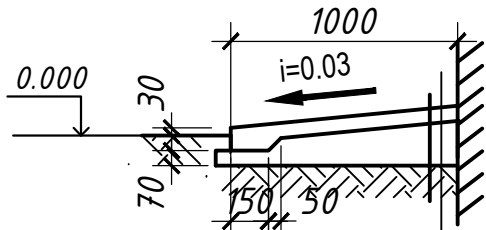


Бетон кл. В7,5 - 50мм
Гравийная подготовка - 100мм.
Уплотненный грунт


Узел пересечения стен

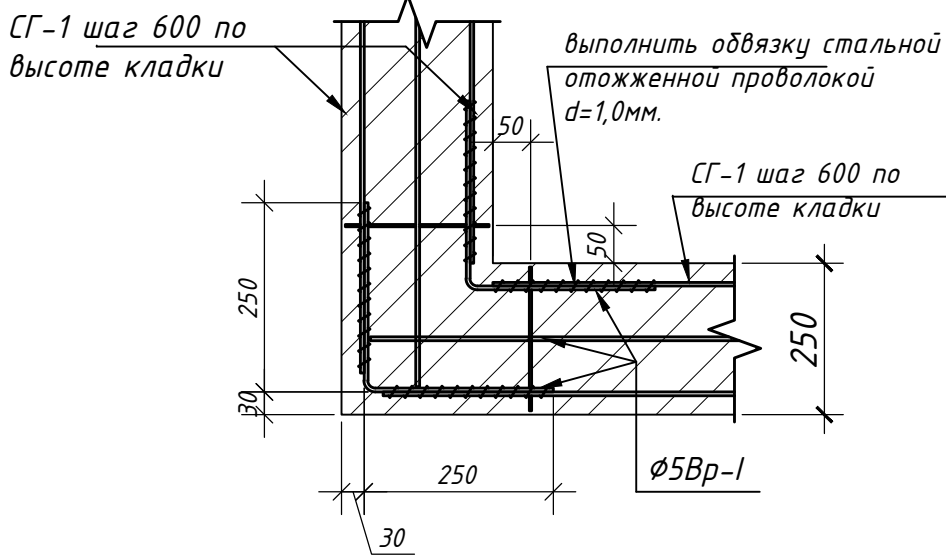

Сетка СГ-1 шаг 600мм по высоте

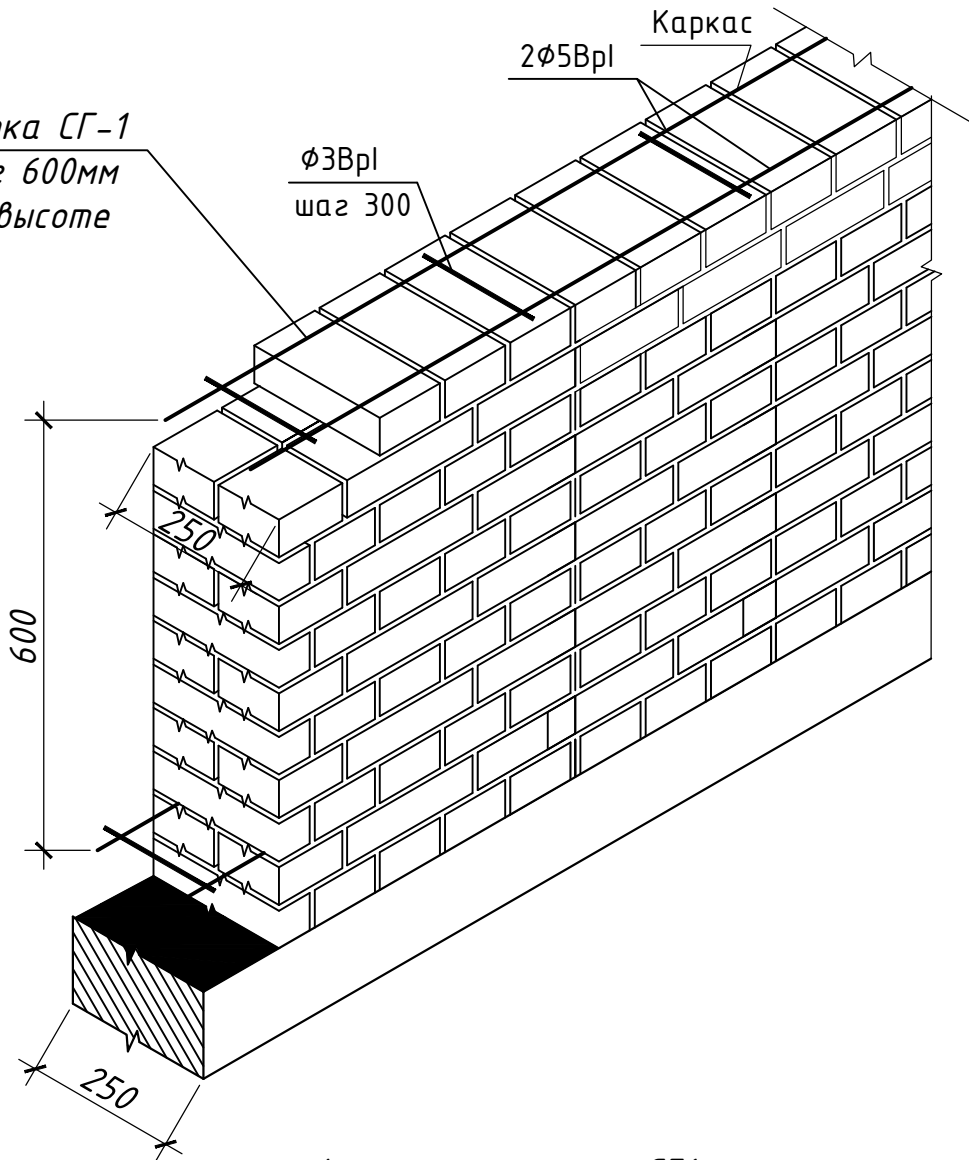


Арматурная сетка СГ1 (разработана на 1 пог.м. длины)

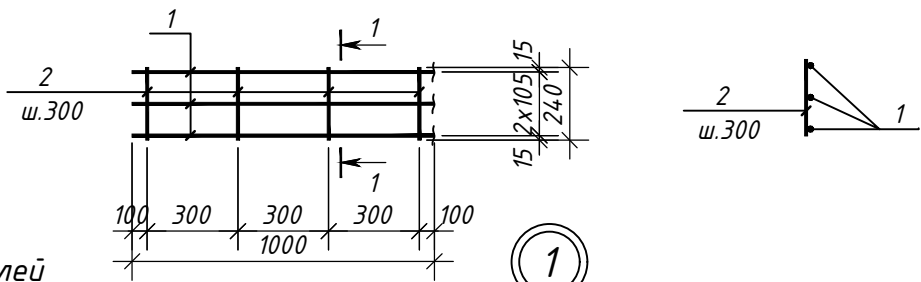


1 - 1

А л.АС-2

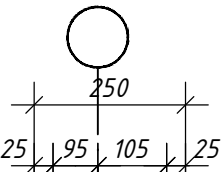

2 - 2

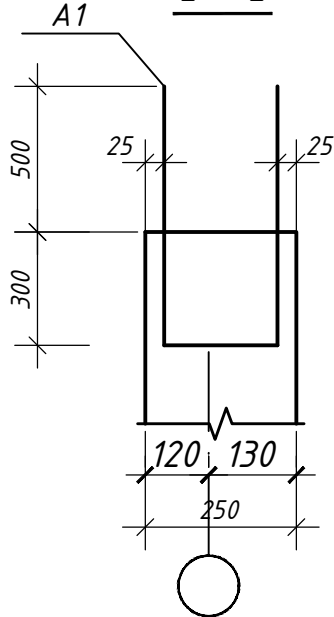


Взам.инв.№

Подп. и дата

Инв.№подл.

Ведомость деталей

Поз.	Эскиз
2	
A1	
5	
7	

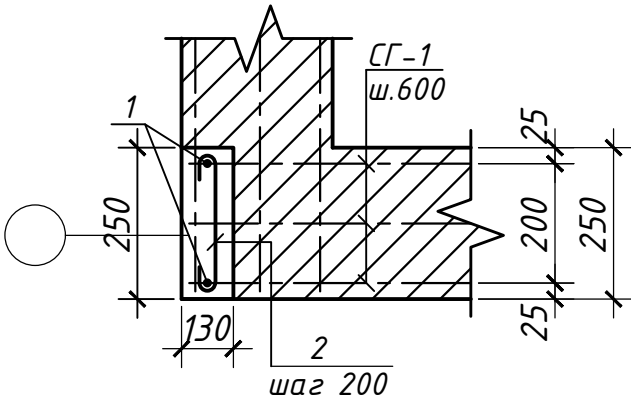

Спецификация элементов монолитных конструкций

Марка Поз.	Обозначение	Наименование	Кол-во шт	Масса ед. кг.	Примеч.
		Сборочные единицы на стены			
		Сетка СГ1	23,7шт		0,515 кг/пог.м.
1	ГОСТ 5781 - 93	Ф5Вр1 L = 1000 мм	3,0	0,154	
2	ГОСТ 5781 - 93	Ф3Вр1 L = 240мм	4,0	0,013	
		Фундамент прямка			
A1	ГОСТ 5781-93	Ф12 АIII Лодж- 1800мм	4,0	1,60	6,40
		Материалы:			
		Бетон Кл. В-15			6,53 м3
См-1		Монолитный сердечник			
4	ГОСТ 5781-93	Ф12 АIII L= 2700мм	8,0	2,4	19,2
5	ГОСТ 5781-93	Ф6 АI L= 250мм	56,0	0,056	3,14
		Материалы:			
		Бетон Кл. В-15			0,34 м3

Ведомость расхода стали

Марка элемента	Изделия арматурные									Общий расход
	Арматура класса									
	А-I			А-III			Вр-I		Итого	
	ГОСТ 5781-93			ГОСТ 5781-93						
	Ø 6	Ø 10	Итого	Ø 12	Ø 10	Итого	Ø 5	Ø 3		
П -1	39,4	15,3	54,7	—	—	—	—	—	—	54,7
Сейсмопояс	6,84	—	6,84	—	18,8	18,8	—	—	—	25,64
Б-1	2,72	—	2,72	9,60	—	9,60	—	—	—	12,32
См-1	3,14	—	3,14	19,2	—	19,2	—	—	—	22,34
Сетка СГ1	—	—	—	—	—	—	11,0	1,23	12,23	12,23
Фундамент	—	—	—	6,40	—	6,40	—	—	—	6,40

Изм.	Кол.ч/лист	Ндок.	Подп.	Дата			
Нач. отд.	Бабаев				Выгребная уборная на 1 очко		
Исполнит.	Одилов				Узлы крепления кирпичных стен		
					Спецификация		
					Стадия	Лист	Листов
					РП	4	
					UZTRANS-GAZ <TRANSGAZINJINIRING> MCHJ		

Инв. № подл.	Исполнит.	Одилов	Подп.	Дата	Изм.	Кол.уч	Лист	№Док.	Подп.	Дата	Выгребная уборная на 1 очко	Стадия	Лист	Листов
												РП	1	2
												 UZTRANSGAZ «TRANSGAZJINIRING» MCHJ		
												Водомонтажные работы		
№ п.п	Наименование работ	Ед. изм.	Кол.
	Уборная на 1 очко		
	1.Земляные работы		
1	Разработка грунта 2 группы экскаватором ковша 0,25 м³ в котловане	м³	58,8
2	Доработка грунта вручную 3 %	м³	1,8
3	Обратная засыпка пазух котлована мех. способом с послойным трамбованием и поливкой водой	м³	40,4
4	Обратная засыпка грунта вручную 3 %	м²	1,4
5	Планировка излишнего грунта по дороге	м³	18,8
	2. Фундаменты		
1	Устройство гравийной подготовки с пропиткой битумом до насыщения толщиной 10 см.	м²	7,7
2	Устройство монолитных ж/б ленточных фундаментов из бетона М-200	м³	6,53
3	Устройство обмазочной гидроизоляции горячим битумом за 2 раза	м²	27,6-за 1 раза. 27,6х2=55,2- за 2 раза
4	Устройство бетонной подготовки внутри ямы для создания уклона из бетона М-100	м³	0,62
5	Арматура Ø12 кл. А-III	Тн	0,0064
6	Устройство монолитной балки из бетона М-200	м³	0,083
7	Арматура Ø12 кл. А-III	Тн	0,0096
8	Арматура Ø6 кл. А-I	Тн	0,0027
9	Устройство ступеньки из бетона М-100	м³	0,15
	3. Плита ПГ-1		
1	Устройство монолитных ж/б плиты перекрытия ямы толщиной 150мм из бетона М-200	м³	0,72
	Арматура Ø10 кл. А-I	Тн	0,0153
	Арматура Ø6 кл. А-I	Тн	0,0394
	4. Стены		
1	Кладка стен из обыкновенного ж/к кирпича М-75 на растворе М-25 высотой до 3-х м.толщиной 250мм	м³	3,8
3	Горизонтальная гидроизоляция стен цементным раствором толщиной 20 мм	м²	1,5
4	Армирование стен сетками из проволоки ВрI	Тн	0,0122
5	Устройство деревянного бруска размером 120х250х65(н)	м³	0,016
6	Полоса из стали толщ. 4х40мм L=980мм	Тн	0,005
7	Устройство монолитного сердечника из бетона М-200	м³	0,34
8	Арматура Ø12 кл. А-III	Тн	0,0192
9	Арматура Ø6 кл. А-I	Тн	0,0032

№ п/п		Наименование работ	Ед. изм.	Кол.	Примеч.
		5. Проемы			
1		Монтаж дверного блока алюминиевый размером 0,9х2,0(н)м площадью S-1,8 м2	шт	1,0	
2		Монтаж фрамуги наружные алюминиевые 0,9х0,6(н)м площадью S-0,54 м2	шт	2,0	
		6. Покрытие			
1		Монтаж деревянных стропил	м³	0,05	
2		Обрешетка из досок 32х120мм	м³	0,076	
3		Устройство монолитного ж/б сейсмопояса из бетона М-200	м³	0,29	
		Арматура Ø10 кл. А-III	Тн	0,019	
		Арматура Ø6 кл. А-I	Тн	0,007	
		7. Кровля			
1		Устройство кровли из металлочерепицы толщ. t=0.5мм с устройством обрешетки	м²	5,5	
2		Монтаж вытяжной ПВХ трубы	пог.м.	3,8	
3		Установка круглого зонта из оцинк.стали Ø250мм	Тн	0,0029	
		8. Полы			
1		Железнение полов раствором толщиной 3 см	м²	2,20	
2		Железнение стен и дна внутри ямы цементным раствором	м²	25,2	
3		Железнение нижней части плиты перекрытия цементным раствором	м²	5,1	
		9. Отделочные работы			
1		Улучшенная штукатурка стен сложным раствором внутри помещения	м²	12,7	
2		Улучшенная окраска стен ПВА за 2 раза	м²	12,7	
3		Улучшенная штукатурка дверных и оконных откосов сложным раствором внутри помещения	м²	1,2	
4		Улучшенная окраска дверных и оконных откосов ПВА за 2 раза	м²	2,4	1,2-за1 раза. 1,2х2=2,4- за 2 раза
5		Затирка потолка	м²	2,4	
6		Улучшенная окраска потолка ПВА за 2 раза	м²	4,8	2,4х2=4,8за2 раза
7		Улучшенная штукатурка стен и цоколя сложным раствором снаружи	м²	18,7	
8		Улучшенная штукатурка откосов сложным раствором снаружи	м²	1,2	
9		Улучшенная окраска стен фасадной краской за 2 раза	м²	34,2	17,1х2=34,2за2раза
10		Улучшенная окраска откосов фасадной краской за 2 раза	м²	2,4	1,2х2=2,4за2раза
11		Антисептирование деревянных конструкций покрытия	м²	5,5	
		10. Разные работы			
1		Устройство бетонной отмостки из бетона М-100 толщиной 30мм по гравийной подготовке толщиной 100мм	м²	9,4	
2		Устройство бетонных крылец из бетона М-100 толщиной 10 см. по гравийной подготовке толщиной 10см.	м²	1,2	
3		Монтаж опорного кольца из сборного ж/б марки КЦО-1 весом -0,033тн, объем бетона -0,13м3	шт	1,0	
4		То же, чугунного люка	шт	1,0	
Инв. N подл.	Подразмещение. N				Лист
					2